Bad DG – Fliesenplan Wände + Boden (Fliesen 60×30, 30 cm versetzt)

0 · Draufsicht Bad (Grundriss)

Norden oben · blau = gefliest (Dusche + Trennwand bis 2,35 m, Fensterwand bis 0,875 m, Waschbeckenwand bis 1,175 m) · orange = Fliesensockel 7 cm · SD = Steckdose · Maße Rohbau lt. Plan

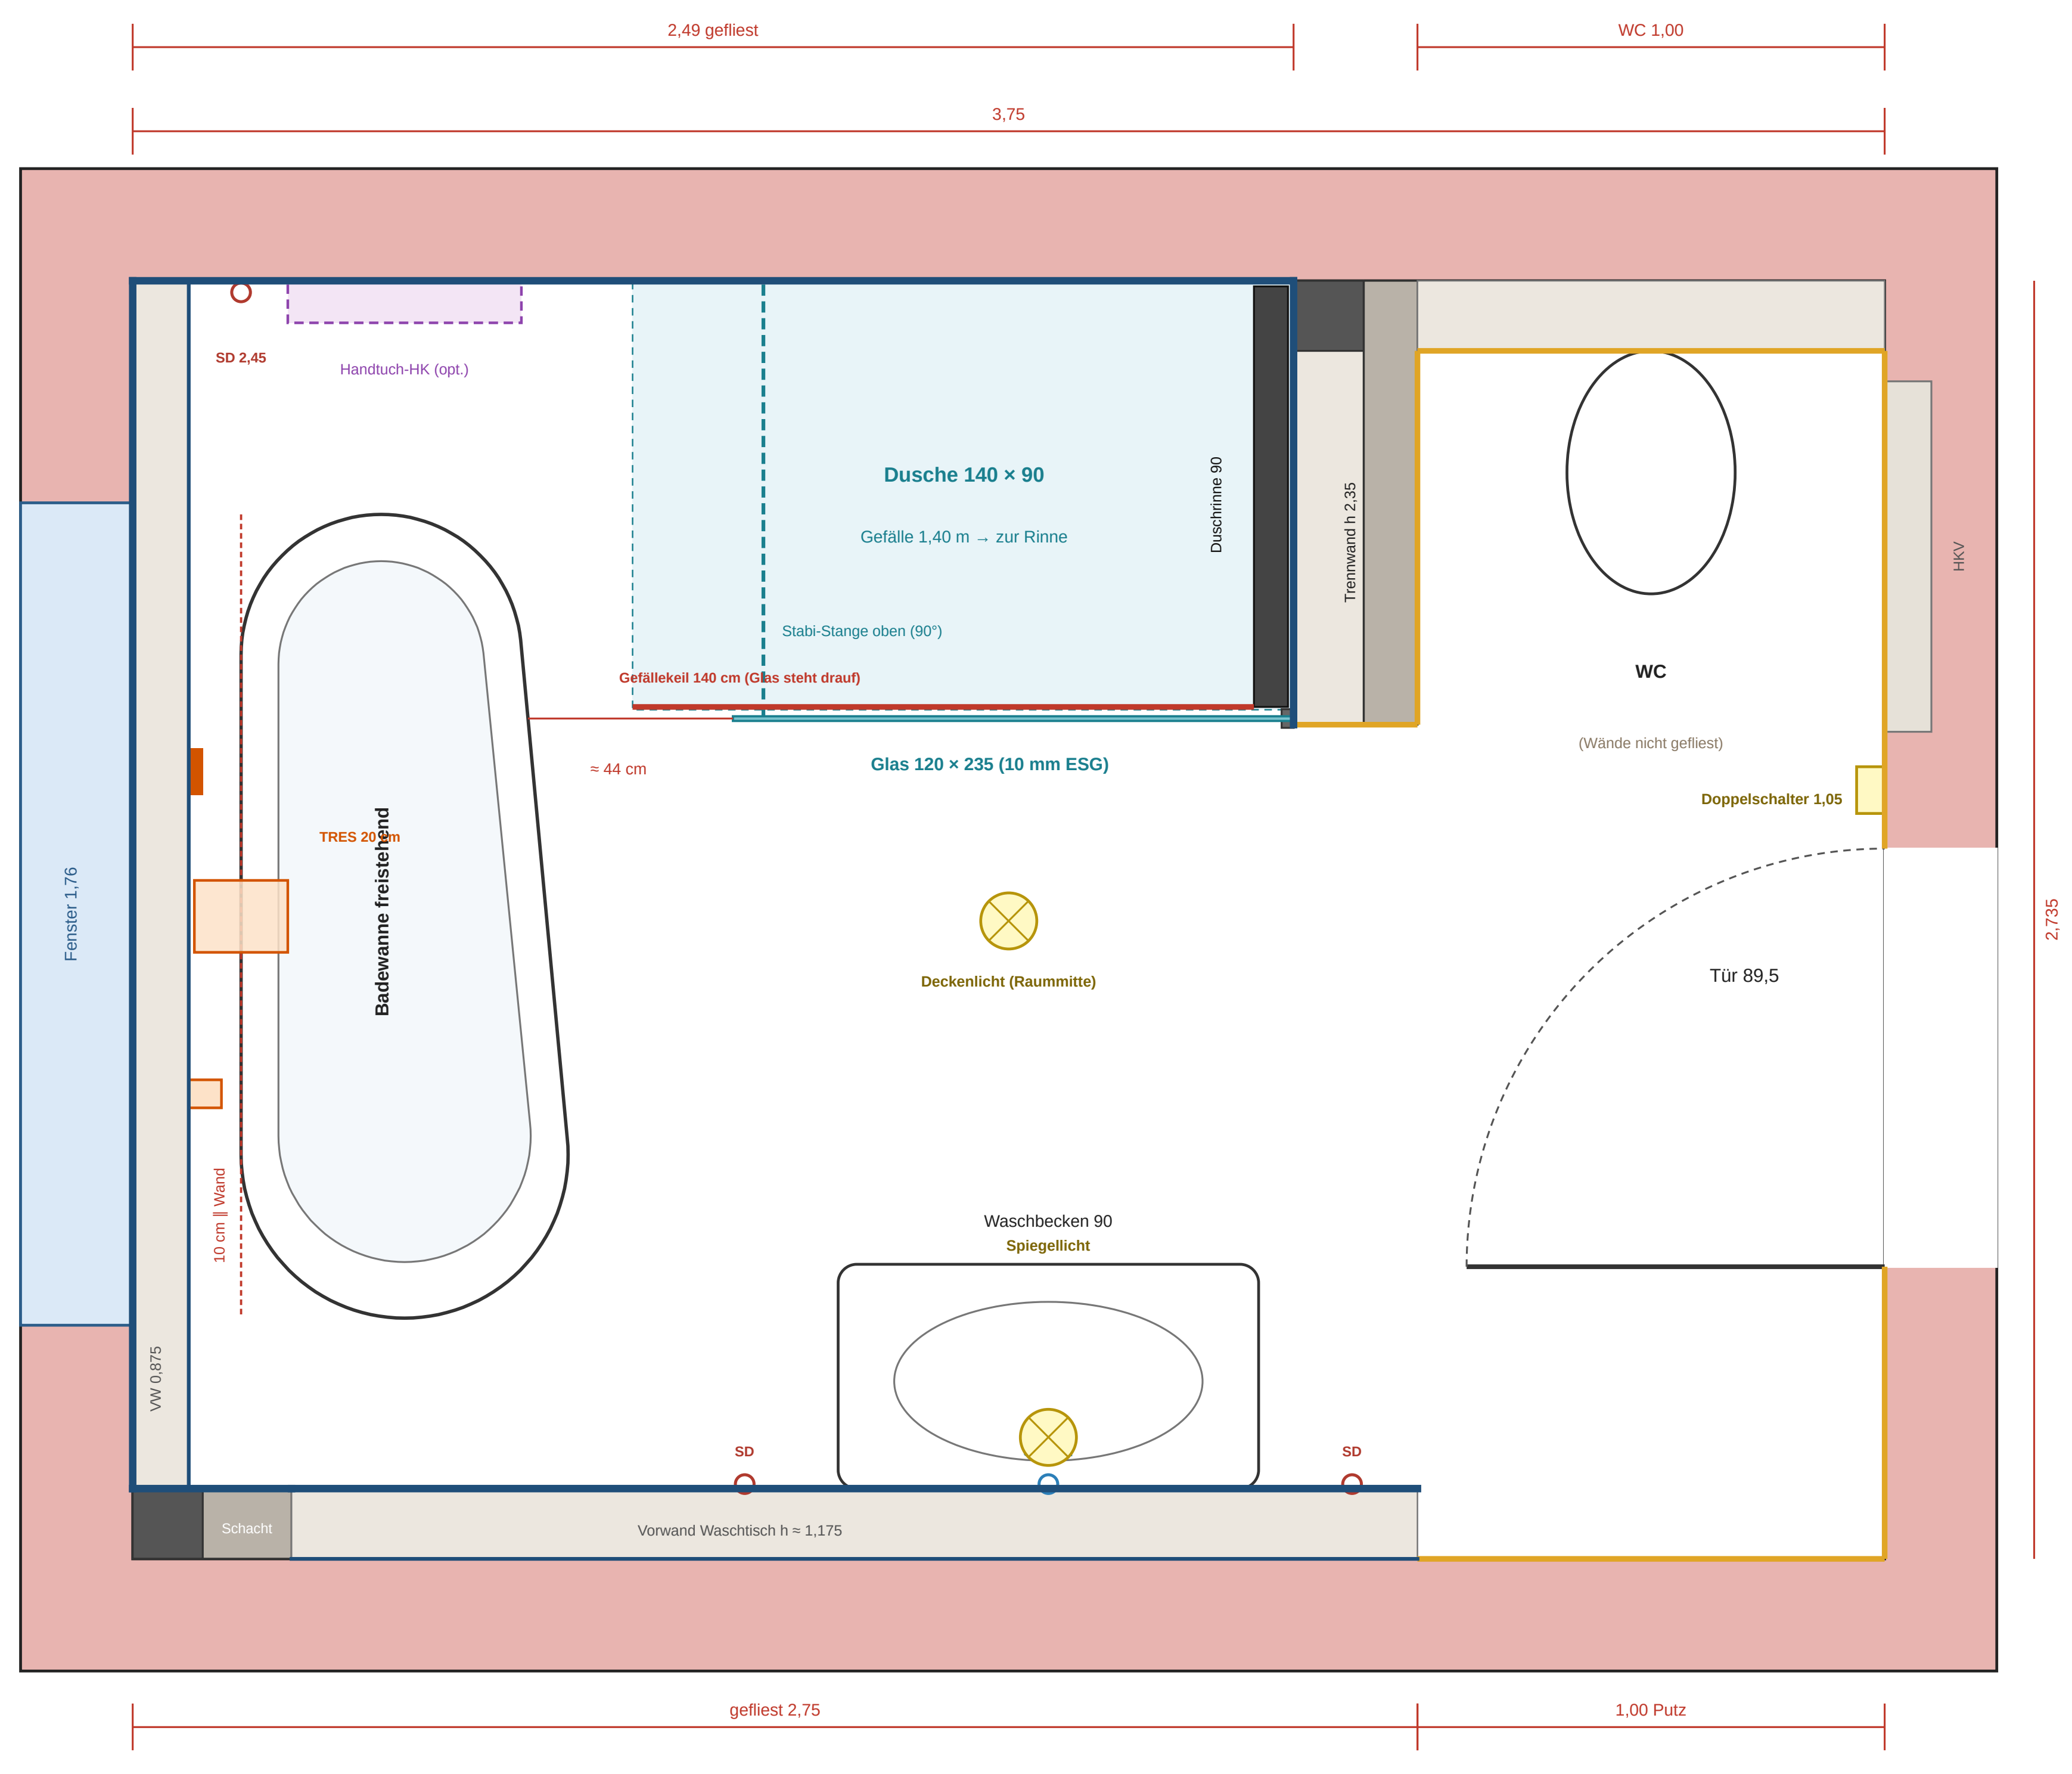
2,49 gefliest
WC 1,00
3,75
SD 2,45
Handtuch-HK (opt.)
Dusche 140 × 90
Gefälle 1,40 m → zur Rinne
Duschrinne 90
Trennwand h 2,35
HKV
Stabi-Stange oben (90°)
Gefällekeil 140 cm (Glas steht drauf)
Glas 120 × 235 (10 mm ESG)
≈ 44 cm
WC
(Wände nicht gefliest)
Doppelschalter 1,05
Fenster 1,76
TRES 20 cm
Badewanne freistehend
Deckenlicht (Raummitte)
Tür 89,5
2,735
10 cm ∥ Wand
Waschbecken 90
Spiegellicht
VW 0,875
SD
SD
Schacht
Vorwand Waschtisch h ≈ 1,175
gefliest 2,75
1,00 Putz

0a · Boden – Fliesen längs (Ost–West), 30 cm versetzt

60×30 · ca. 9,0 m² · ganze Reihen an der Duschwand · Streifen 13,7 cm unter der Waschtisch-Vorwand · Duschrinne 90 cm an der Trennwand, Gefälle über 1,40 m · Gefällekeil 140 cm an der Glaslinie

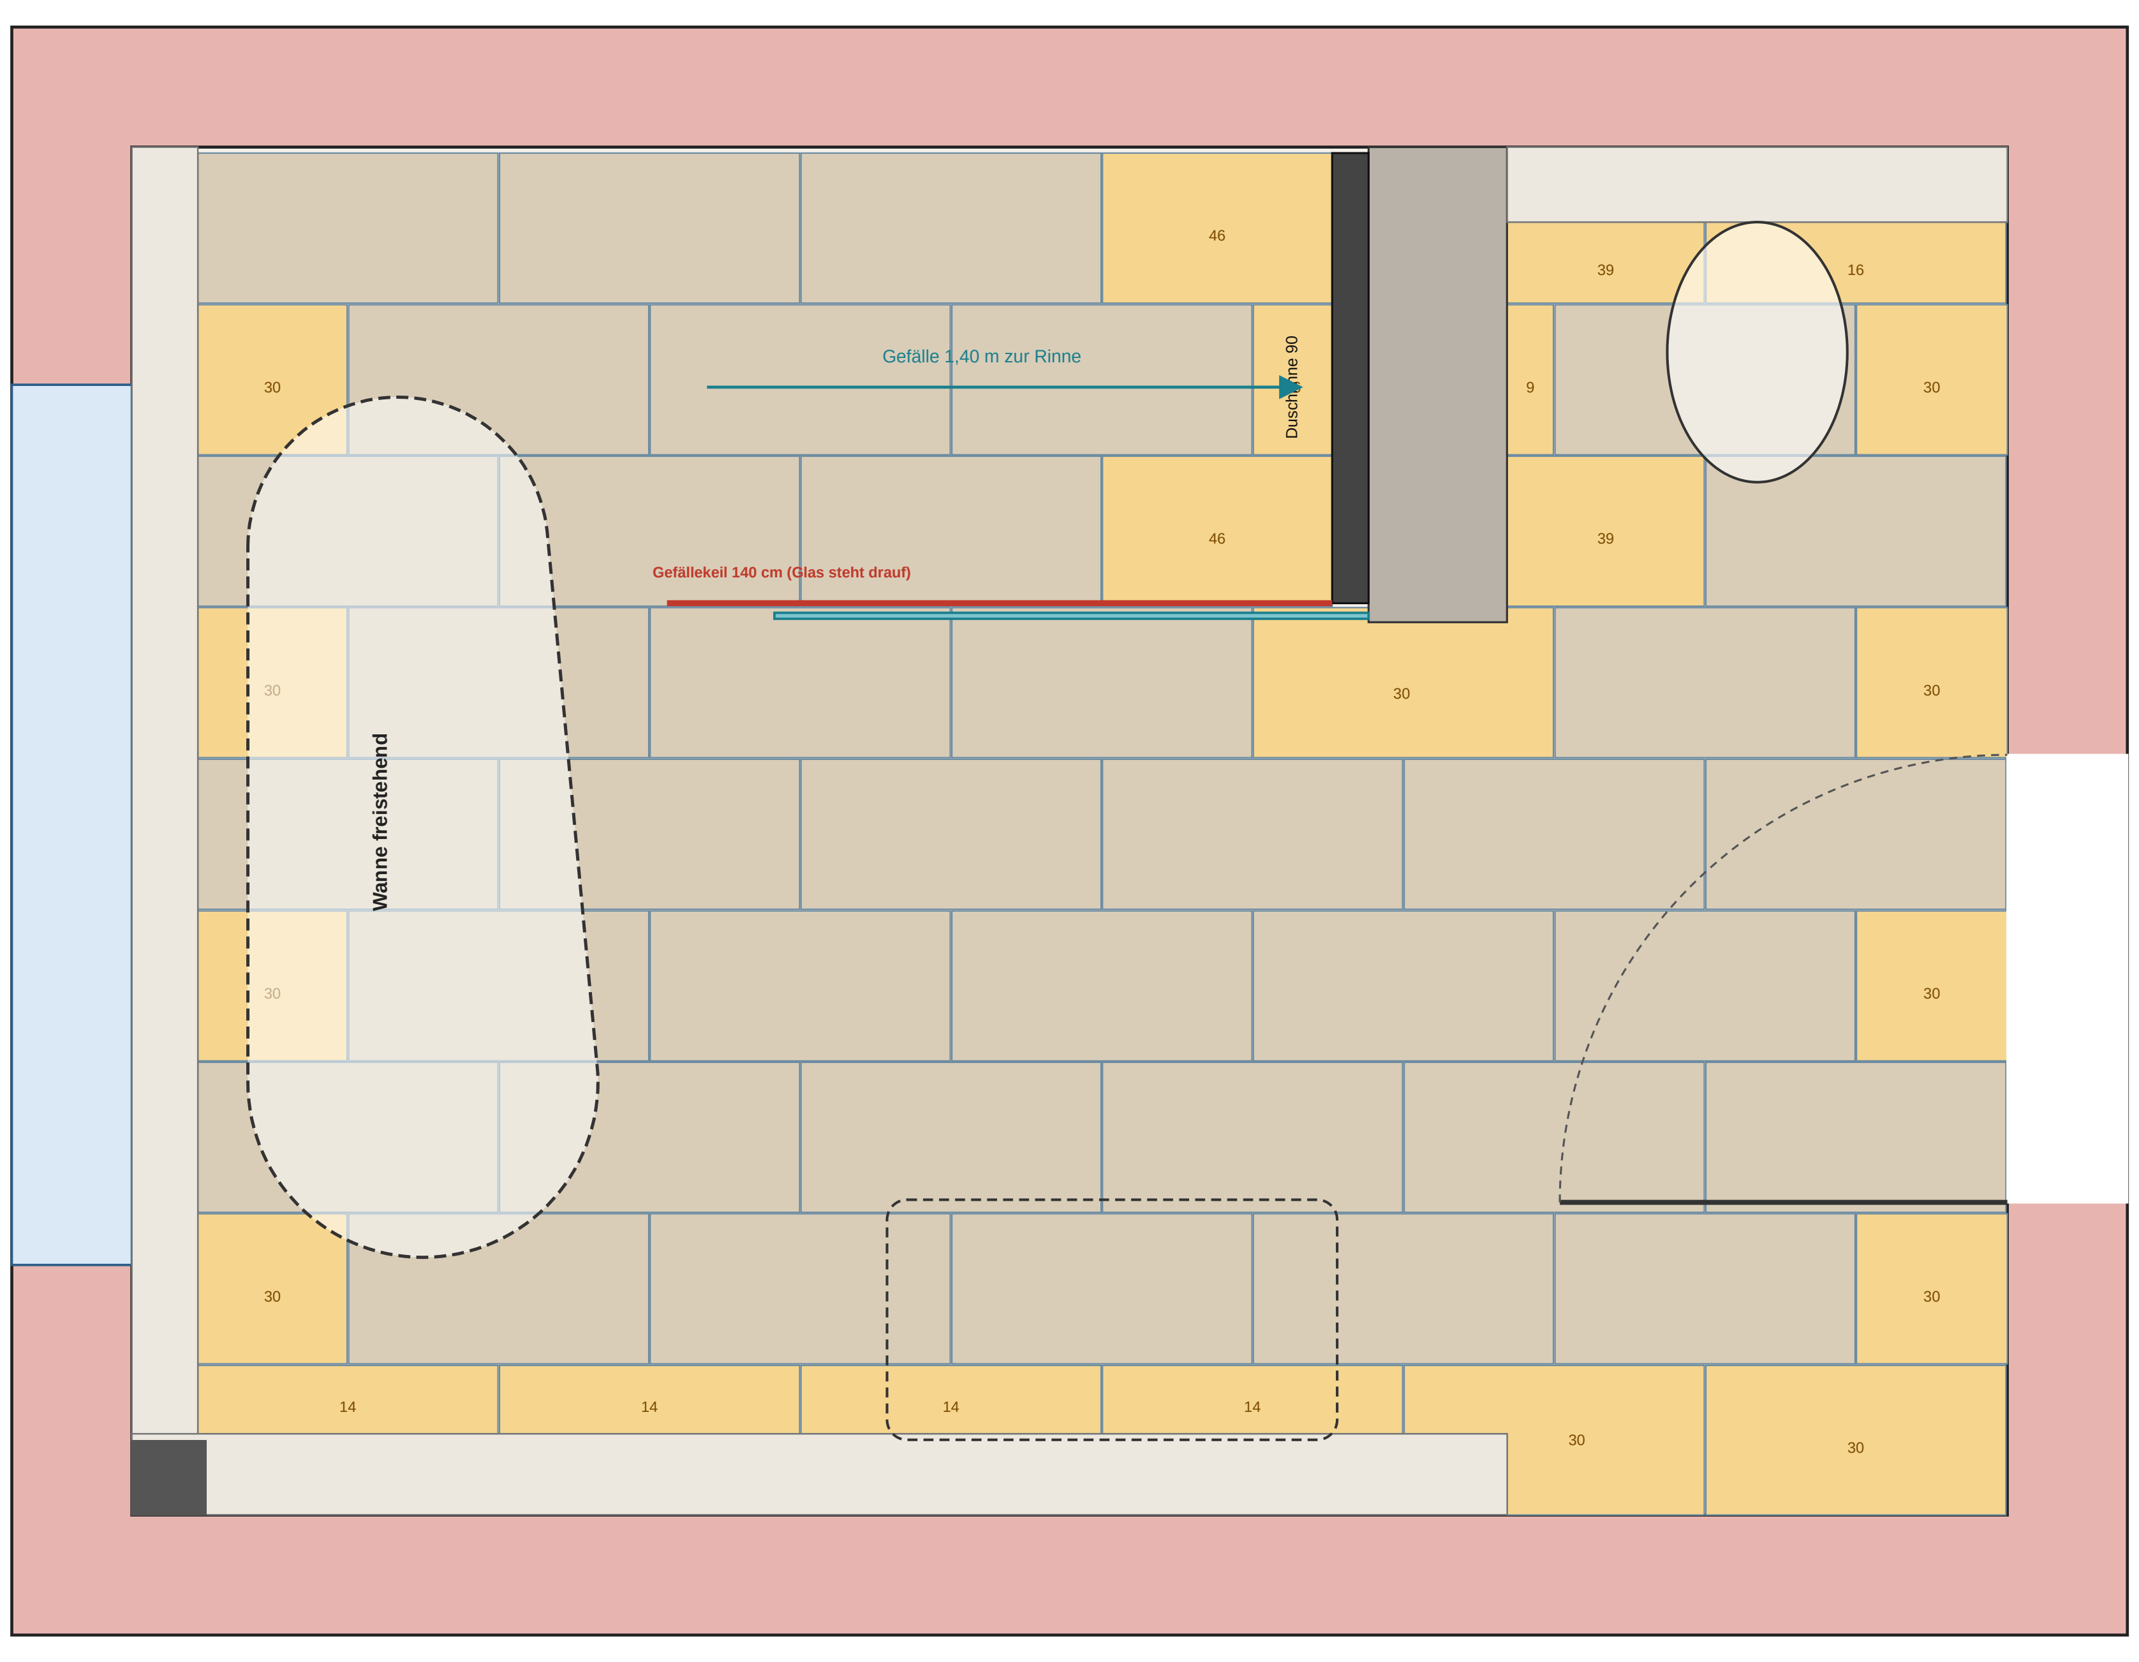
46
39
16
30
Gefälle 1,40 m zur Rinne
Duschrinne 90
9
30
46
39
Gefällekeil 140 cm (Glas steht drauf)
30
30
30
Wanne freistehend
30
30
30
30
14
14
14
14
30
30

1 · Wand Badewanne / Fenster (Westen)

Blick nach Westen · Fliesen nur auf der Vorwand (bis 0,875 m) und oben auf der Ablage, darüber Putz

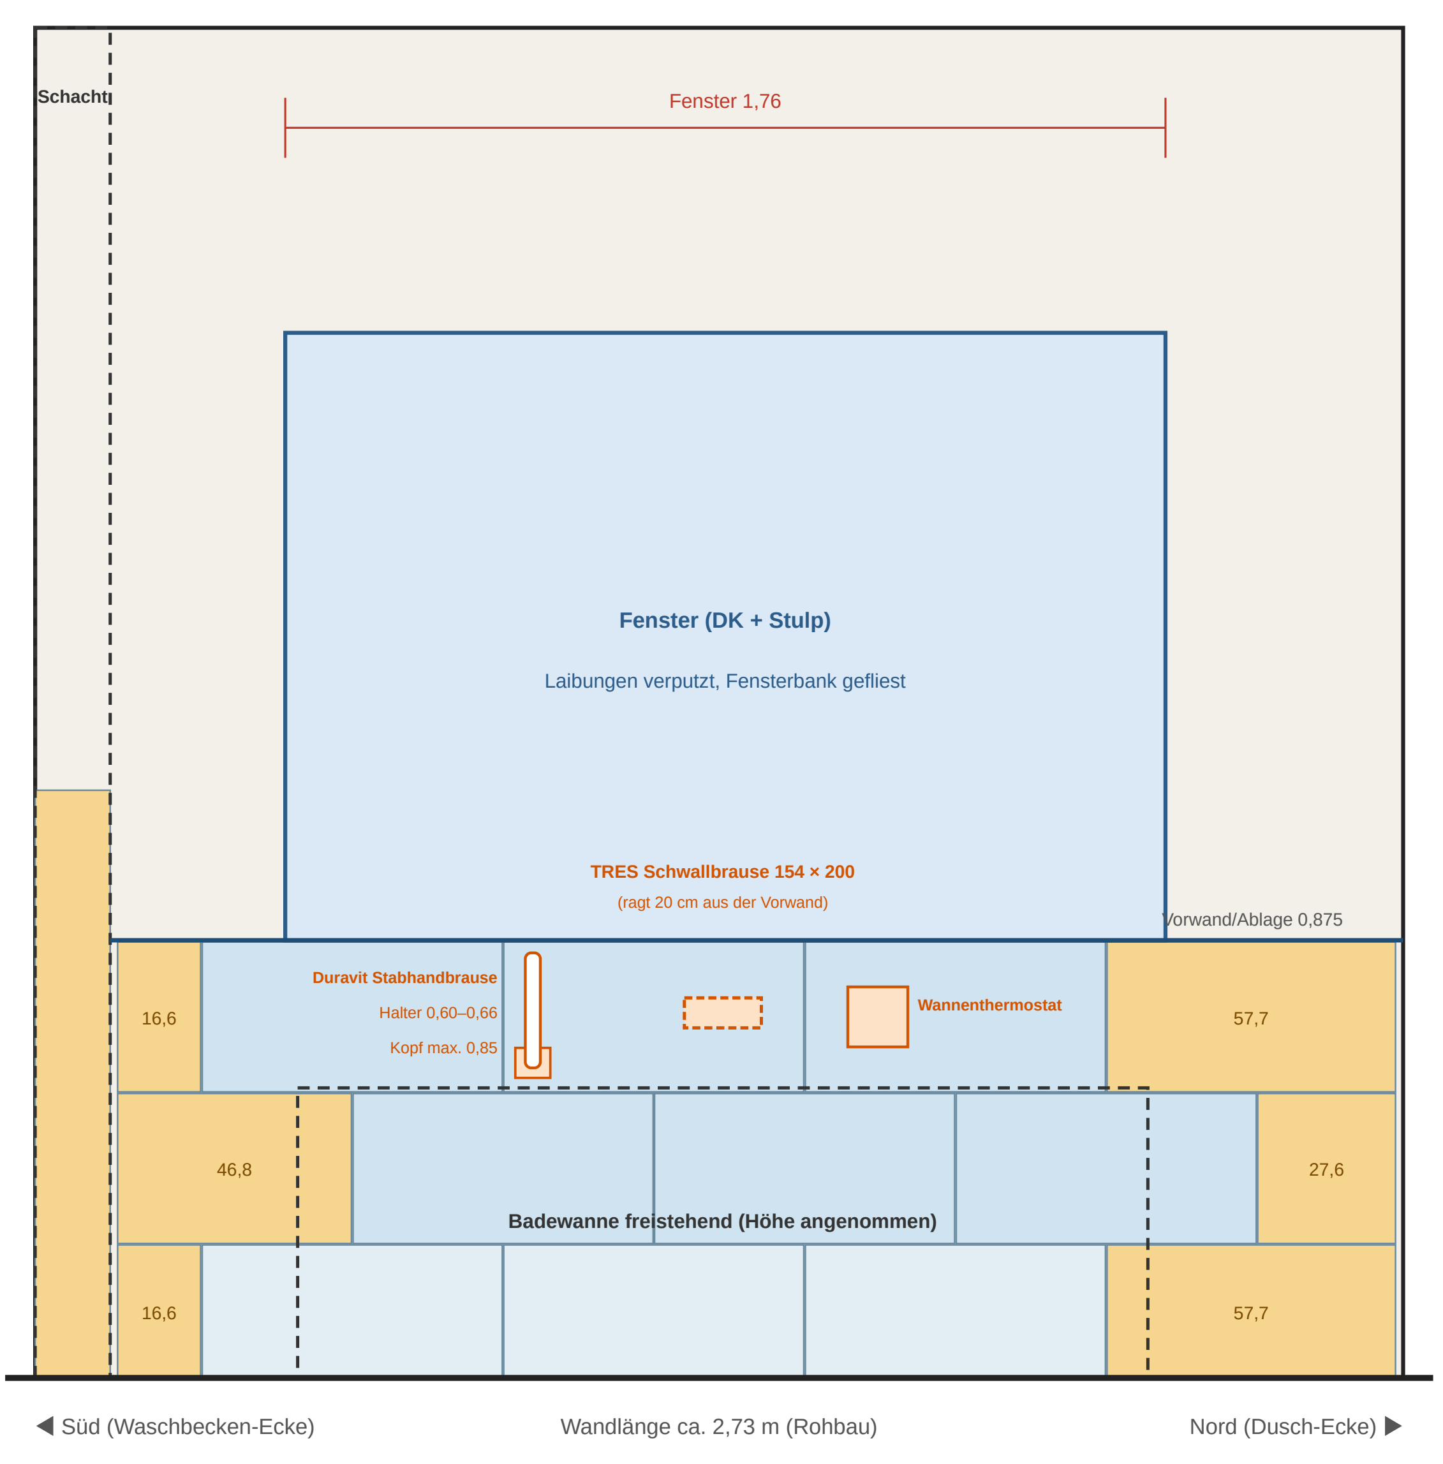
Schacht
Fenster 1,76
Fenster (DK + Stulp)
Laibungen verputzt, Fensterbank gefliest
TRES Schwallbrause 154 × 200
(ragt 20 cm aus der Vorwand)
Vorwand/Ablage 0,875
16,6
Duravit Stabhandbrause
Halter 0,60–0,66
Kopf max. 0,85
Wannenthermostat
57,7
46,8
27,6
Badewanne freistehend (Höhe angenommen)
16,6
57,7
◀ Süd (Waschbecken-Ecke)
Wandlänge ca. 2,73 m (Rohbau)
Nord (Dusch-Ecke) ▶

2 · Wand Dusche / WC (Norden)

Blick nach Norden · gefliest von der Wannen-Ecke bis zur Trennwand (2,49 m) · WC-Nische (1,00 m) nicht gefliest · Trennwand 2,35 hoch

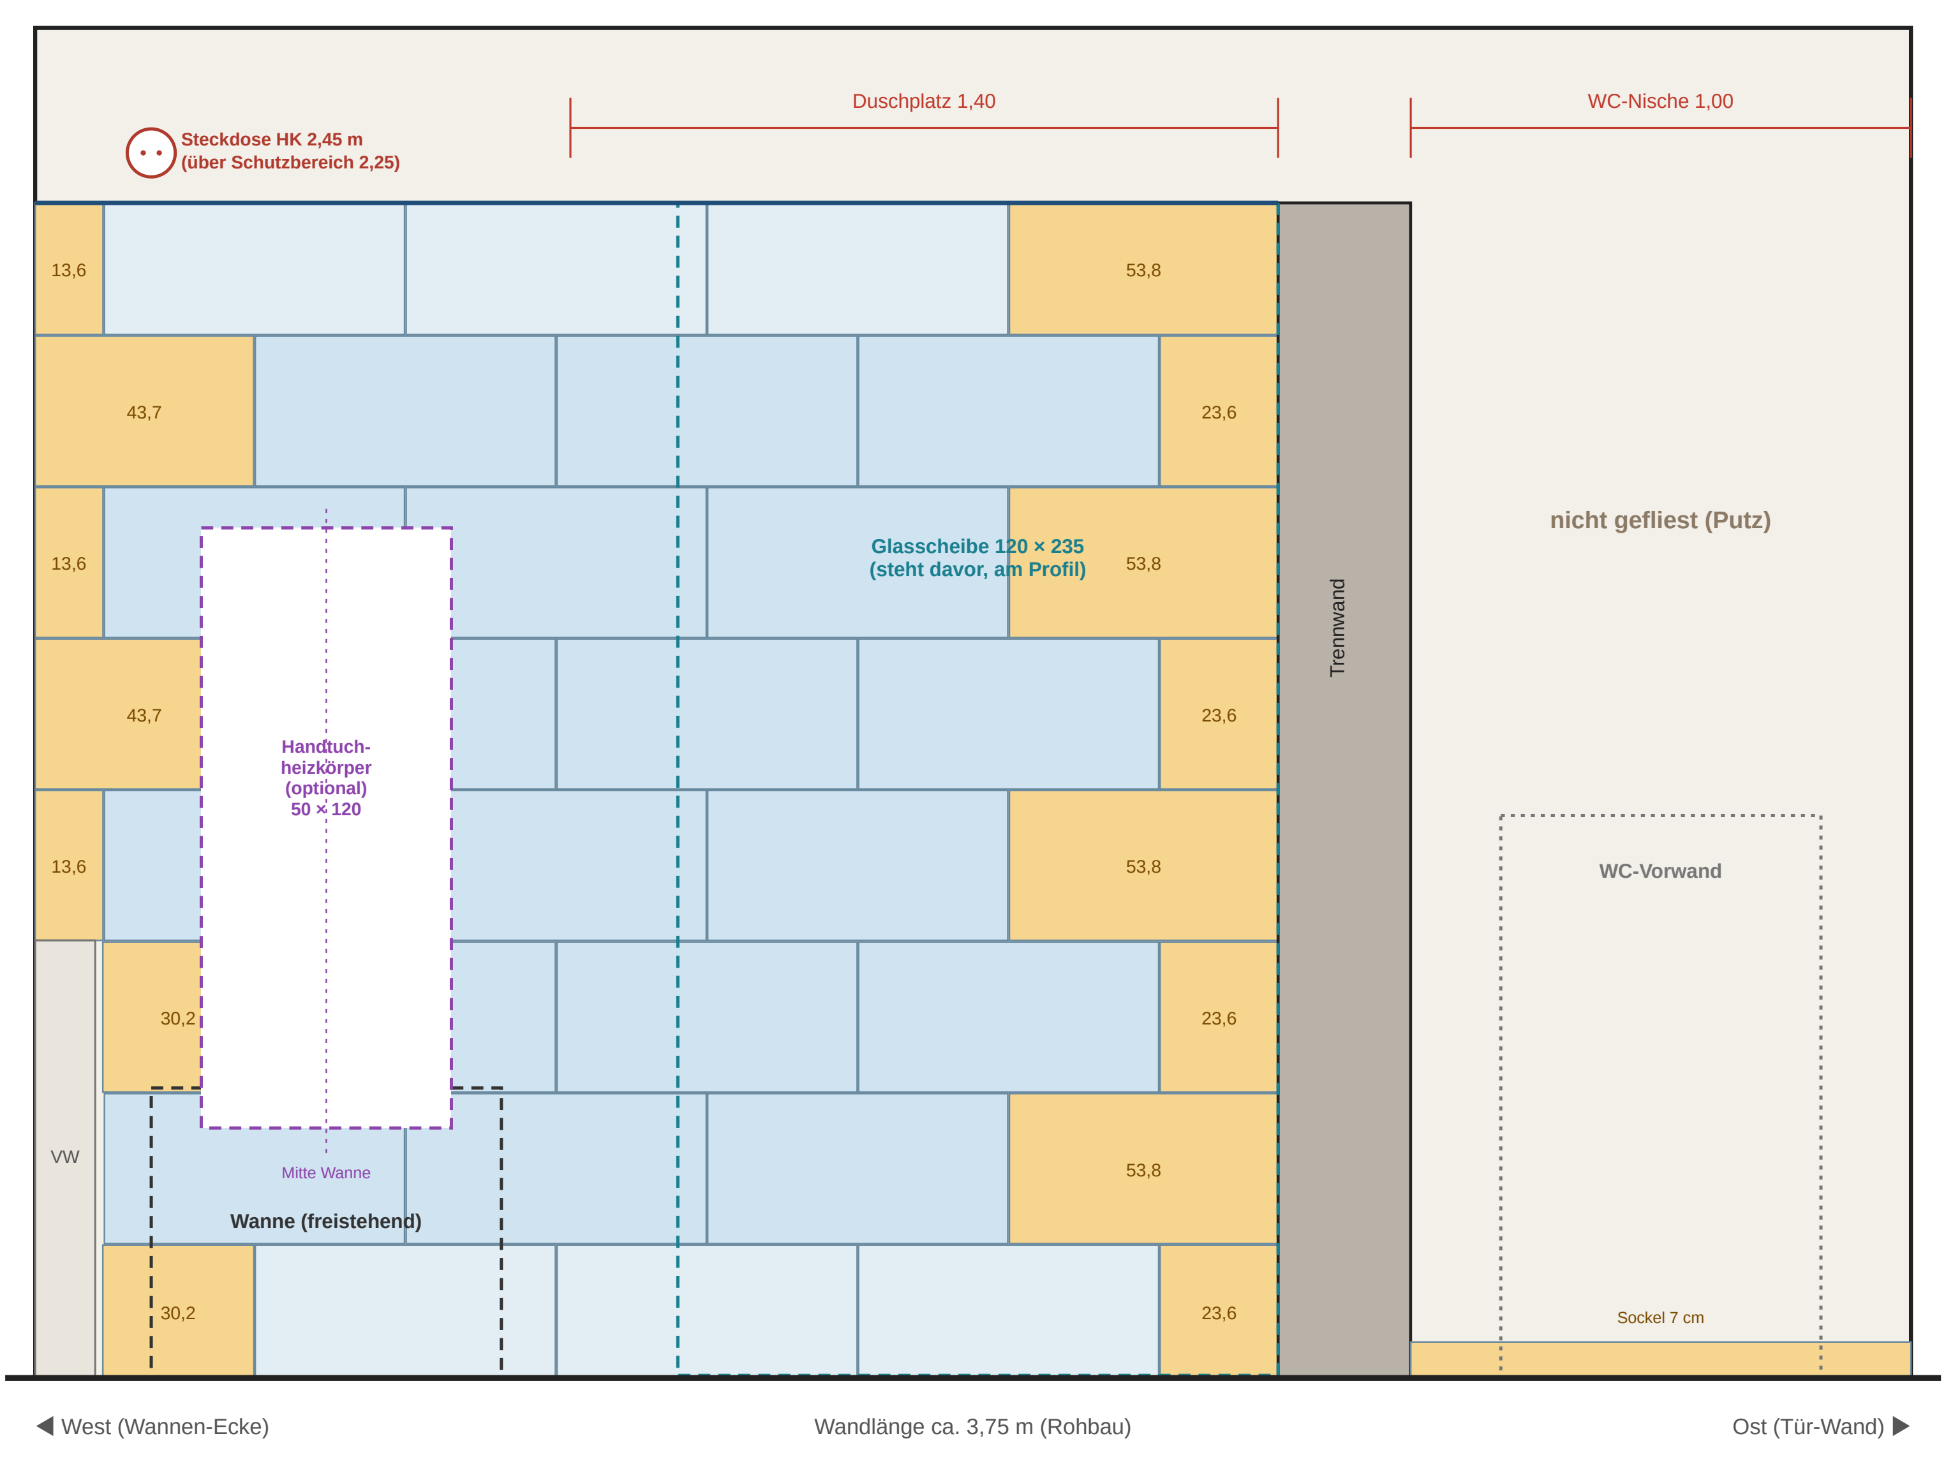
Steckdose HK 2,45 m
(über Schutzbereich 2,25)
Duschplatz 1,40
WC-Nische 1,00
13,6
53,8
43,7
23,6
nicht gefliest (Putz)
13,6
Glasscheibe 120 × 235
(steht davor, am Profil)
53,8
Trennwand
43,7
Handtuch-heizkörper (optional) 50 × 120
23,6
13,6
53,8
WC-Vorwand
30,2
23,6
VW
Mitte Wanne
Wanne (freistehend)
53,8
30,2
23,6
Sockel 7 cm
◀ West (Wannen-Ecke)
Wandlänge ca. 3,75 m (Rohbau)
Ost (Tür-Wand) ▶

3 · Trennwand – Duschseite (mit Glasprofil)

Blick nach Osten aus der Dusche · Höhe 2,35 m = Fliesenkante = Glasoberkante · Reihe A: ganze Fliese am Profil, Reihe B: ganze Fliese in der Ecke

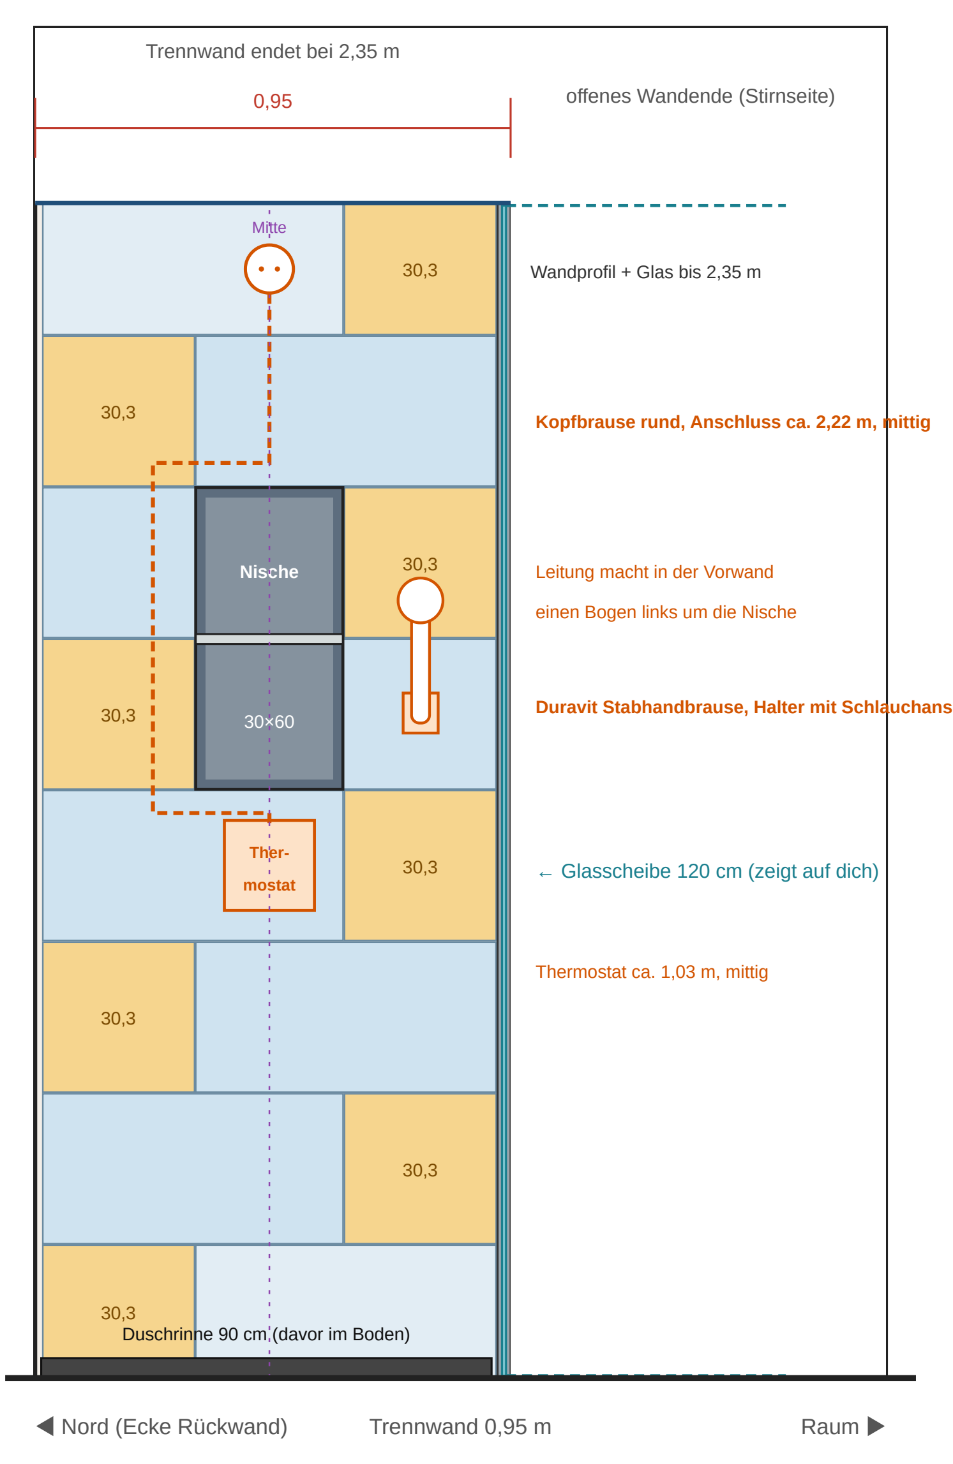
Trennwand endet bei 2,35 m
0,95
offenes Wandende (Stirnseite)
Mitte
30,3
Wandprofil + Glas bis 2,35 m
30,3
Kopfbrause rund, Anschluss ca. 2,22 m, mittig
Nische
30×60
30,3
Leitung macht in der Vorwand
einen Bogen links um die Nische
30,3
Duravit Stabhandbrause, Halter mit Schlauchanschluss ca. 1,33 m
Ther-mostat
30,3
← Glasscheibe 120 cm (zeigt auf dich)
Thermostat ca. 1,03 m, mittig
30,3
30,3
30,3
Duschrinne 90 cm (davor im Boden)
◀ Nord (Ecke Rückwand)
Trennwand 0,95 m
Raum ▶

4 · Wand Waschbecken (Süden)

Blick nach Süden · Fliesen nur auf der Vorwand (bis 1,175 m) und oben auf der Ablage, darüber Putz · die ersten 1,00 m an der Tür-Seite nur Sockel

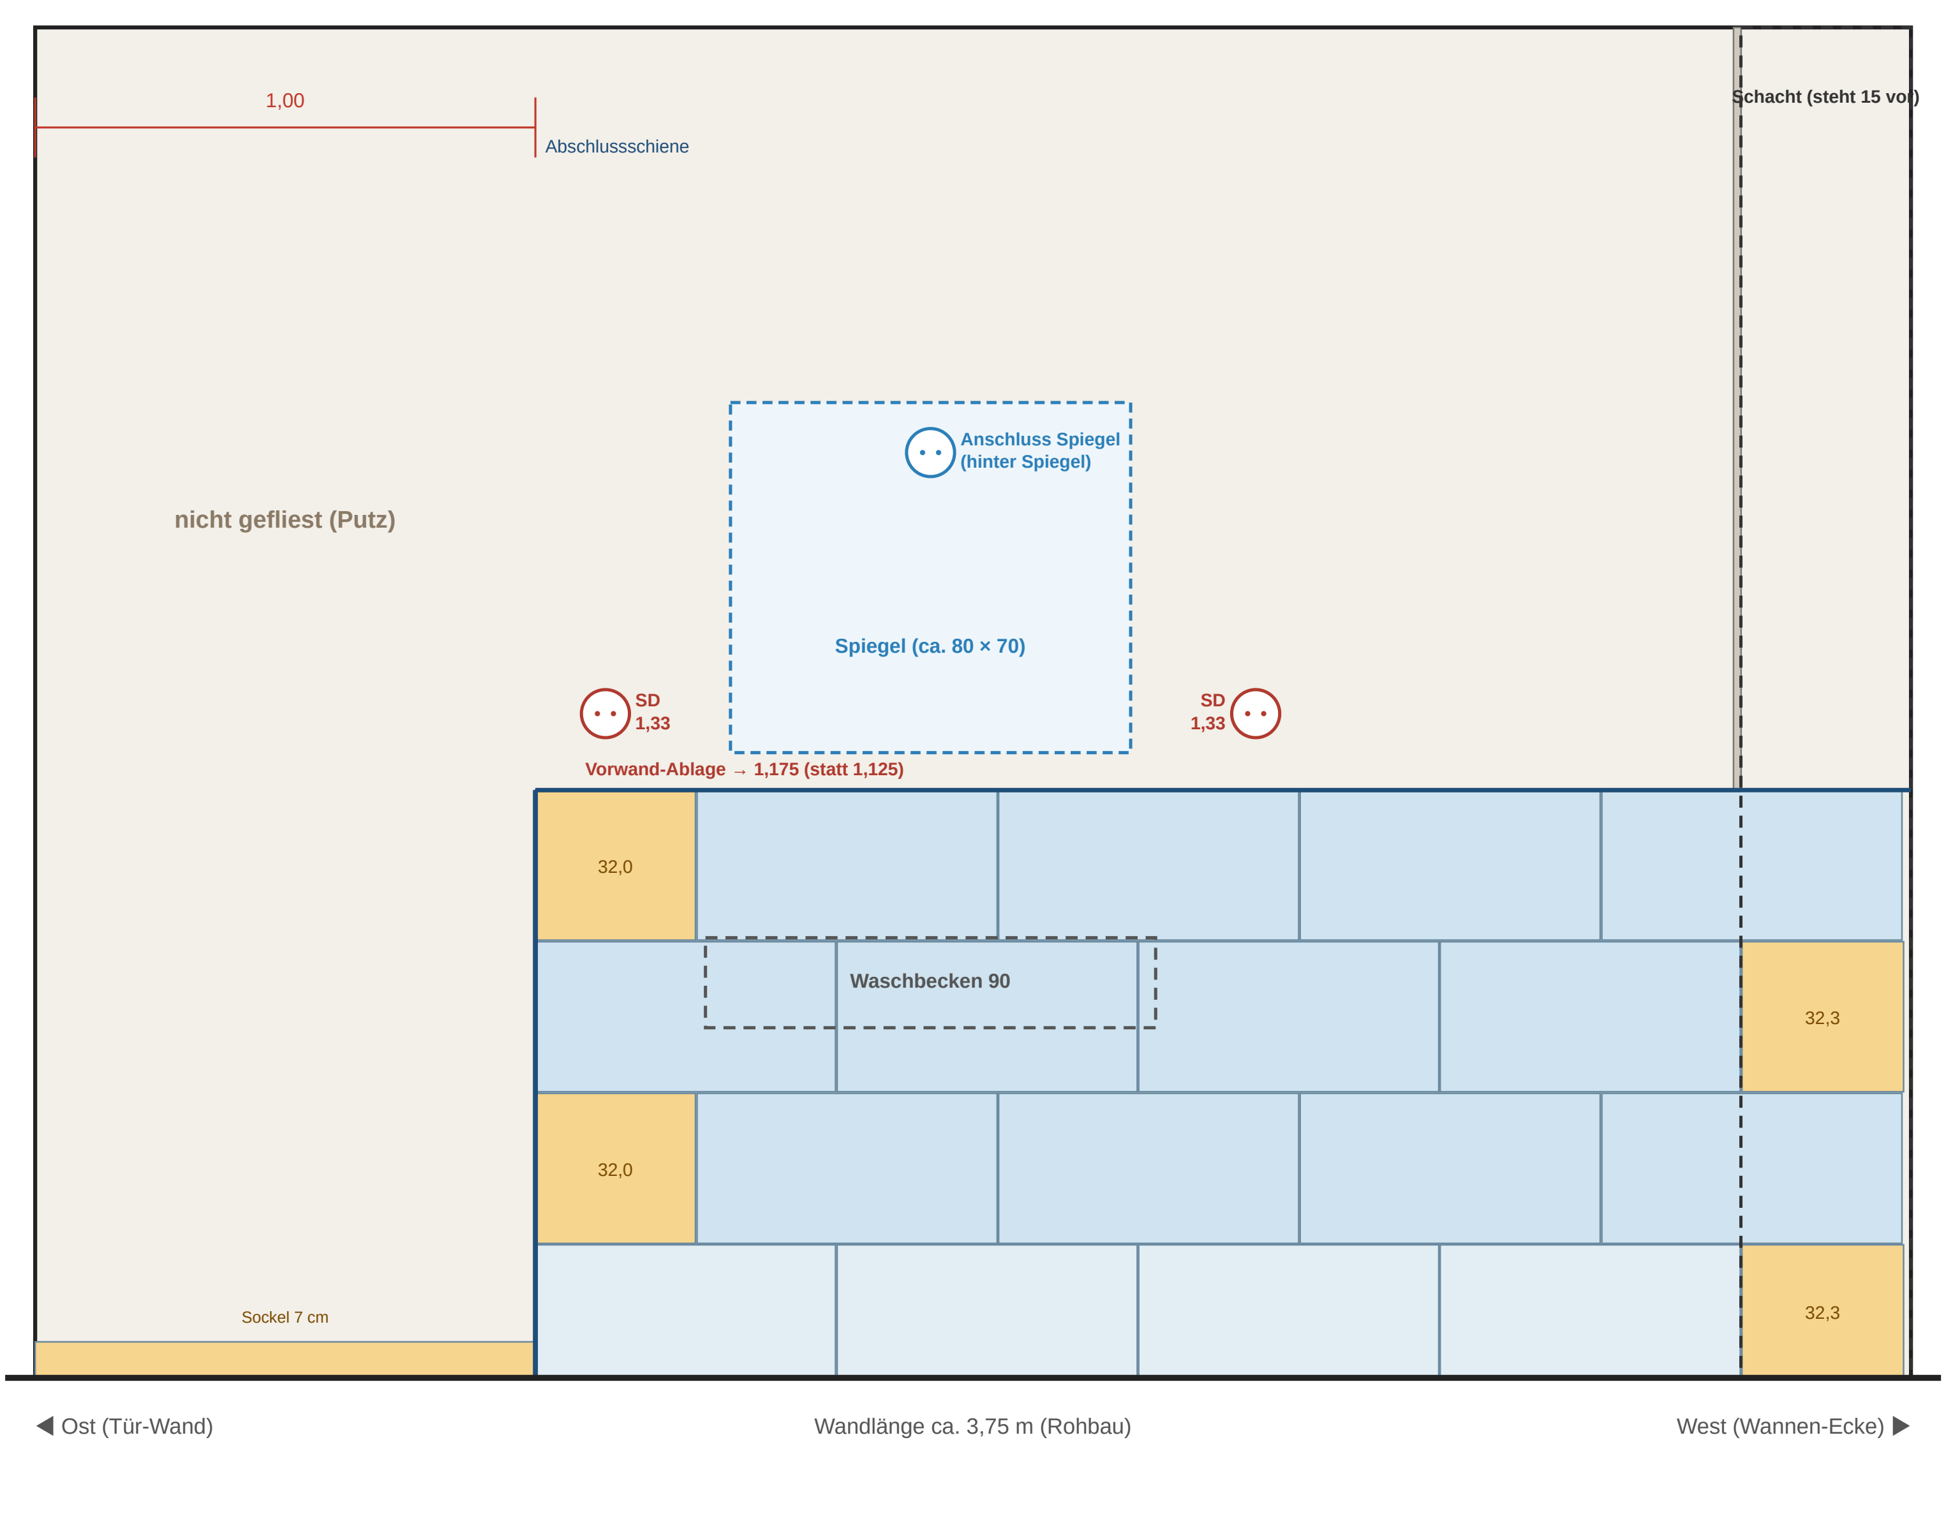
1,00
Abschlussschiene
Schacht (steht 15 vor)
nicht gefliest (Putz)
Anschluss Spiegel
(hinter Spiegel)
Spiegel (ca. 80 × 70)
SD 1,33
SD 1,33
Vorwand-Ablage → 1,175 (statt 1,125)
32,0
Waschbecken 90
32,3
32,0
Sockel 7 cm
32,3
◀ Ost (Tür-Wand)
Wandlänge ca. 3,75 m (Rohbau)
West (Wannen-Ecke) ▶

5 · Wand mit Tür (Osten)

Blick nach Osten · nicht gefliest, nur Fliesensockel 7 cm

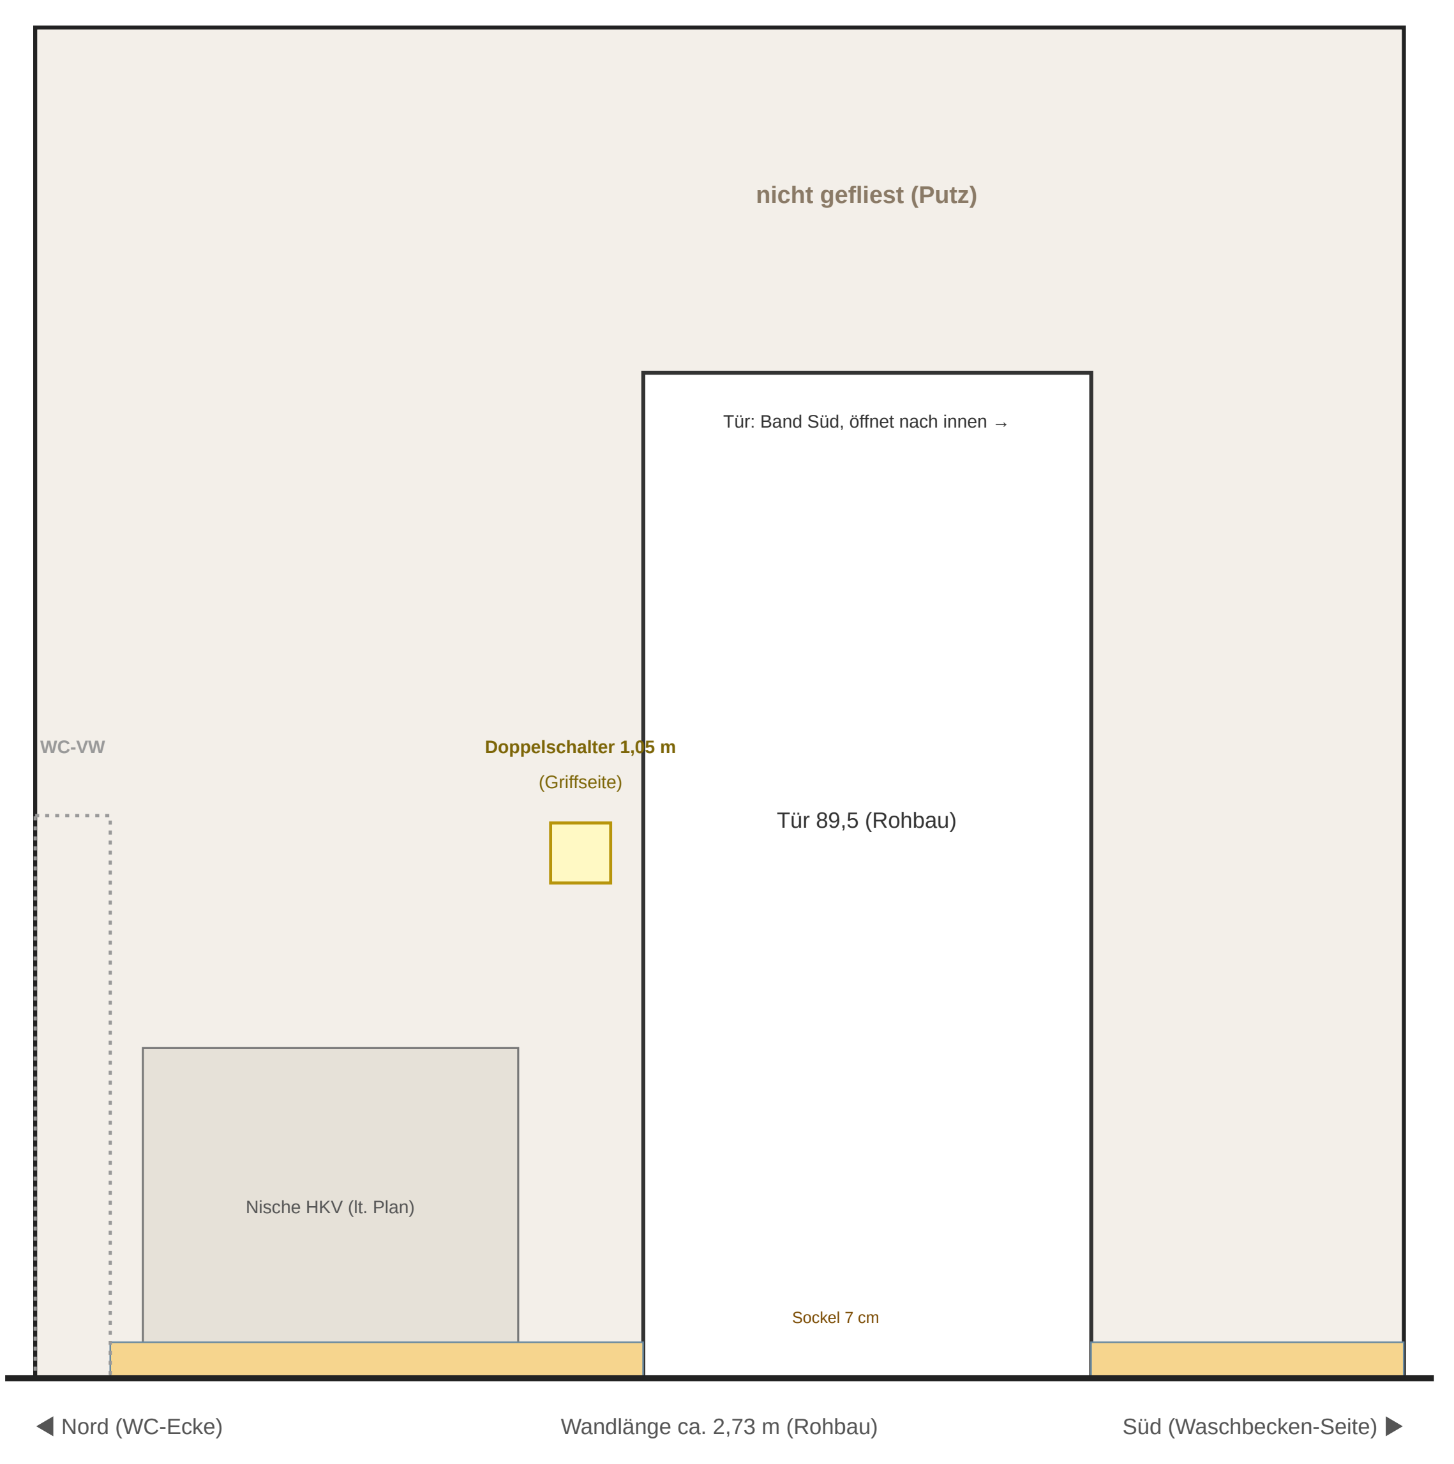
nicht gefliest (Putz)
Tür: Band Süd, öffnet nach innen →
WC-VW
Doppelschalter 1,05 m
(Griffseite)
Tür 89,5 (Rohbau)
Nische HKV (lt. Plan)
Sockel 7 cm
◀ Nord (WC-Ecke)
Wandlänge ca. 2,73 m (Rohbau)
Süd (Waschbecken-Seite) ▶

🟦 ganze Fliese 60×30
▭ volle Breite, in der Höhe geschnitten
🟨 Zuschnitt (Zahl = Maß in cm)
— Fliesenkante 2,35 m

Fugen 3 mm · Reihenhöhen von unten: 26,6 / 6× 30 / 26,3 cm → Fuge genau auf Fensterbank (0,875) · Maße aus Plan „03A Dachgeschoss“, auf der Baustelle nachmessen! Decke/Dachschräge vereinfacht als 2,70 m dargestellt. Ansichten jeweils „vom Raum aus auf die Wand geschaut“. Badewanne gedreht: linke Längsseite parallel zur Wand.

▨ ganze Bodenfliese