Bad DG – Fliesenplan Wände + Boden (Fliesen 60×30, 30 cm versetzt)

0 · Draufsicht Bad (Grundriss)

Norden oben · blau = gefliest bis 2,35 m · orange = Fliesensockel 7 cm · SD = Steckdose · Maße Rohbau lt. Plan

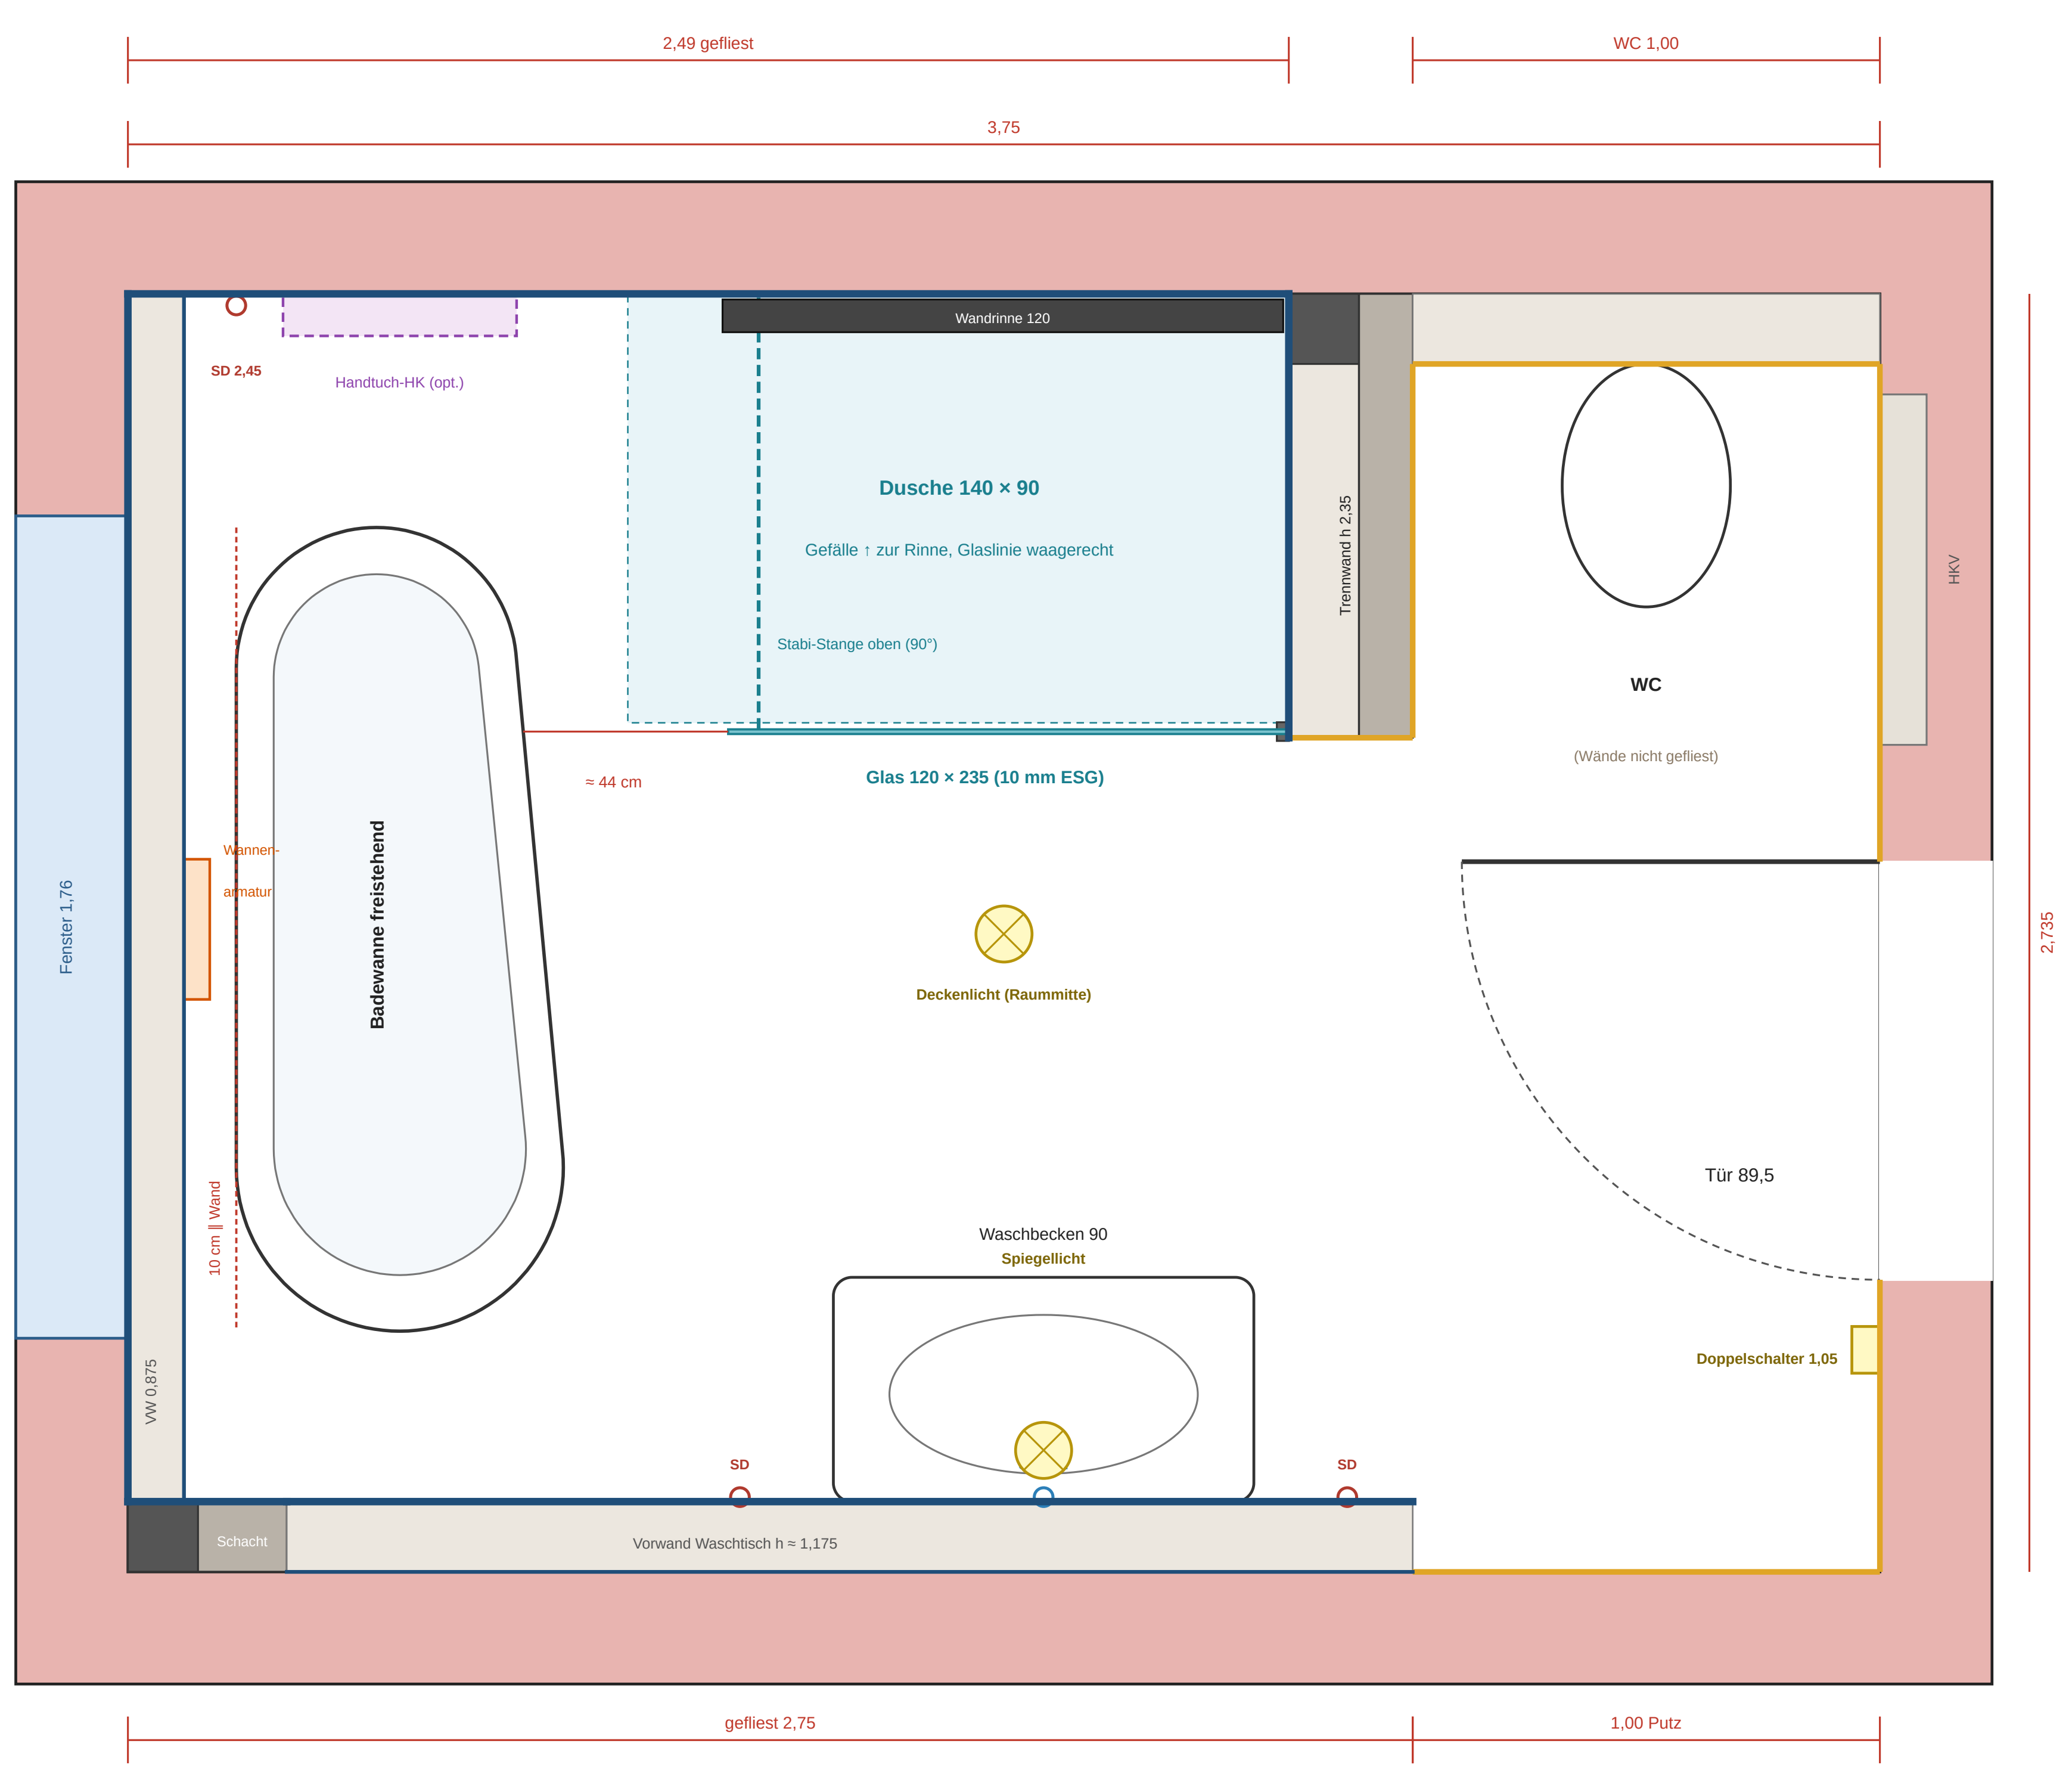
2,49 gefliest
WC 1,00
3,75
Wandrinne 120
SD 2,45
Handtuch-HK (opt.)
Dusche 140 × 90
Gefälle ↑ zur Rinne, Glaslinie waagerecht
Stabi-Stange oben (90°)
Glas 120 × 235 (10 mm ESG)
Trennwand h 2,35
WC
(Wände nicht gefliest)
HKV
2,735
Fenster 1,76
Wannen-
armatur
Badewanne freistehend
≈ 44 cm
10 cm ‖ Wand
Deckenlicht (Raummitte)
Tür 89,5
Waschbecken 90
Spiegellicht
Doppelschalter 1,05
VW 0,875
SD
SD
Schacht
Vorwand Waschtisch h ≈ 1,175
gefliest 2,75
1,00 Putz

0a · Boden – Fliesen längs (Ost–West), 30 cm versetzt

60×30 · ca. 9,0 m² · ganze Reihen an der Duschwand · Streifen 13,7 cm unter der Waschtisch-Vorwand · Wandrinne 120 cm an der Rückwand, Gefälle nur in der Dusche (endet vor dem Glas)

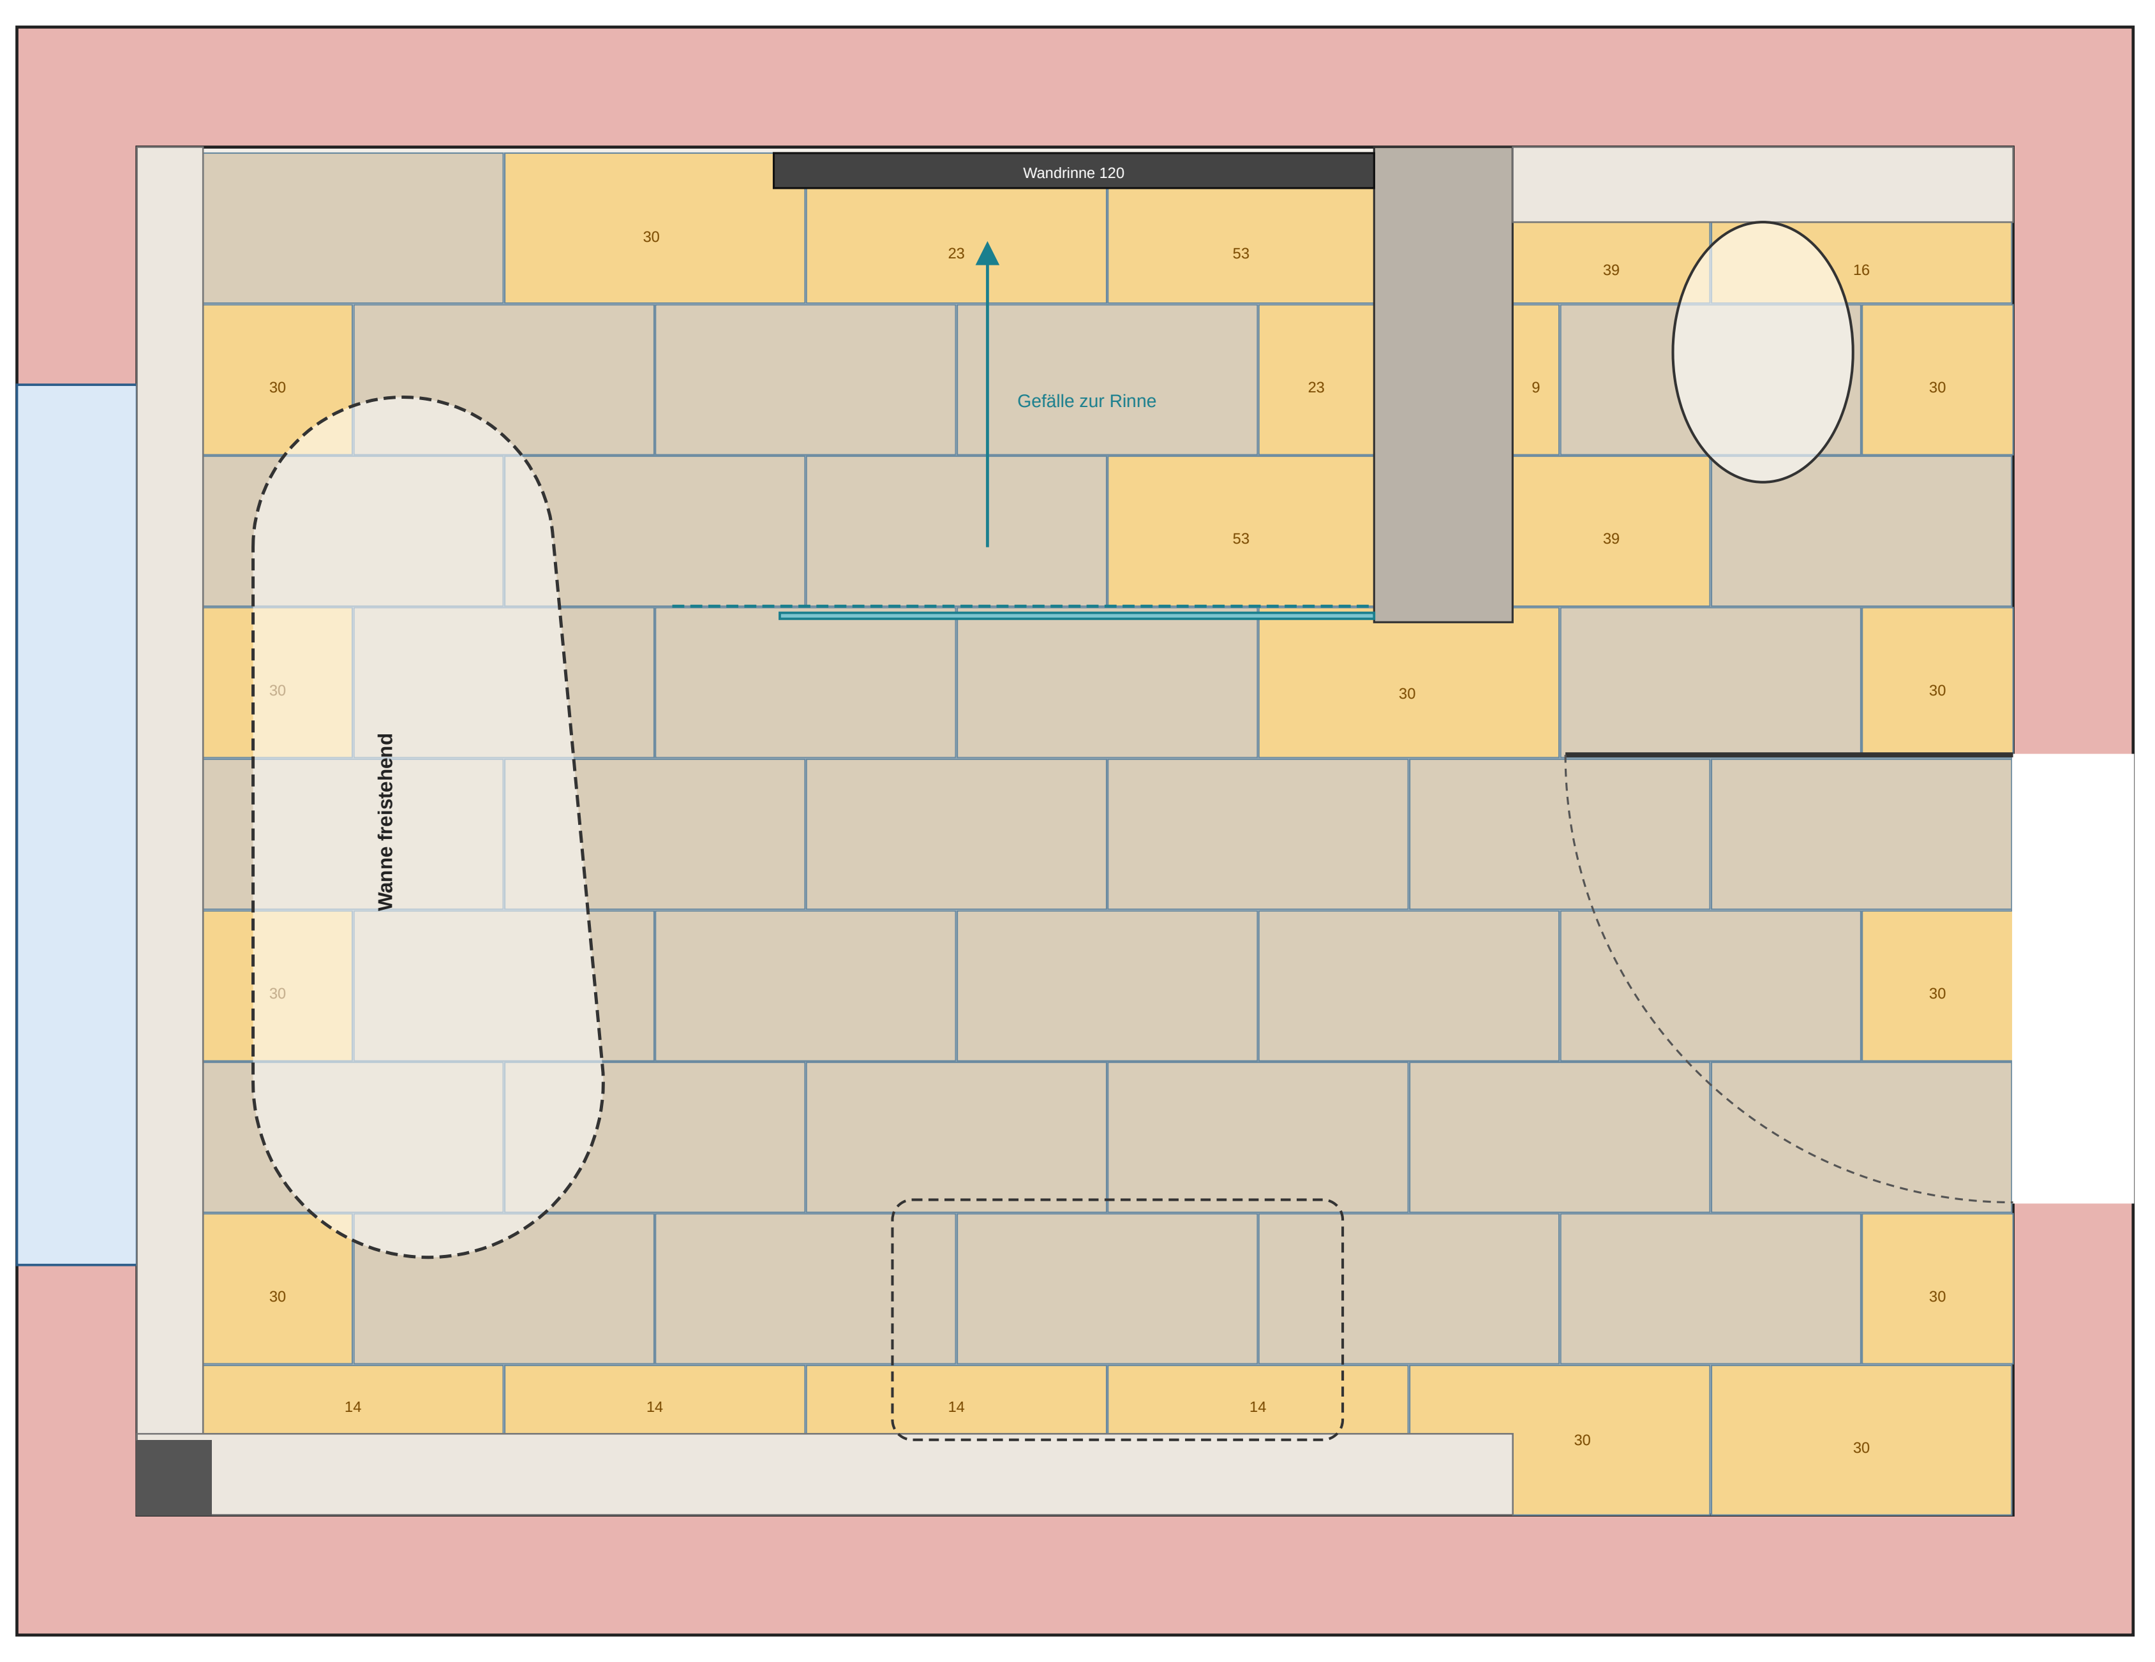
Wandrinne 120
30
23
53
39
16
30
Gefälle zur Rinne
23
9
30
53
39
30
Wanne freistehend
30
30
30
30
30
30
14
14
14
14
30
30

1 · Wand Badewanne / Fenster (Westen)

Blick nach Westen · komplett gefliest bis 2,35 m · Fenster: Brüstung ca. 0,875 / Sturz ca. 2,09 ab FFB (lt. Plan)

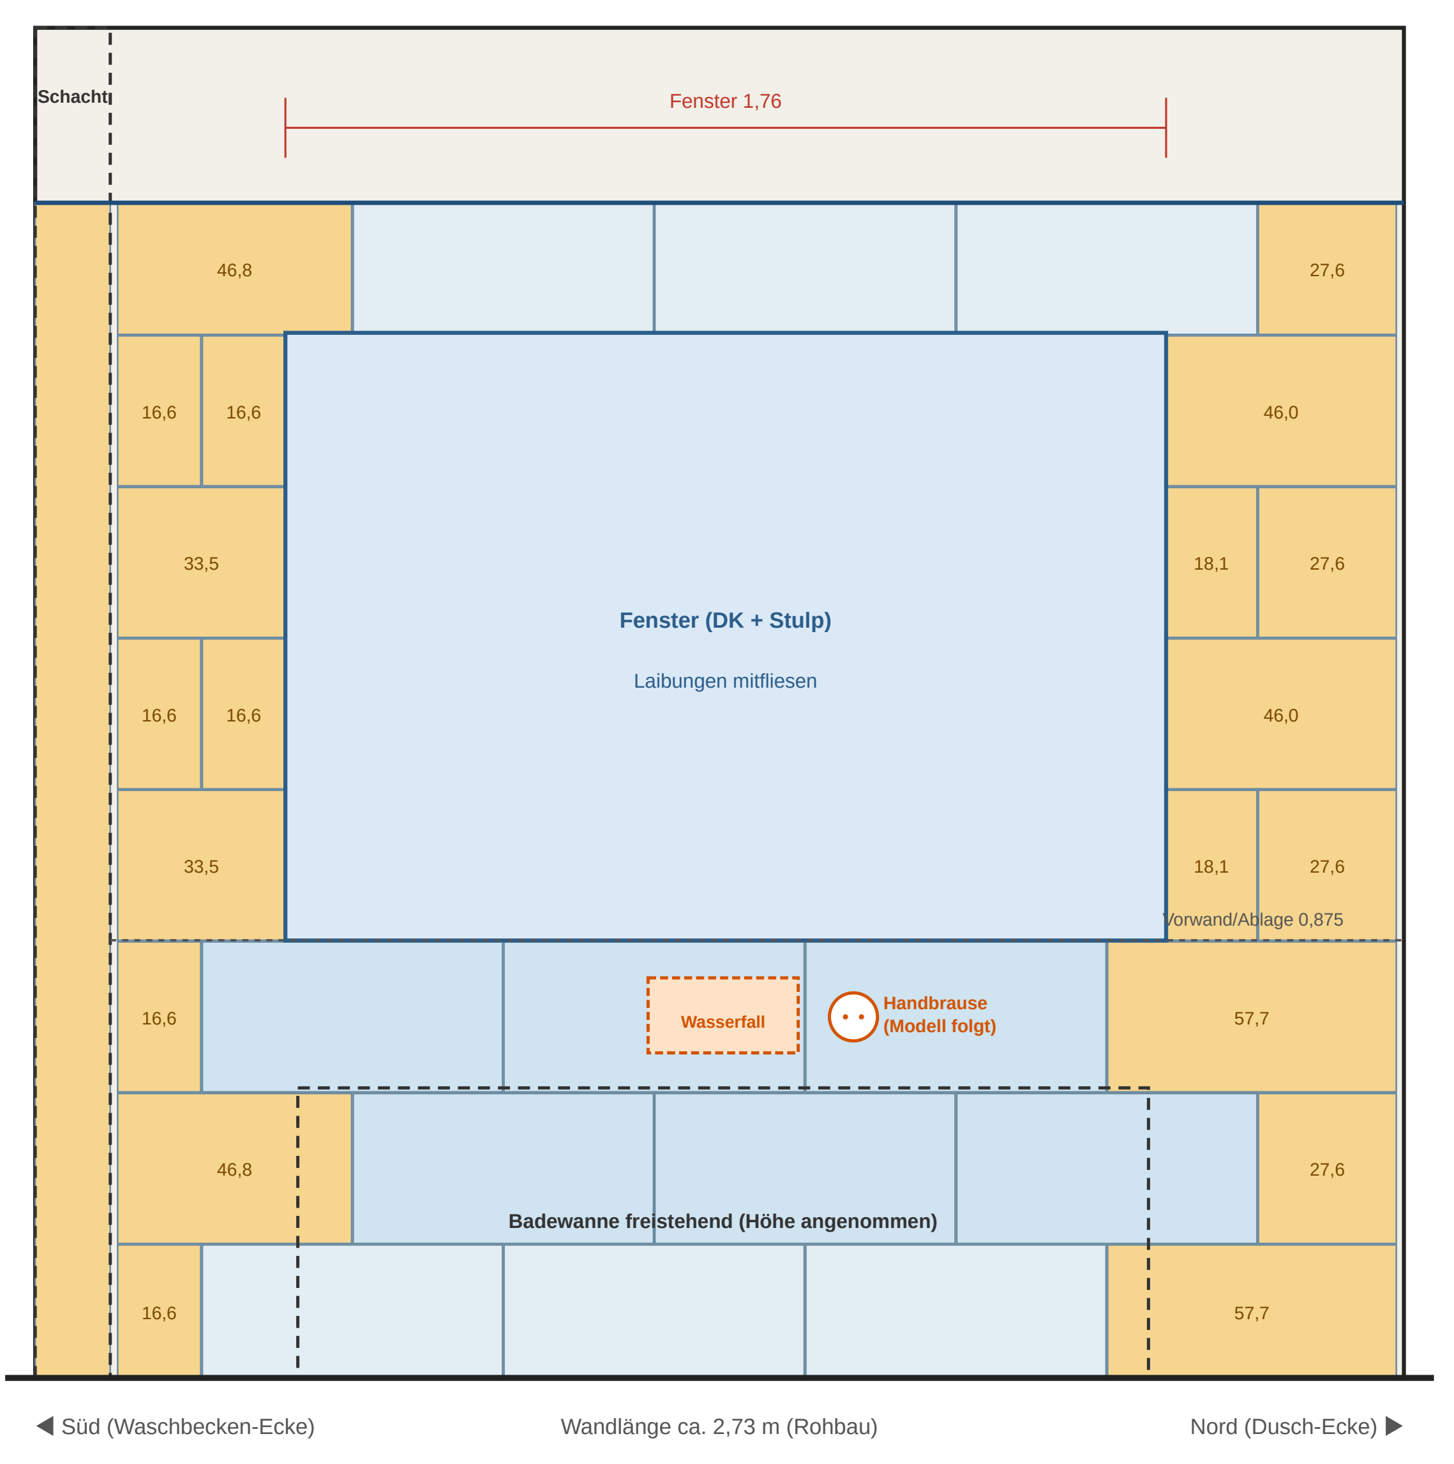
Schacht
Fenster 1,76
46,8
27,6
16,6
16,6
46,0
33,5
Fenster (DK + Stulp)
Laibungen mitfliesen
18,1
27,6
16,6
16,6
46,0
33,5
18,1
27,6
Vorwand/Ablage 0,875
16,6
Wasserfall
Handbrause (Modell folgt)
57,7
46,8
27,6
Badewanne freistehend (Höhe angenommen)
16,6
57,7
◀ Süd (Waschbecken-Ecke)
Wandlänge ca. 2,73 m (Rohbau)
Nord (Dusch-Ecke) ▶

2 · Wand Dusche / WC (Norden)

Blick nach Norden · gefliest von der Wannen-Ecke bis zur Trennwand (2,49 m) · WC-Nische (1,00 m) nicht gefliest · Trennwand 2,35 hoch

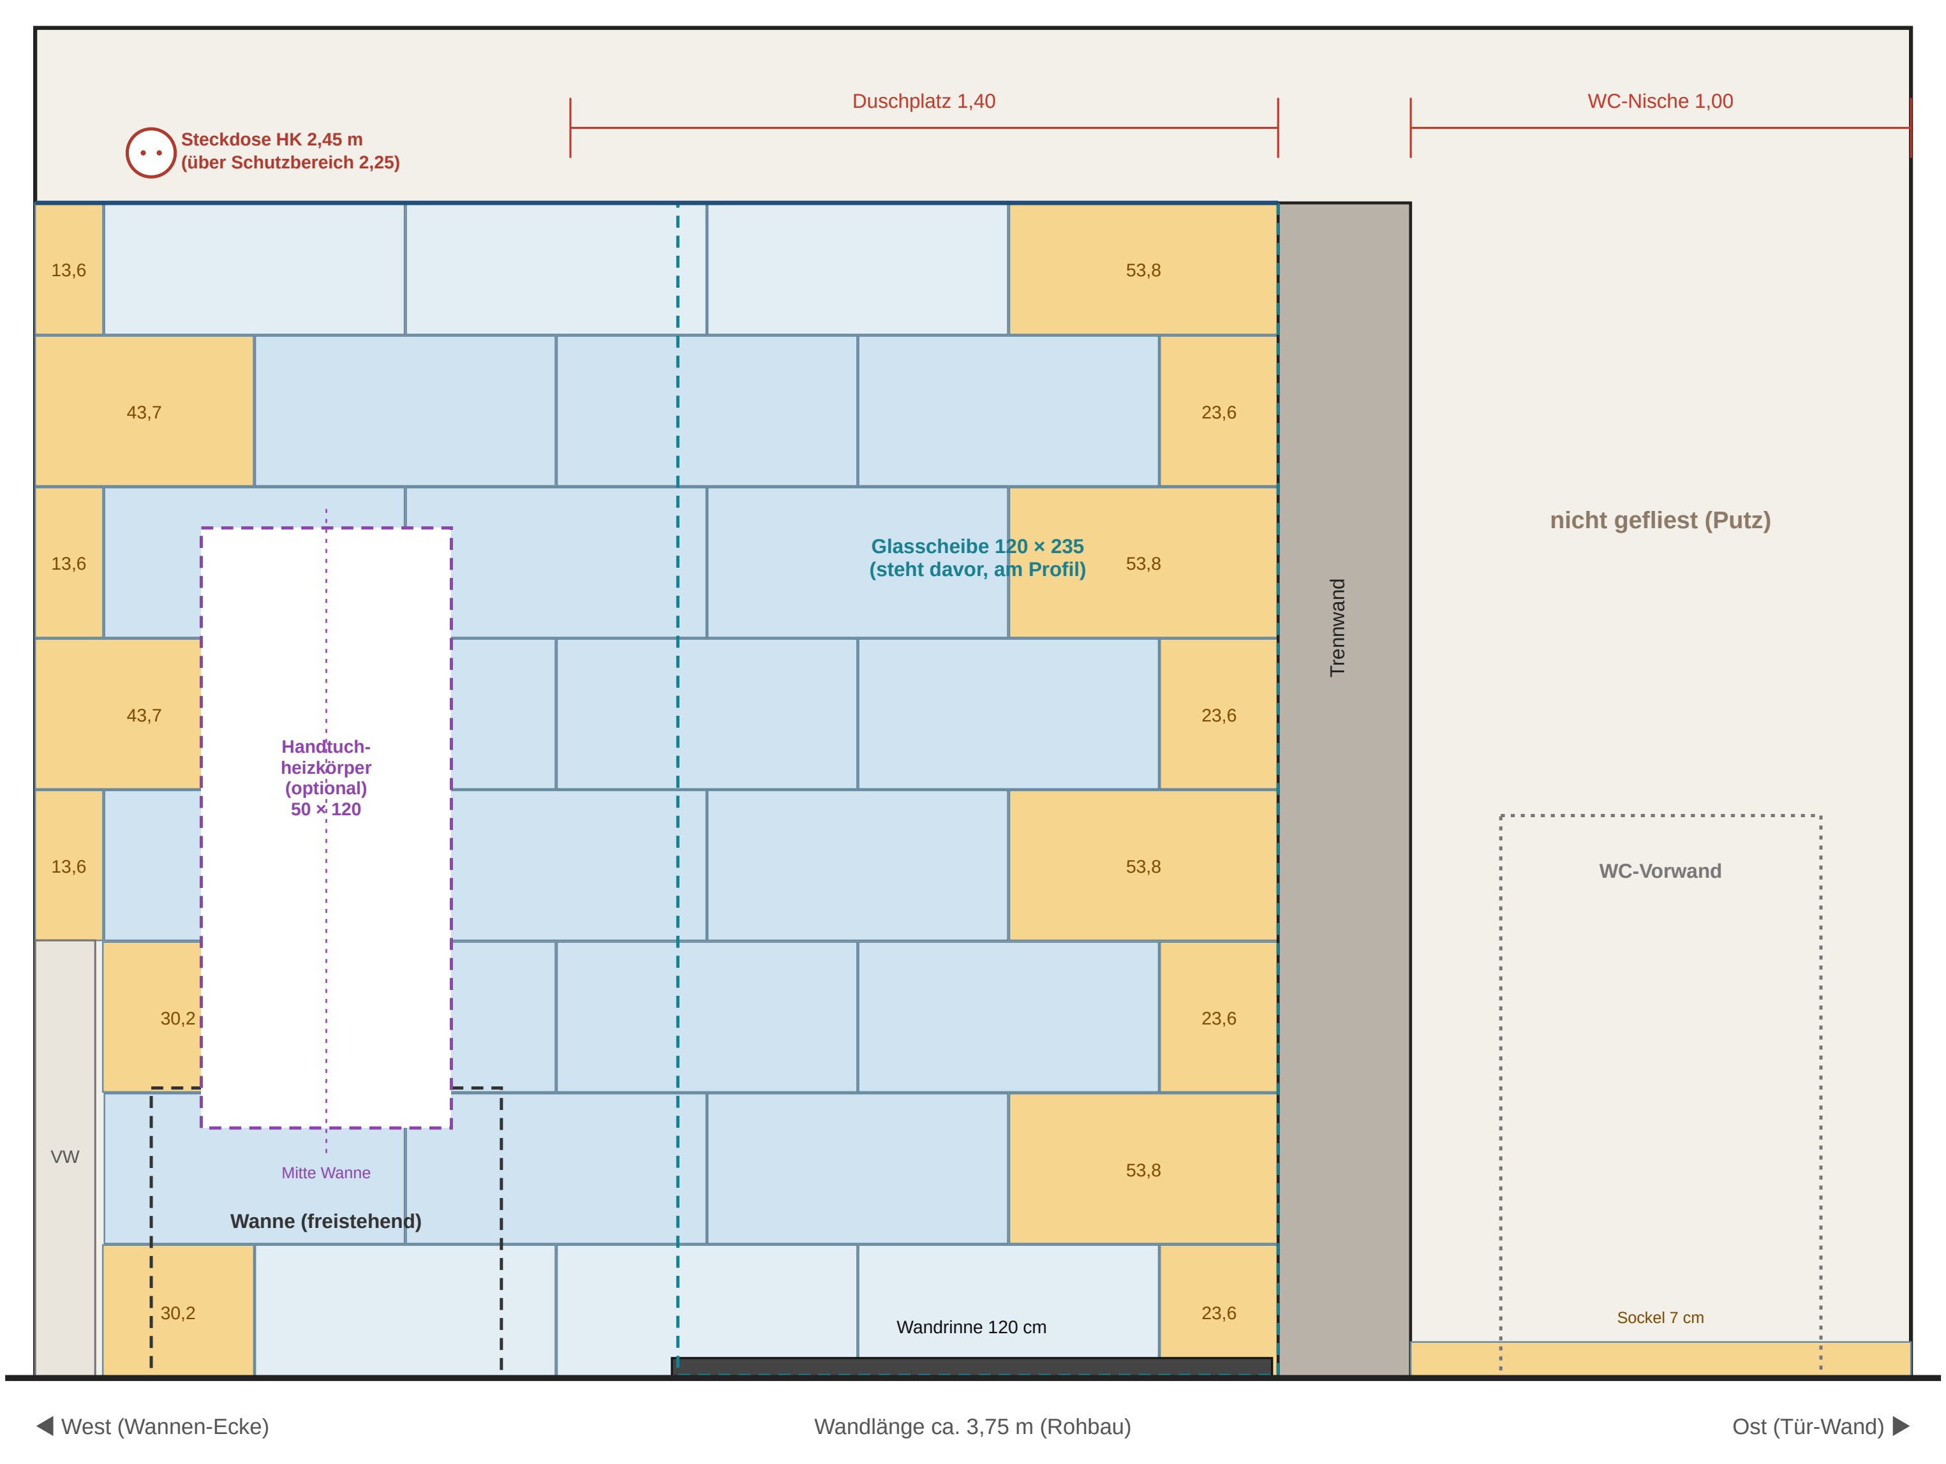
Steckdose HK 2,45 m (über Schutzbereich 2,25)
Duschplatz 1,40
WC-Nische 1,00
13,6
53,8
43,7
23,6
13,6
Glasscheibe 120 × 235 (steht davor, am Profil)
53,8
nicht gefliest (Putz)
43,7
Handtuch-heizkörper (optional) 50 × 120
23,6
Trennwand
13,6
53,8
WC-Vorwand
30,2
23,6
VW
Mitte Wanne
Wanne (freistehend)
53,8
30,2
Wandrinne 120 cm
23,6
Sockel 7 cm
◀ West (Wannen-Ecke)
Wandlänge ca. 3,75 m (Rohbau)
Ost (Tür-Wand) ▶

3 · Trennwand – Duschseite (mit Glasprofil)

Blick nach Osten aus der Dusche · Höhe 2,35 m = Fliesenkante = Glasoberkante · Reihe A: ganze Fliese am Profil, Reihe B: ganze Fliese in der Ecke

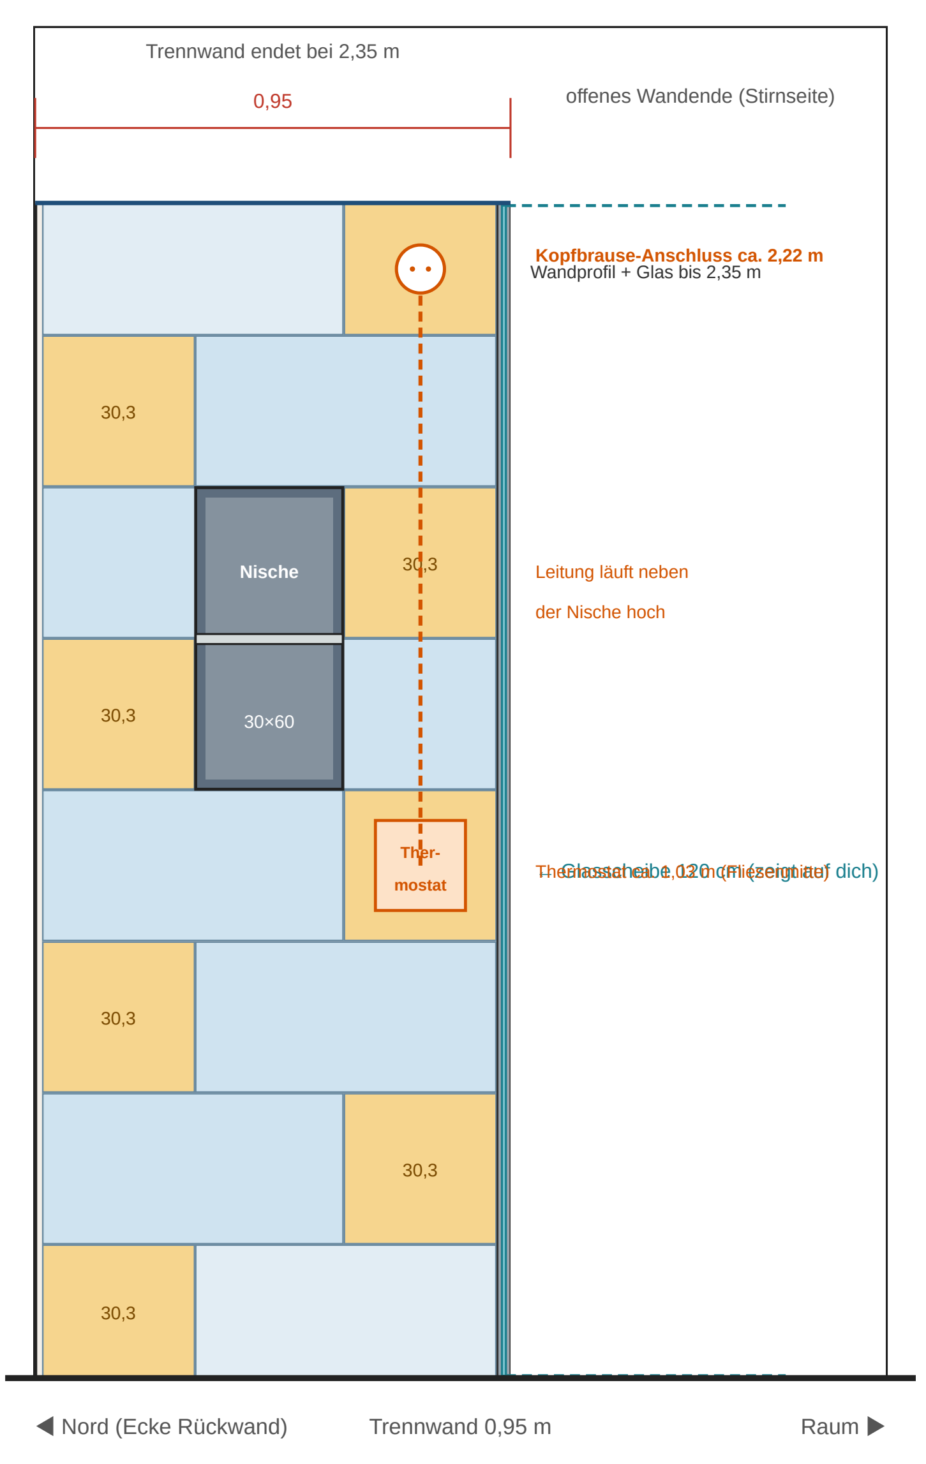
Trennwand endet bei 2,35 m
0,95
offenes Wandende (Stirnseite)
Kopfbrause-Anschluss ca. 2,22 m
Wandprofil + Glas bis 2,35 m
30,3
Nische
30×60
30,3
Leitung läuft neben
der Nische hoch
30,3
Ther-
mostat
Glasscheibe 120 cm (zeigt auf dich)
30,3
30,3
30,3
◀ Nord (Ecke Rückwand)
Trennwand 0,95 m
Raum ▶

4 · Wand Waschbecken (Süden)

Blick nach Süden · gefliest von der Wannen-Ecke bis 2,75 m (Ende Vorwand) · die ersten 1,00 m an der Tür-Seite nicht gefliest

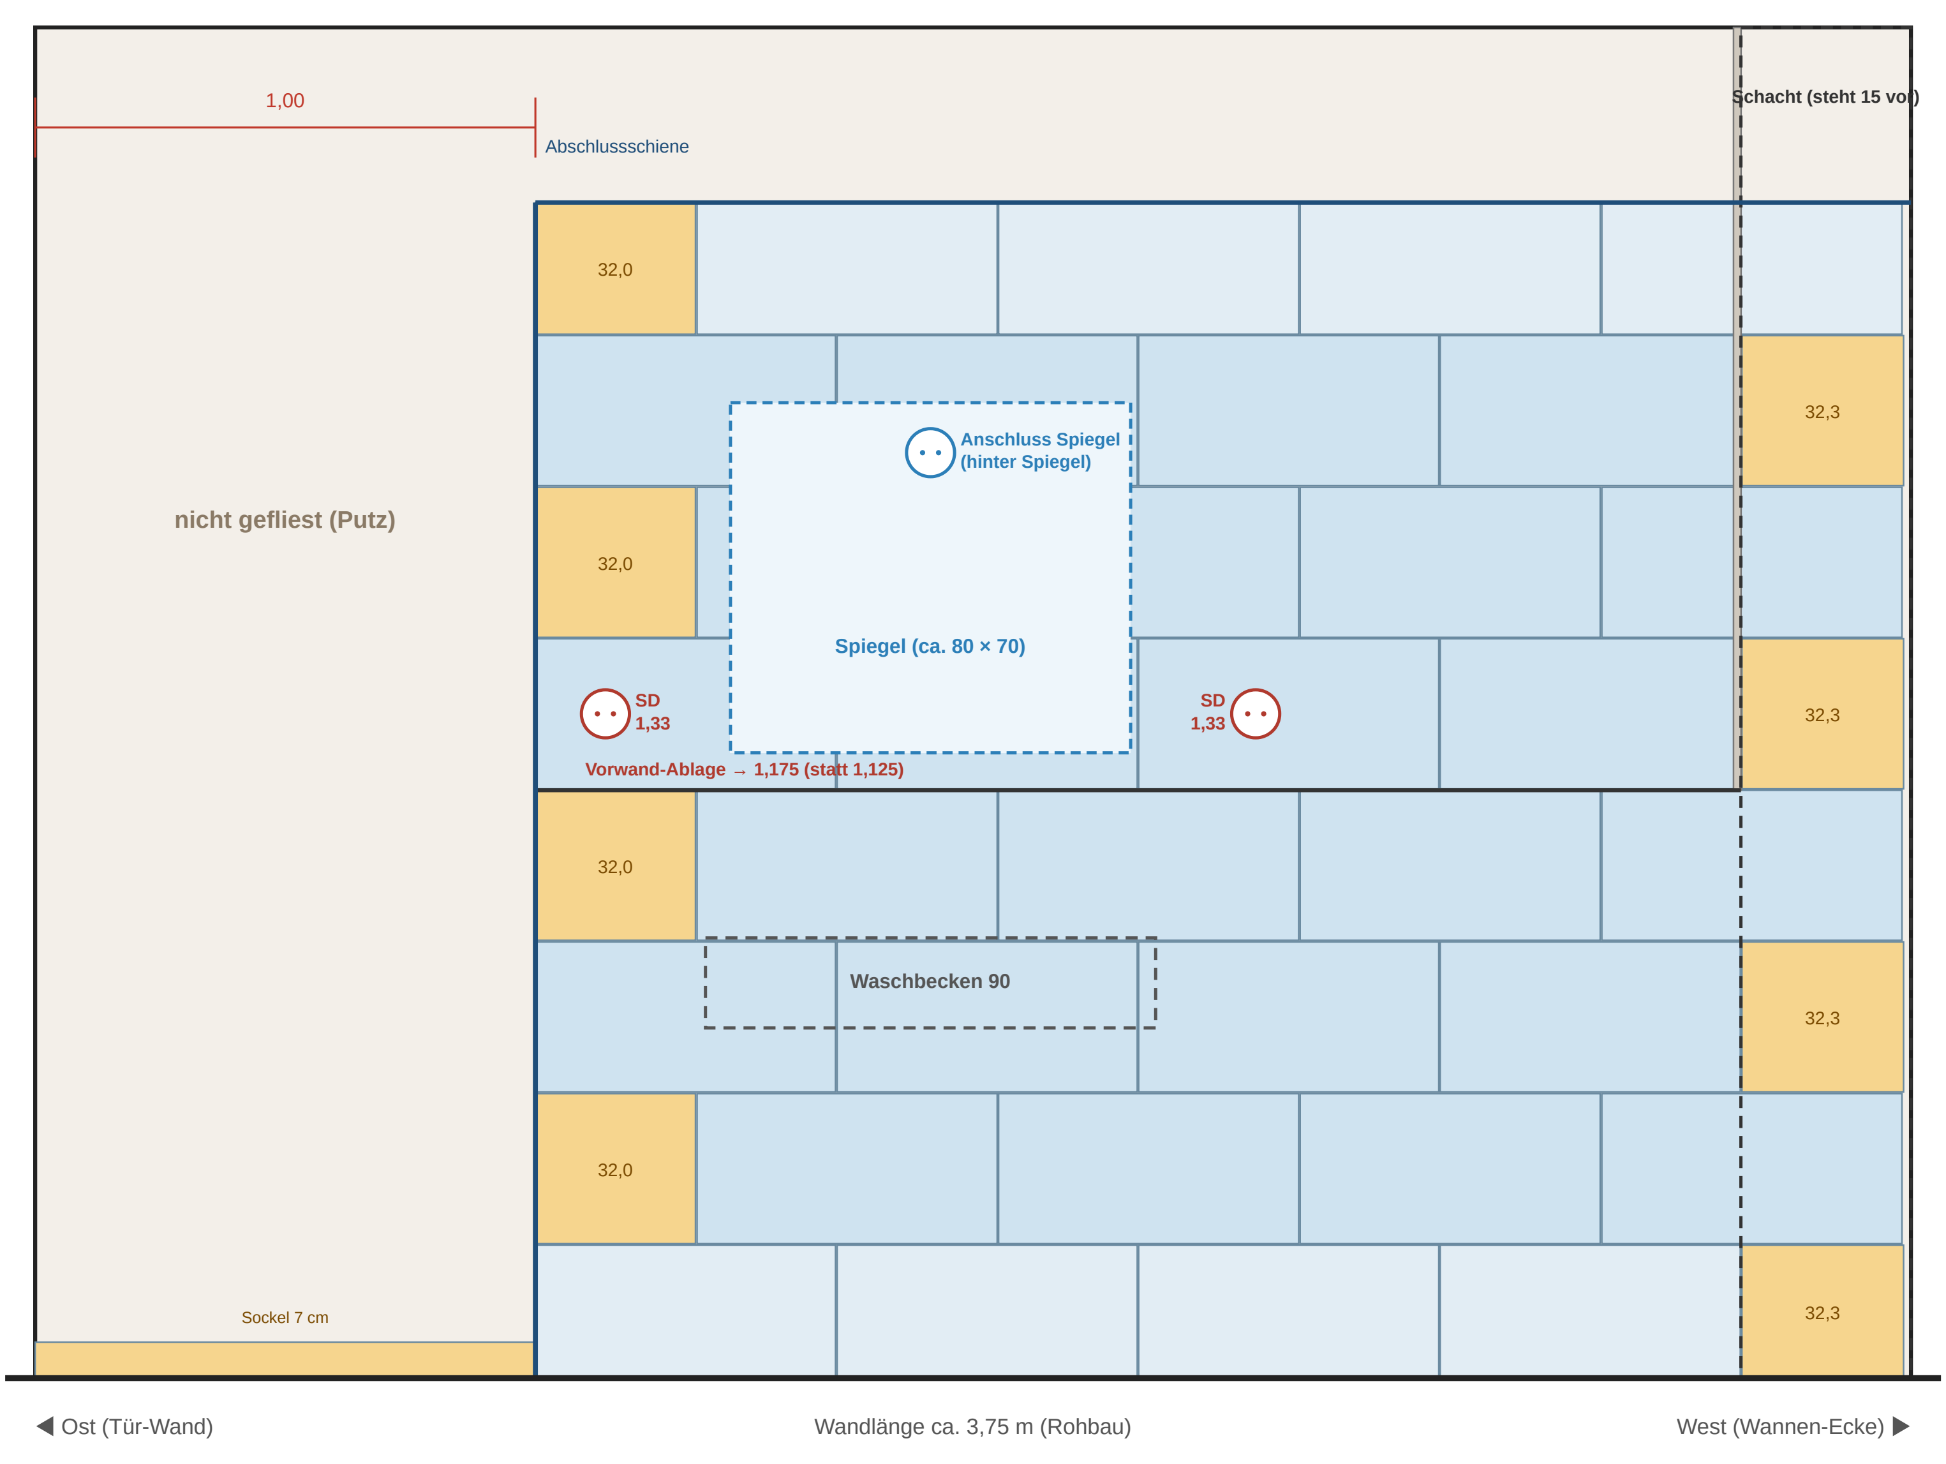
1,00
Abschlussschiene
Schacht (steht 15 vor)
32,0
32,3
Anschluss Spiegel (hinter Spiegel)
nicht gefliest (Putz)
32,0
Spiegel (ca. 80 × 70)
SD 1,33
SD 1,33
32,3
Vorwand-Ablage → 1,175 (statt 1,125)
32,0
Waschbecken 90
32,3
32,0
Sockel 7 cm
32,3
◀ Ost (Tür-Wand)
Wandlänge ca. 3,75 m (Rohbau)
West (Wannen-Ecke) ▶

5 · Wand mit Tür (Osten)

Blick nach Osten · nicht gefliest, nur Fliesensockel 7 cm

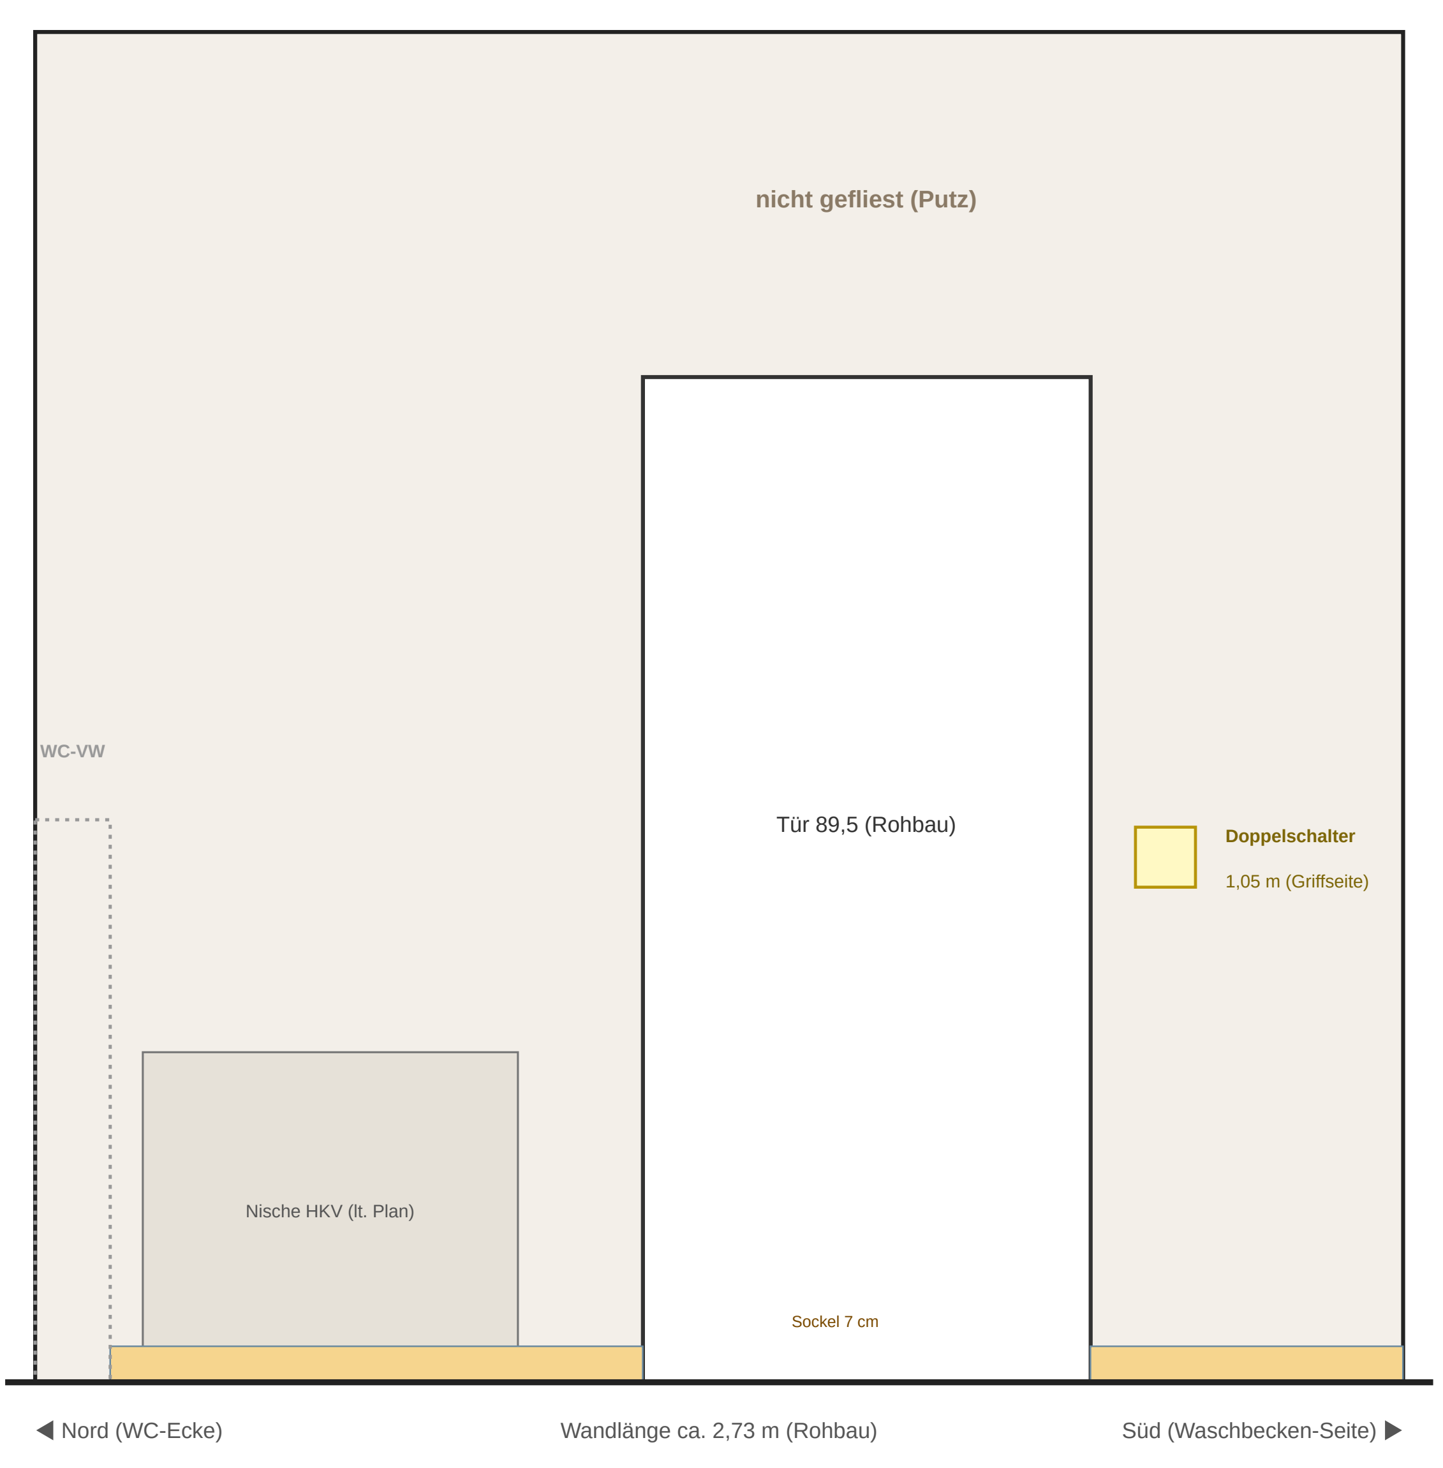
nicht gefliest (Putz)
WC-VW
Tür 89,5 (Rohbau)
Doppelschalter
1,05 m (Griffseite)
Nische HKV (lt. Plan)
Sockel 7 cm
◀ Nord (WC-Ecke)
Wandlänge ca. 2,73 m (Rohbau)
Süd (Waschbecken-Seite) ▶

🟦 ganze Fliese 60×30 ▭ volle Breite, in der Höhe geschnitten 🟨 Zuschnitt (Zahl = Maß in cm) — Fliesenkante 2,35 m

Fugen 3 mm · Reihenhöhen von unten: 26,6 / 6× 30 / 26,3 cm → Fuge genau auf Fensterbank (0,875) · Maße aus Plan „03A Dachgeschoss“, auf der Baustelle nachmessen! Decke/Dachschräge vereinfacht als 2,70 m dargestellt. Ansichten jeweils „vom Raum aus auf die Wand geschaut“. Badewanne gedreht: linke Längsseite parallel zur Wand.

🟫 ganze Bodenfliese