Bad DG – Fliesenplan Wände + Boden (Fliesen 60×30, 30 cm versetzt)

0 · Draufsicht Bad (Grundriss)

Norden oben · blau = gefliest bis 2,35 m · orange = Fliesensockel 7 cm · SD = Steckdose · Maße Rohbau lt. Plan

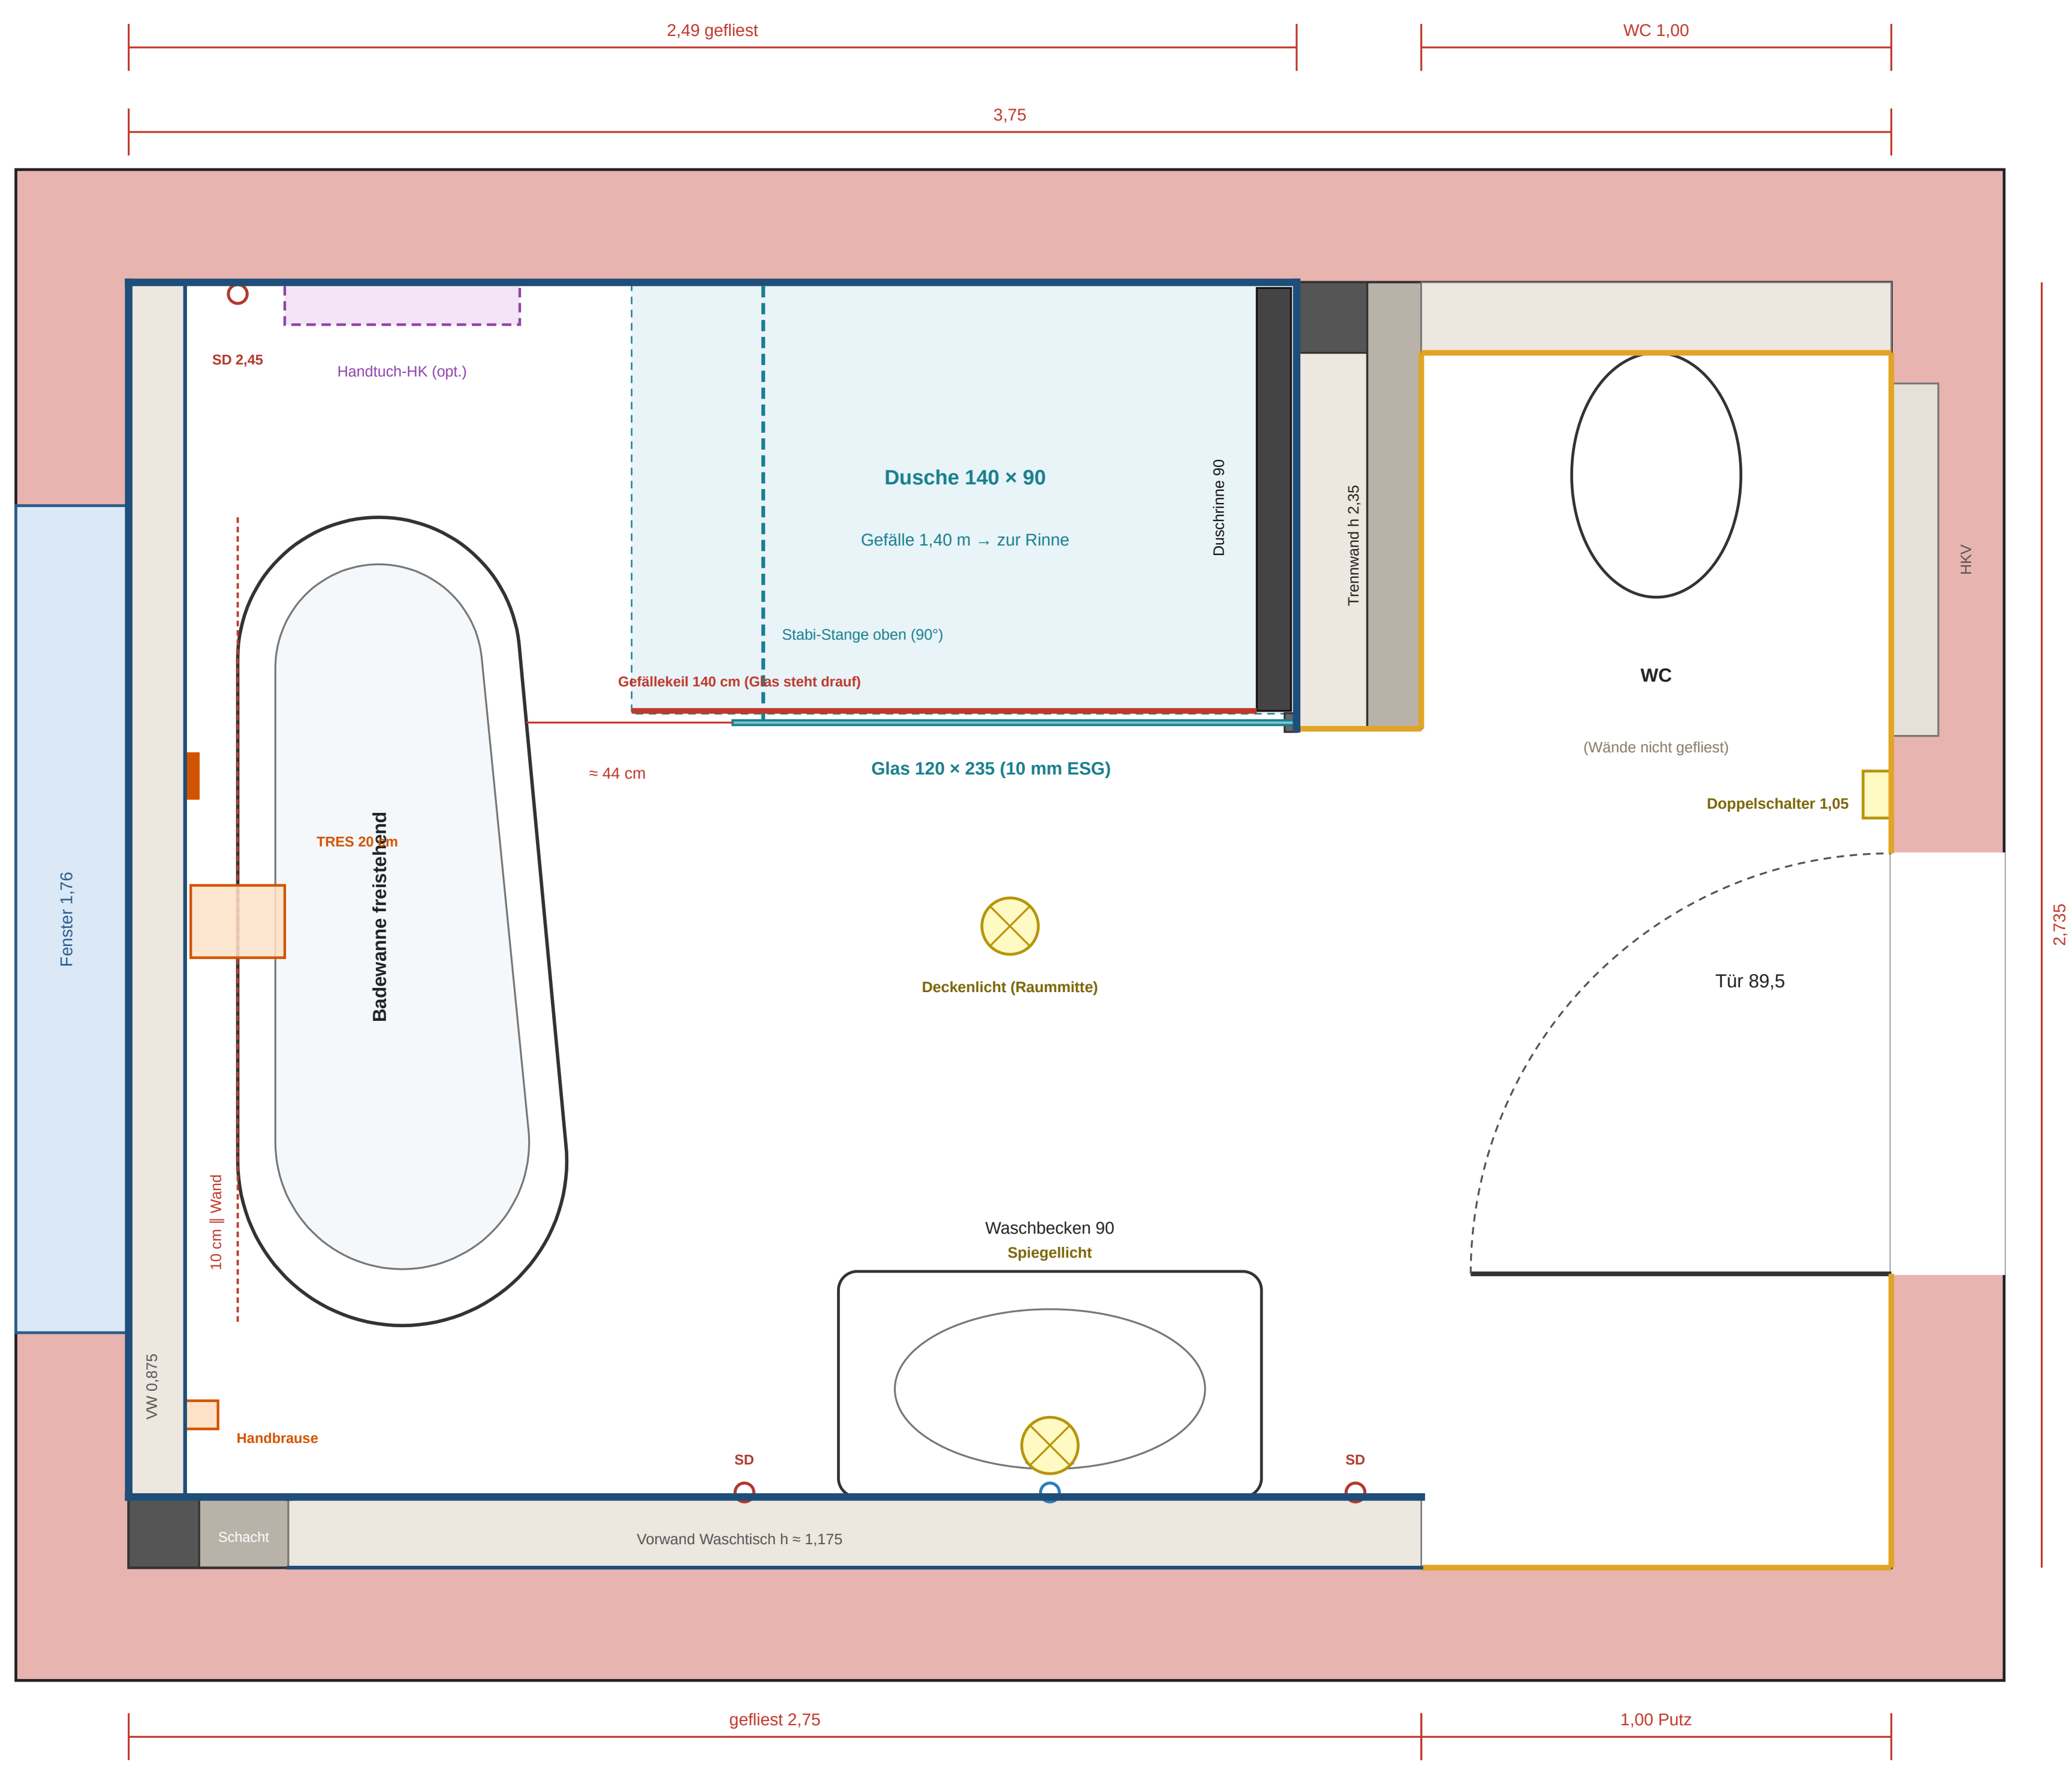

0a · Boden – Fliesen längs (Ost–West), 30 cm versetzt

60×30 · ca. 9,0 m² · ganze Reihen an der Duschwand · Streifen 13,7 cm unter der Waschtisch-Vorwand · Duschrinne 90 cm an der Trennwand, Gefälle über 1,40 m · Gefällekeil 140 cm an der Glaslinie

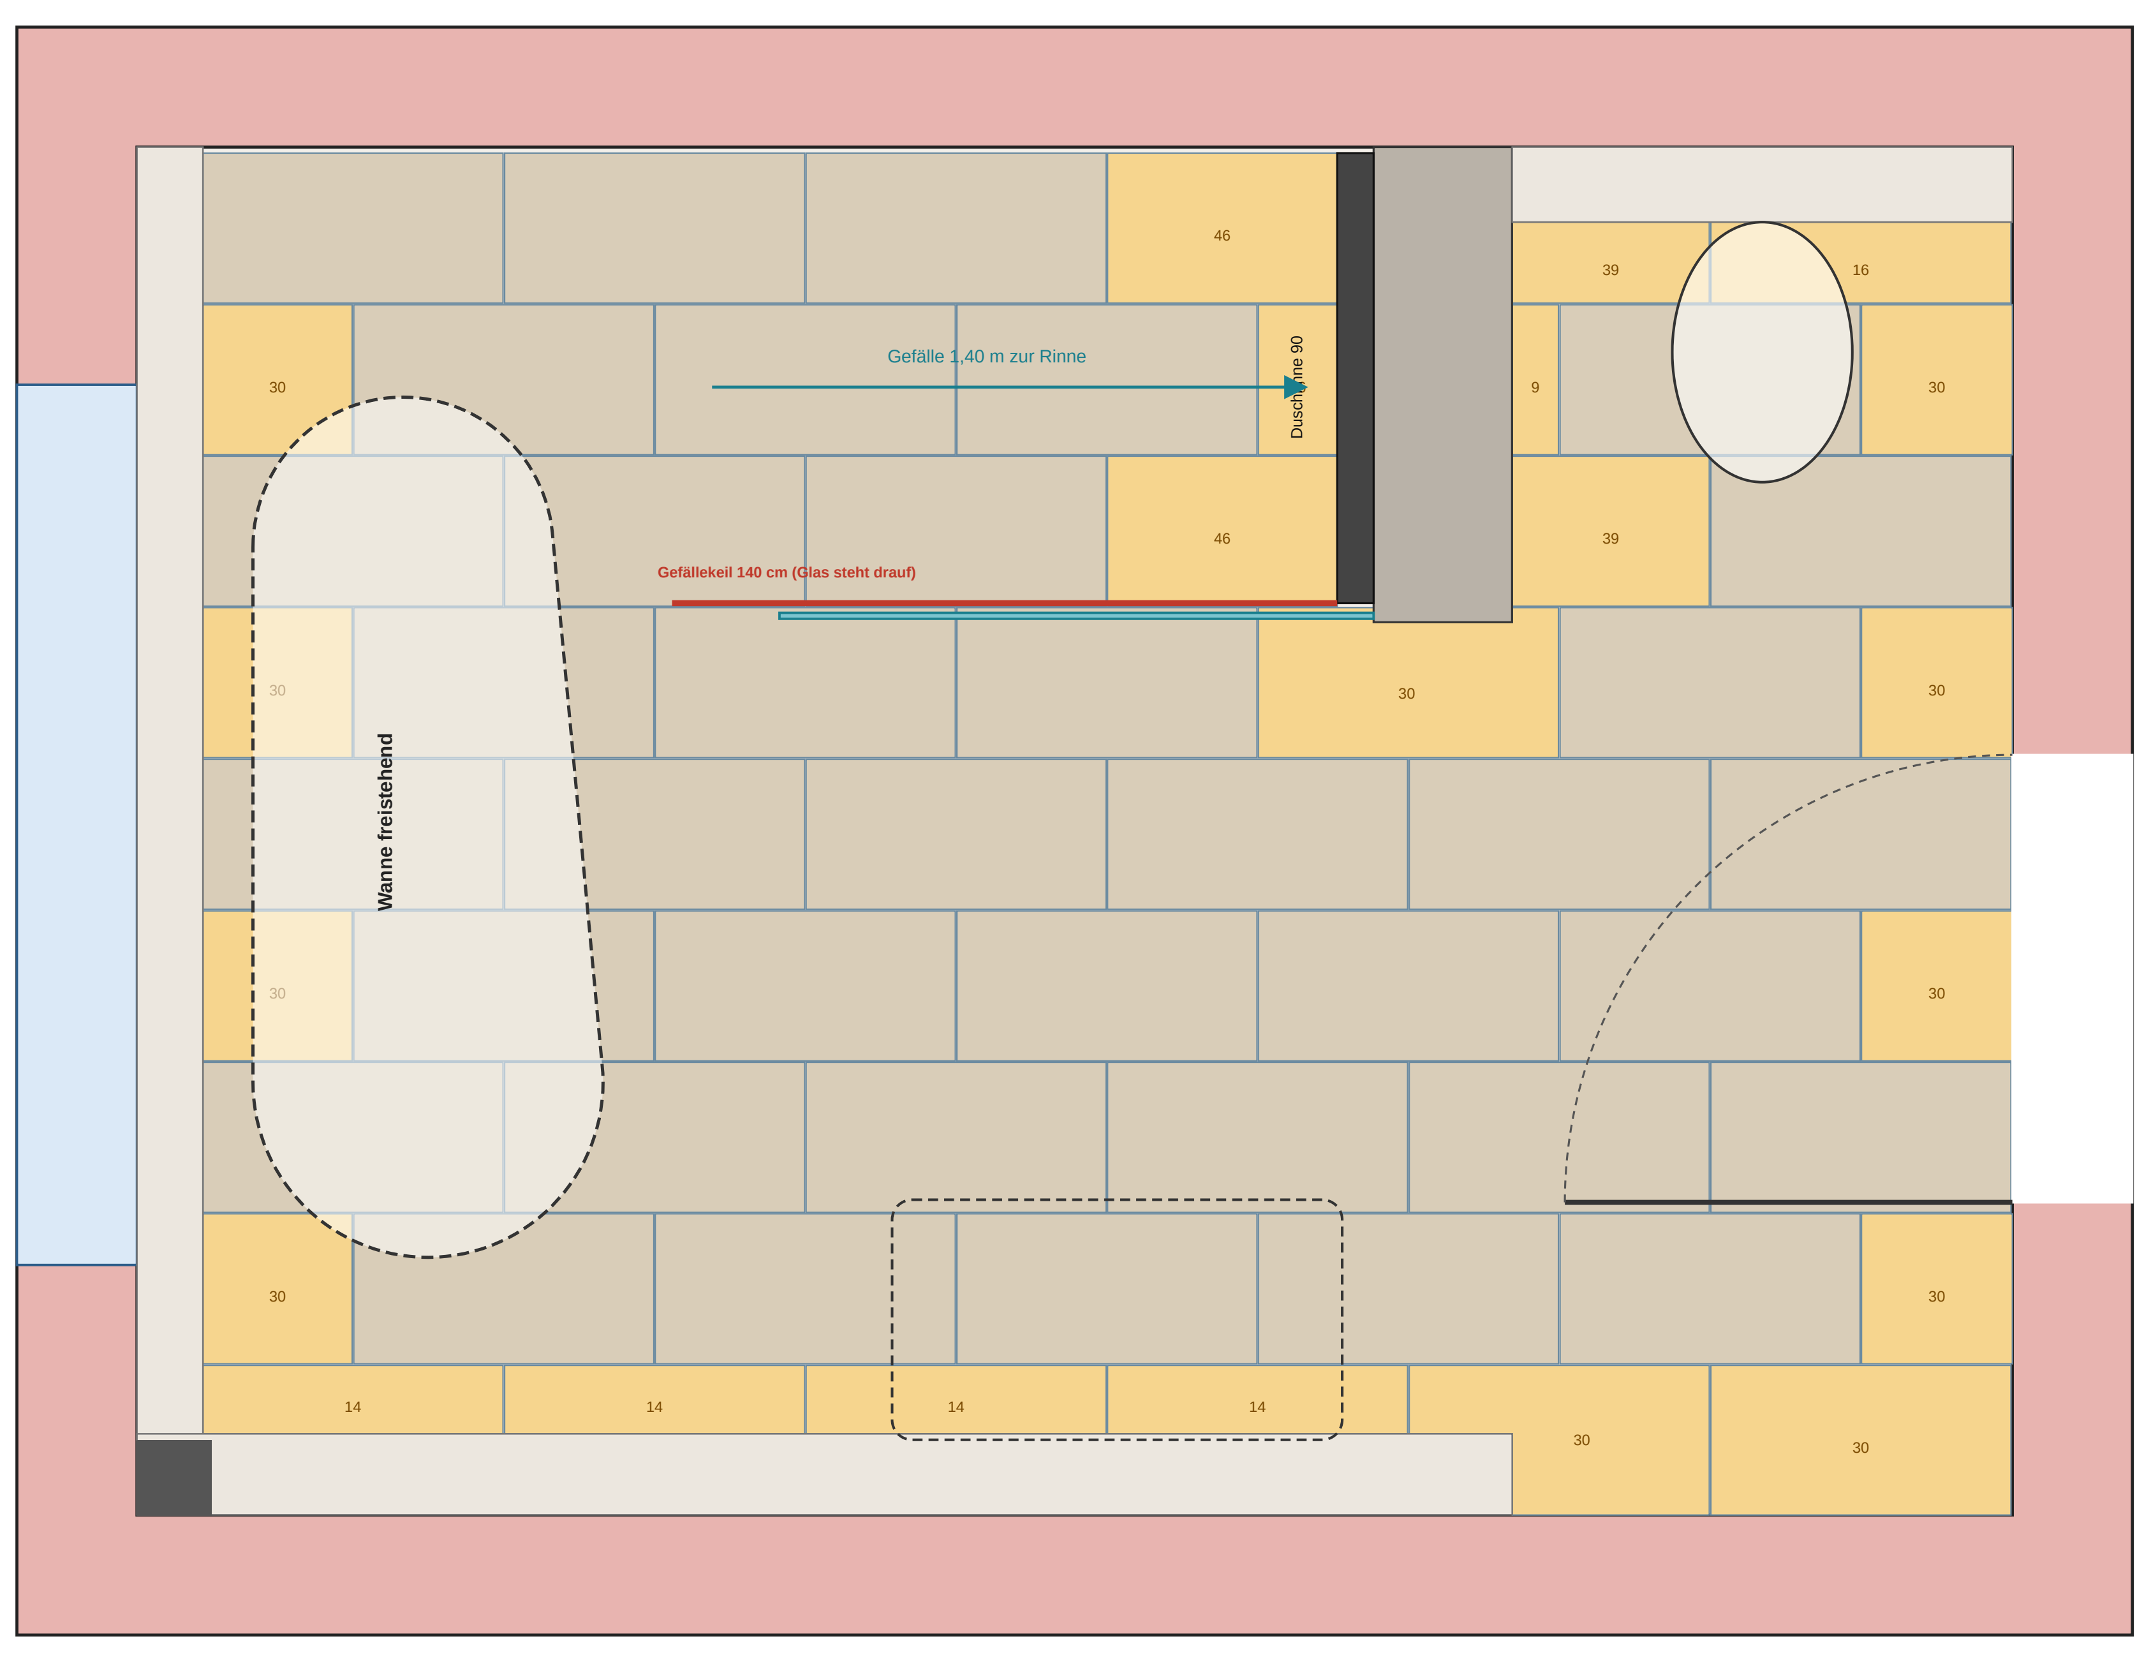

1 · Wand Badewanne / Fenster (Westen)

Blick nach Westen · komplett gefliest bis 2,35 m · Fenster: Brüstung ca. 0,875 / Sturz ca. 2,09 ab FFB (lt. Plan)

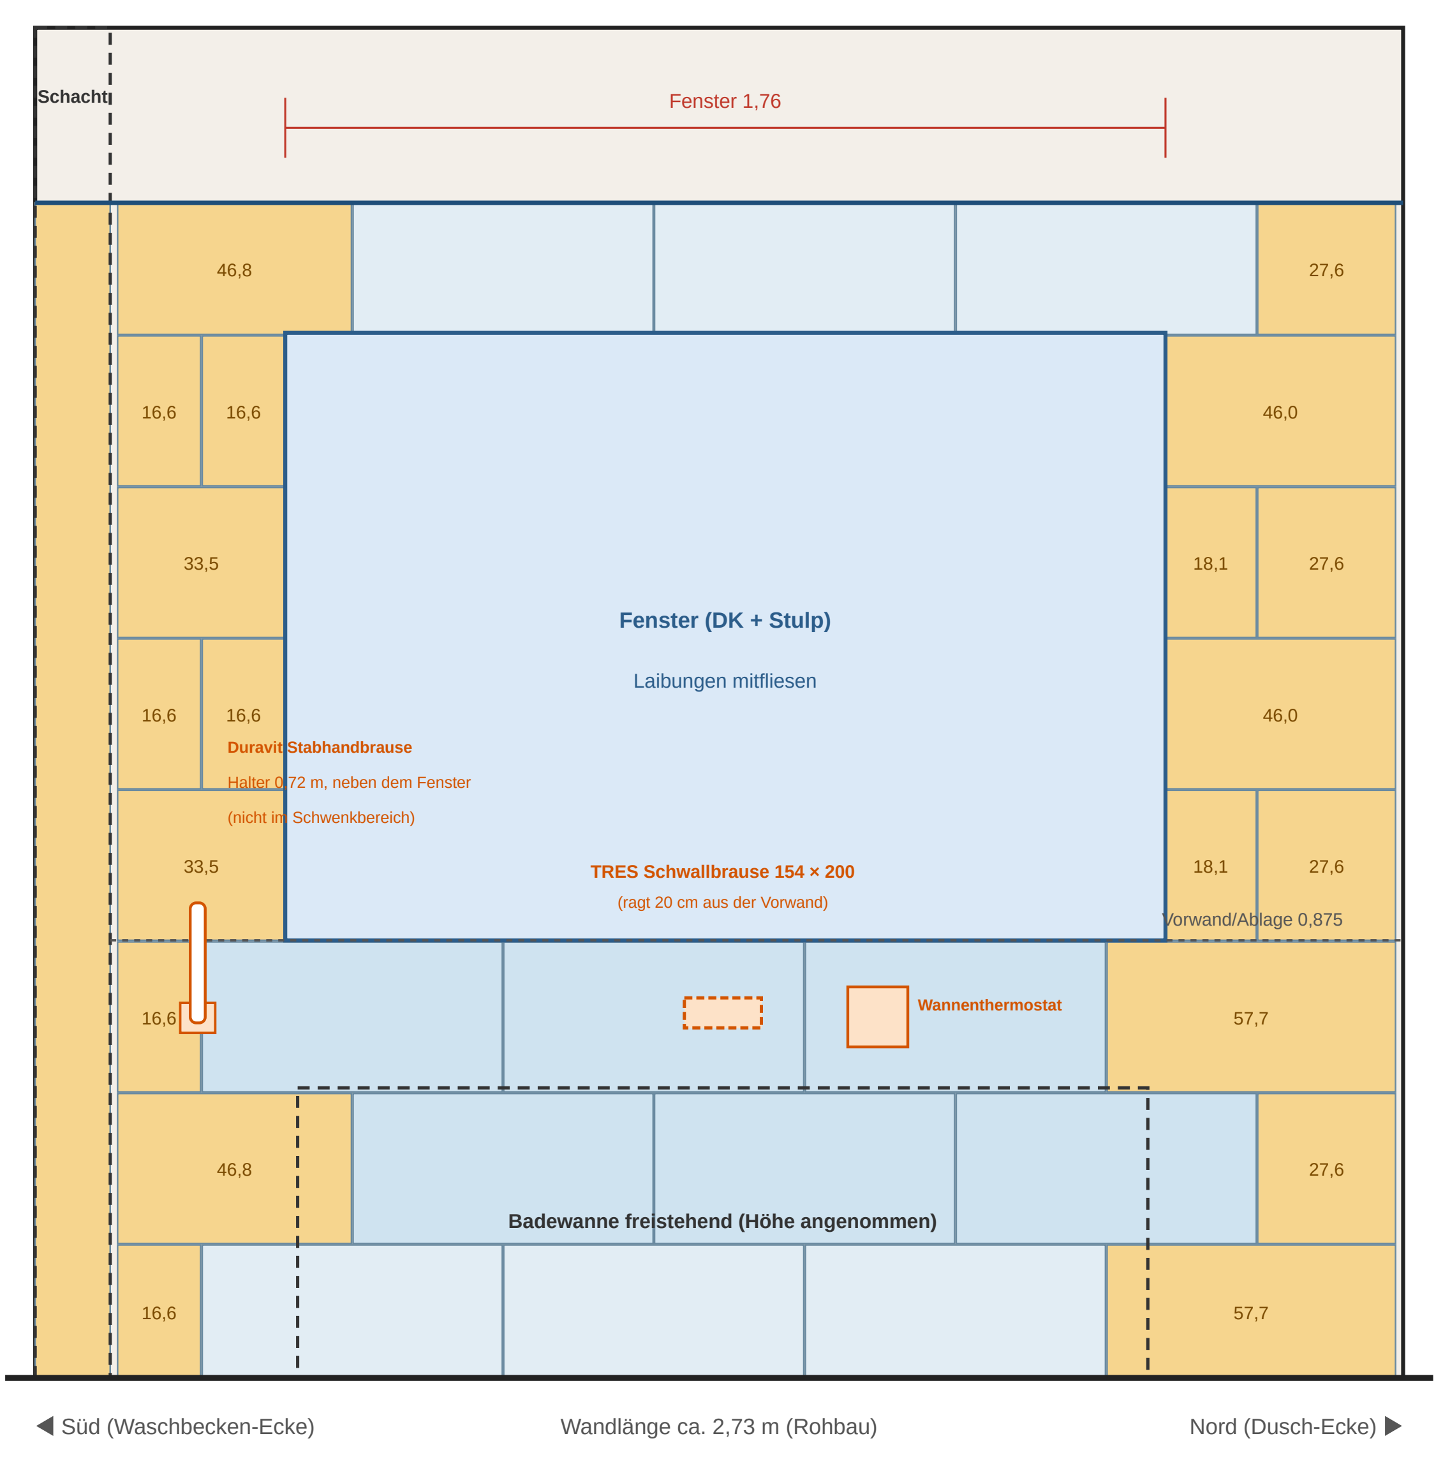

2 · Wand Dusche / WC (Norden)

Blick nach Norden · gefliest von der Wannen-Ecke bis zur Trennwand (2,49 m) · WC-Nische (1,00 m) nicht gefliest · Trennwand 2,35 hoch

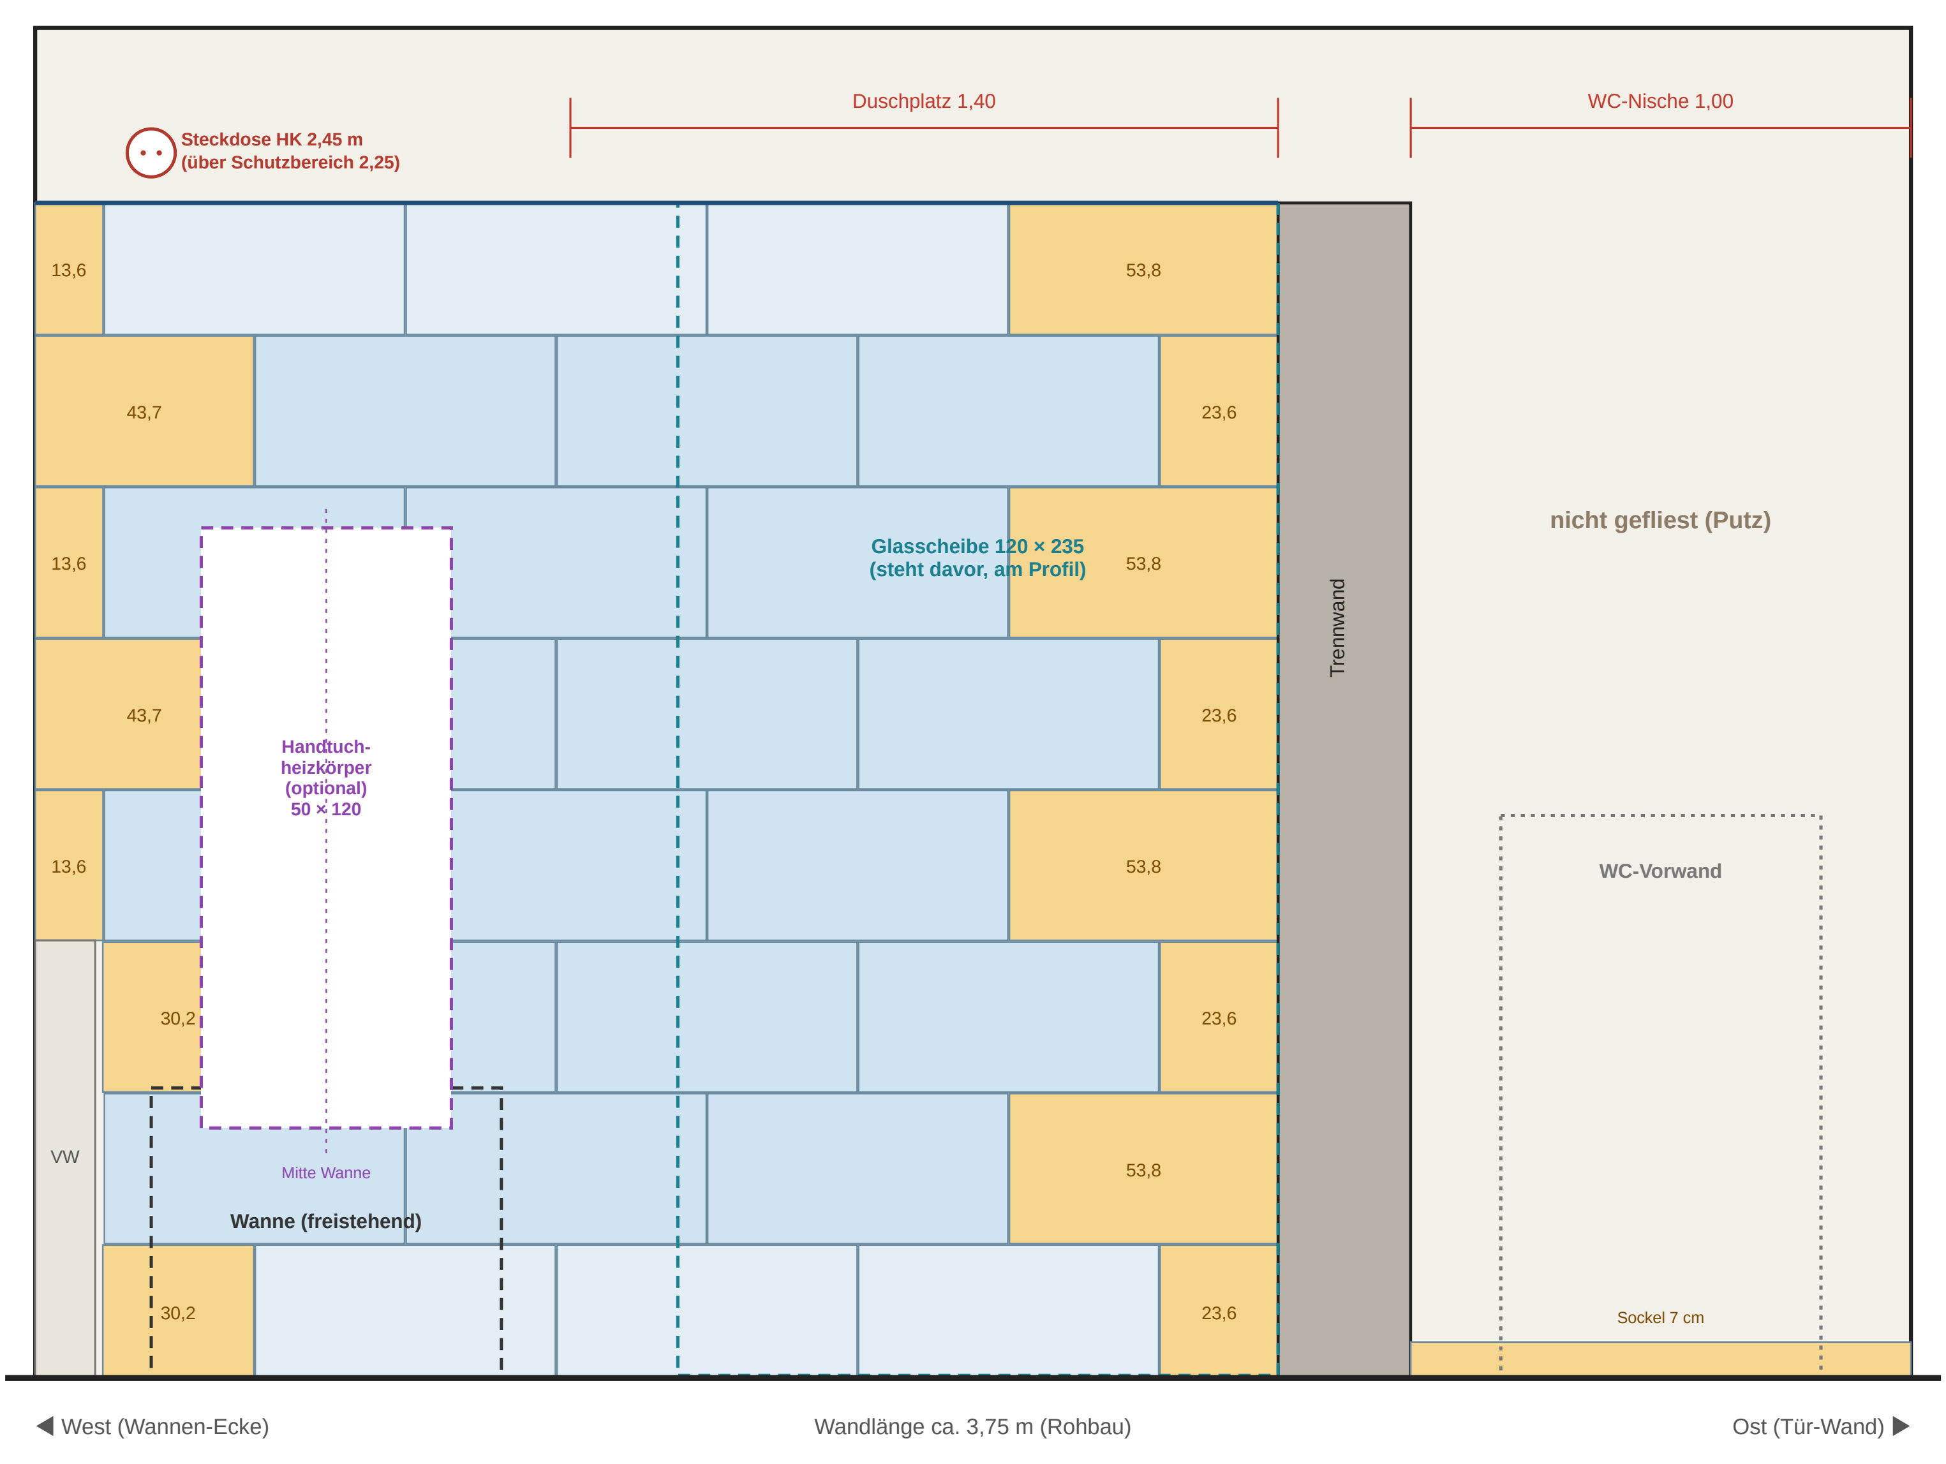

3 · Trennwand – Duschseite (mit Glasprofil)

Blick nach Osten aus der Dusche · Höhe 2,35 m = Fliesenkante = Glasoberkante · Reihe A: ganze Fliese am Profil, Reihe B: ganze Fliese in der Ecke

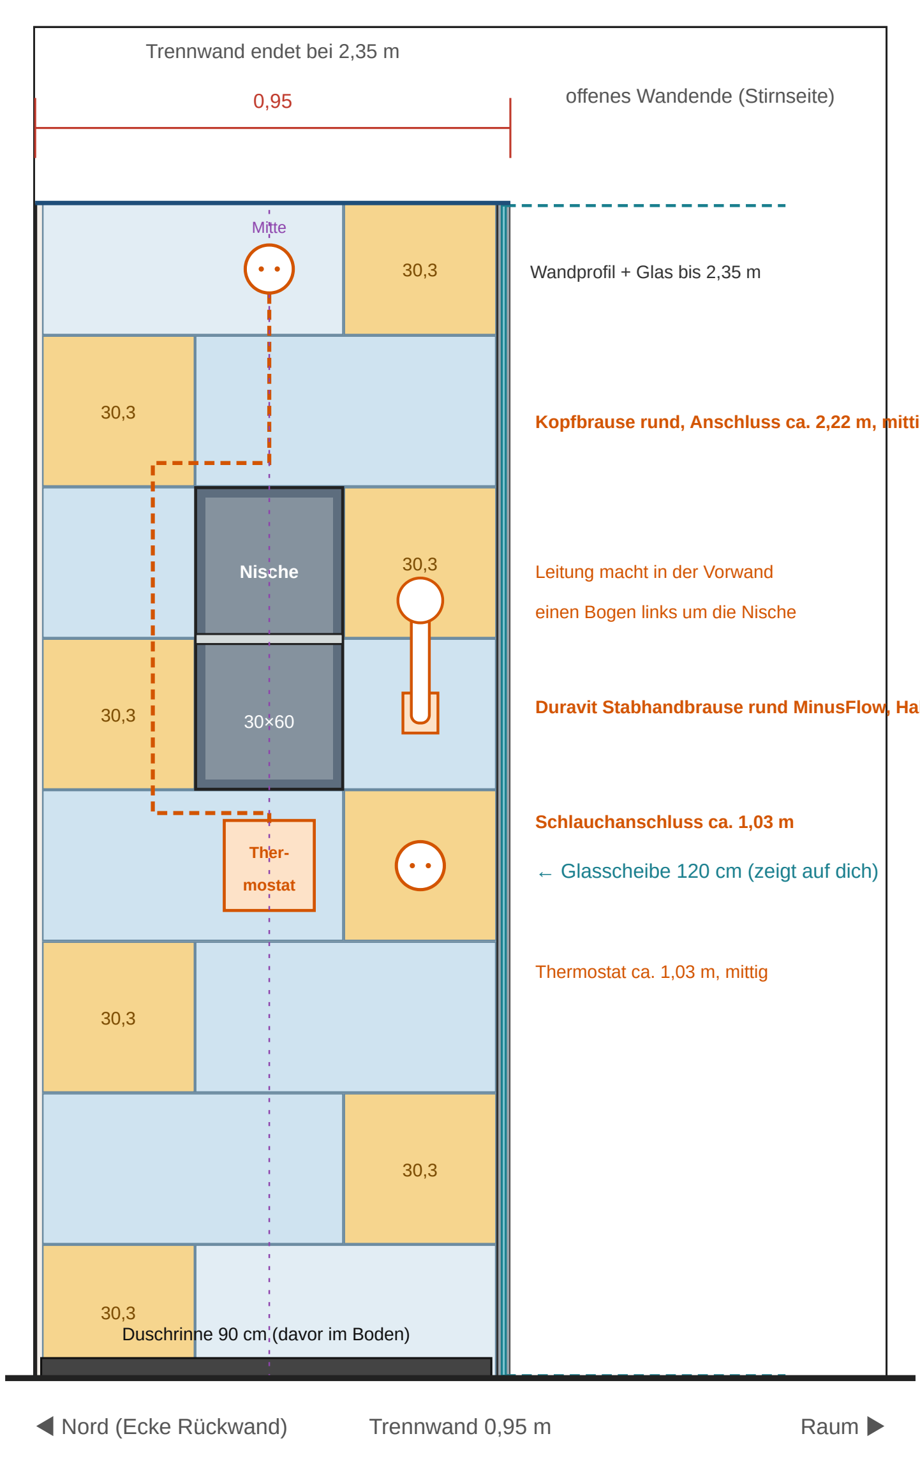
Trennwand endet bei 2,35 m
0,95
offenes Wandende (Stirnseite)
Mitte
30,3
Wandprofil + Glas bis 2,35 m
30,3
Kopfbrause rund, Anschluss ca. 2,22 m, mittig
Nische
30,3
Leitung macht in der Vorwand
einen Bogen links um die Nische
30,3
30×60
Duravit Stabhandbrause rund MinusFlow, Halter ca. 1,33 m
Ther-
mostat
Schlauchanschluss ca. 1,03 m
← Glasscheibe 120 cm (zeigt auf dich)
Thermostat ca. 1,03 m, mittig
30,3
30,3
30,3
Duschrinne 90 cm (davor im Boden)
◀ Nord (Ecke Rückwand)
Trennwand 0,95 m
Raum ▶

4 · Wand Waschbecken (Süden)

Blick nach Süden · gefliest von der Wannen-Ecke bis 2,75 m (Ende Vorwand) · die ersten 1,00 m an der Tür-Seite nicht gefliest

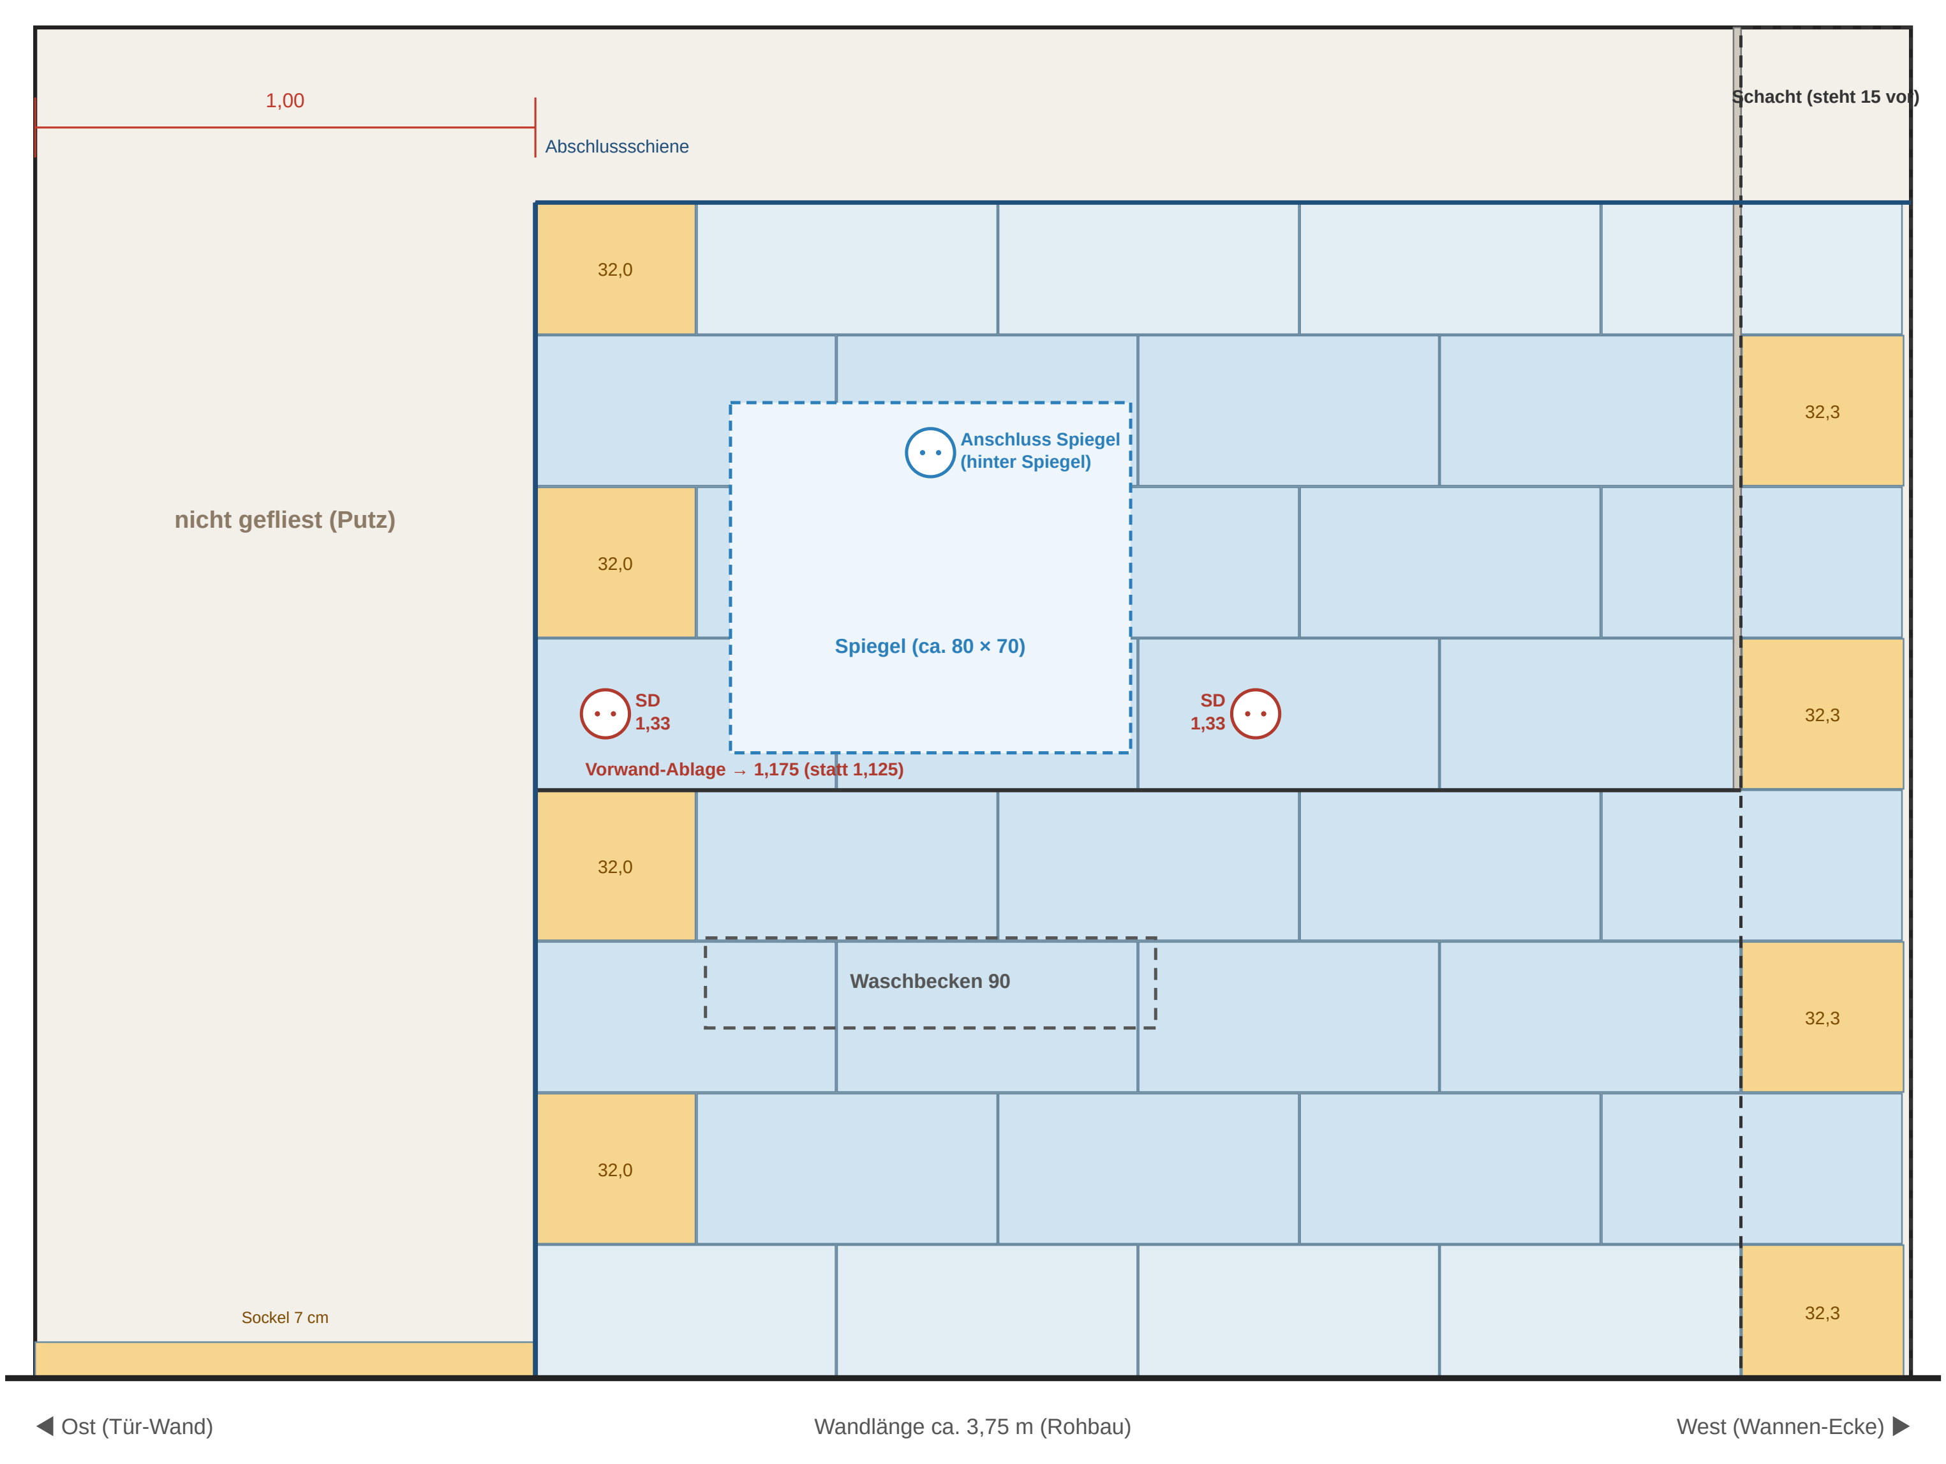

5 · Wand mit Tür (Osten)

Blick nach Osten · nicht gefliest, nur Fliesensockel 7 cm

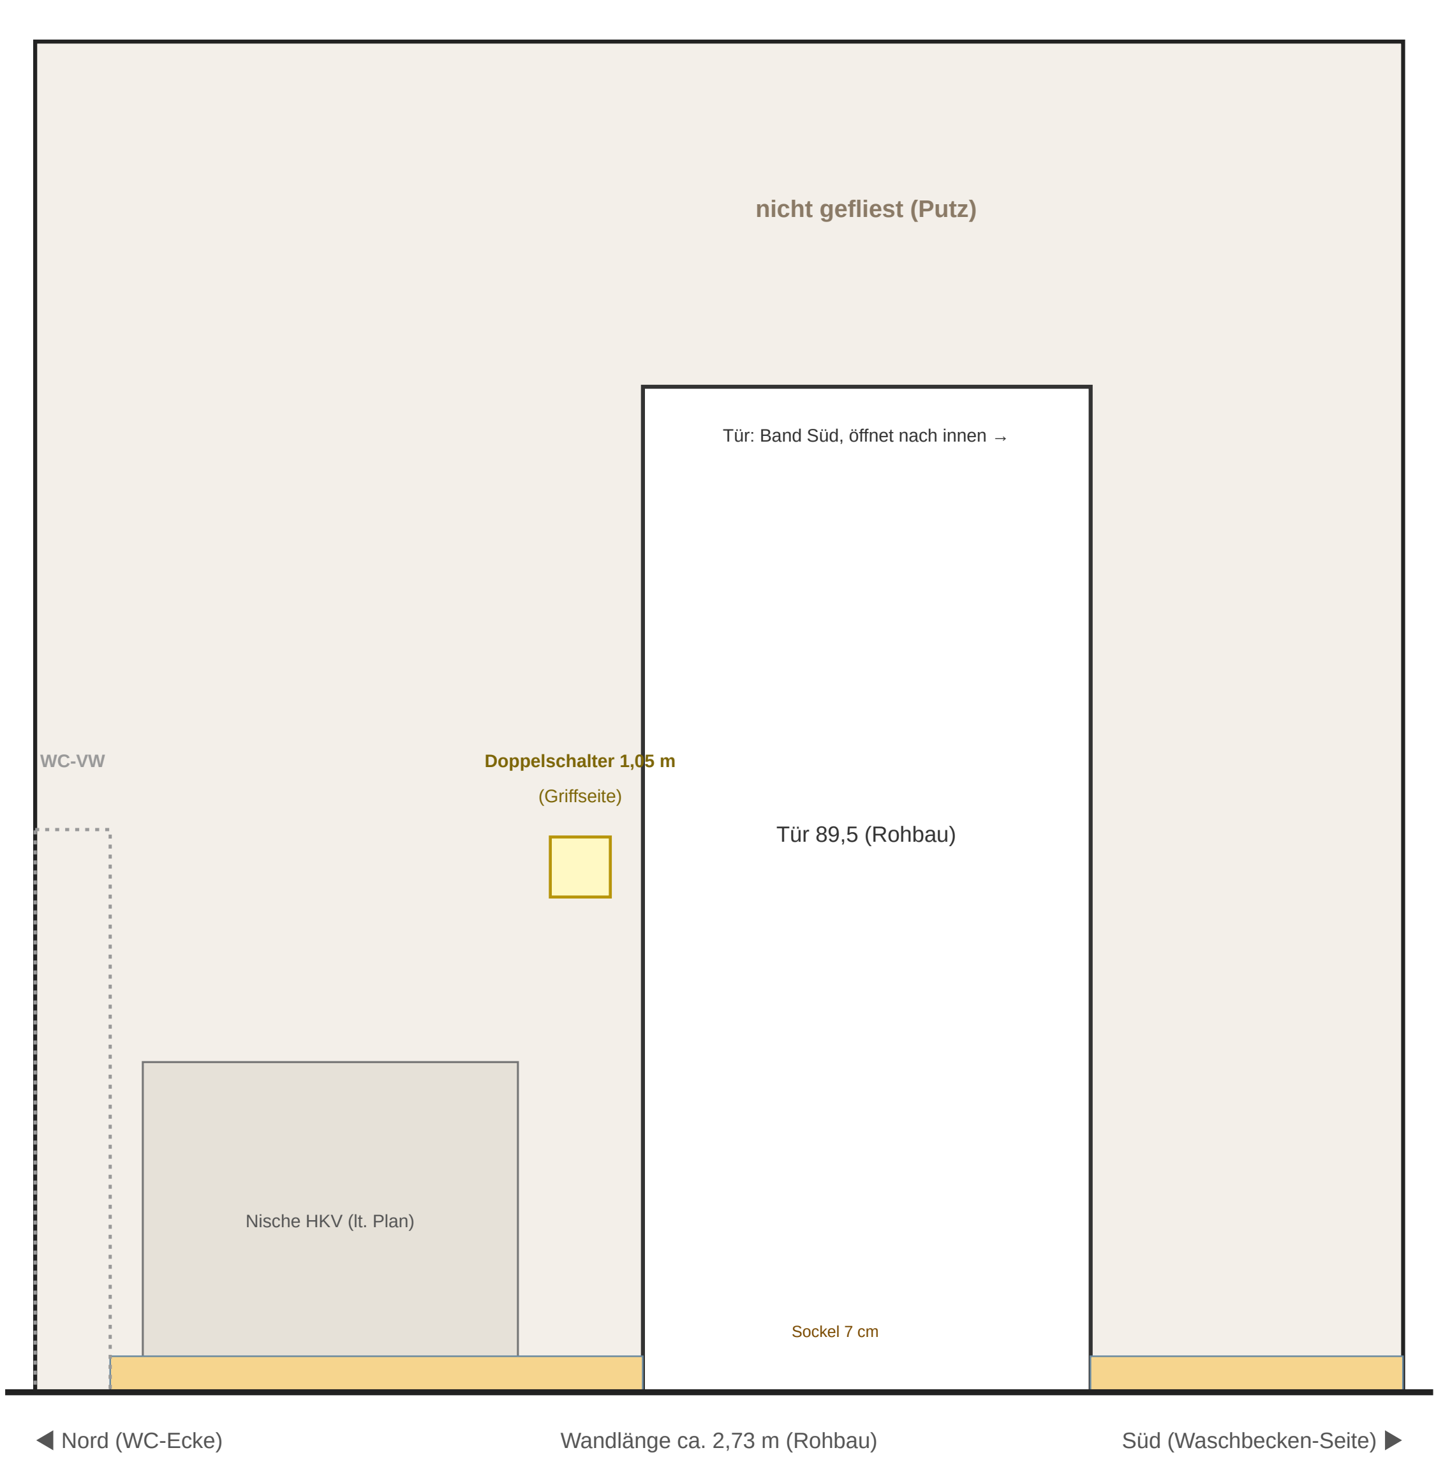

🟦 ganze Fliese 60×30 ◻ volle Breite, in der Höhe geschnitten 🟨 Zuschnitt (Zahl = Maß in cm) — Fliesenkante 2,35 m

Fugen 3 mm · Reihenhöhen von unten: 26,6 / 6× 30 / 26,3 cm → Fuge genau auf Fensterbank (0,875) · Maße aus Plan „03A Dachgeschoss“, auf der Baustelle nachmessen! Decke/Dachschräge vereinfacht als 2,70 m dargestellt. Ansichten jeweils „vom Raum aus auf die Wand geschaut“. Badewanne gedreht: linke Längsseite parallel zur Wand.

🟫 ganze Bodenfliese