Bad DG – Fliesenplan Wände + Boden (Fliesen 60×30, 30 cm versetzt)

0 · Draufsicht Bad (Grundriss)

Norden oben · blau = gefliest (Dusche + Trennwand bis 2,21 m ab FFB = 2,35 ab RFB, Fensterwand bis 0,875, Waschbeckenwand bis 1,125) · orange = Fliesensockel 7 cm · SD = Steckdose · Maße Rohbau lt. Plan

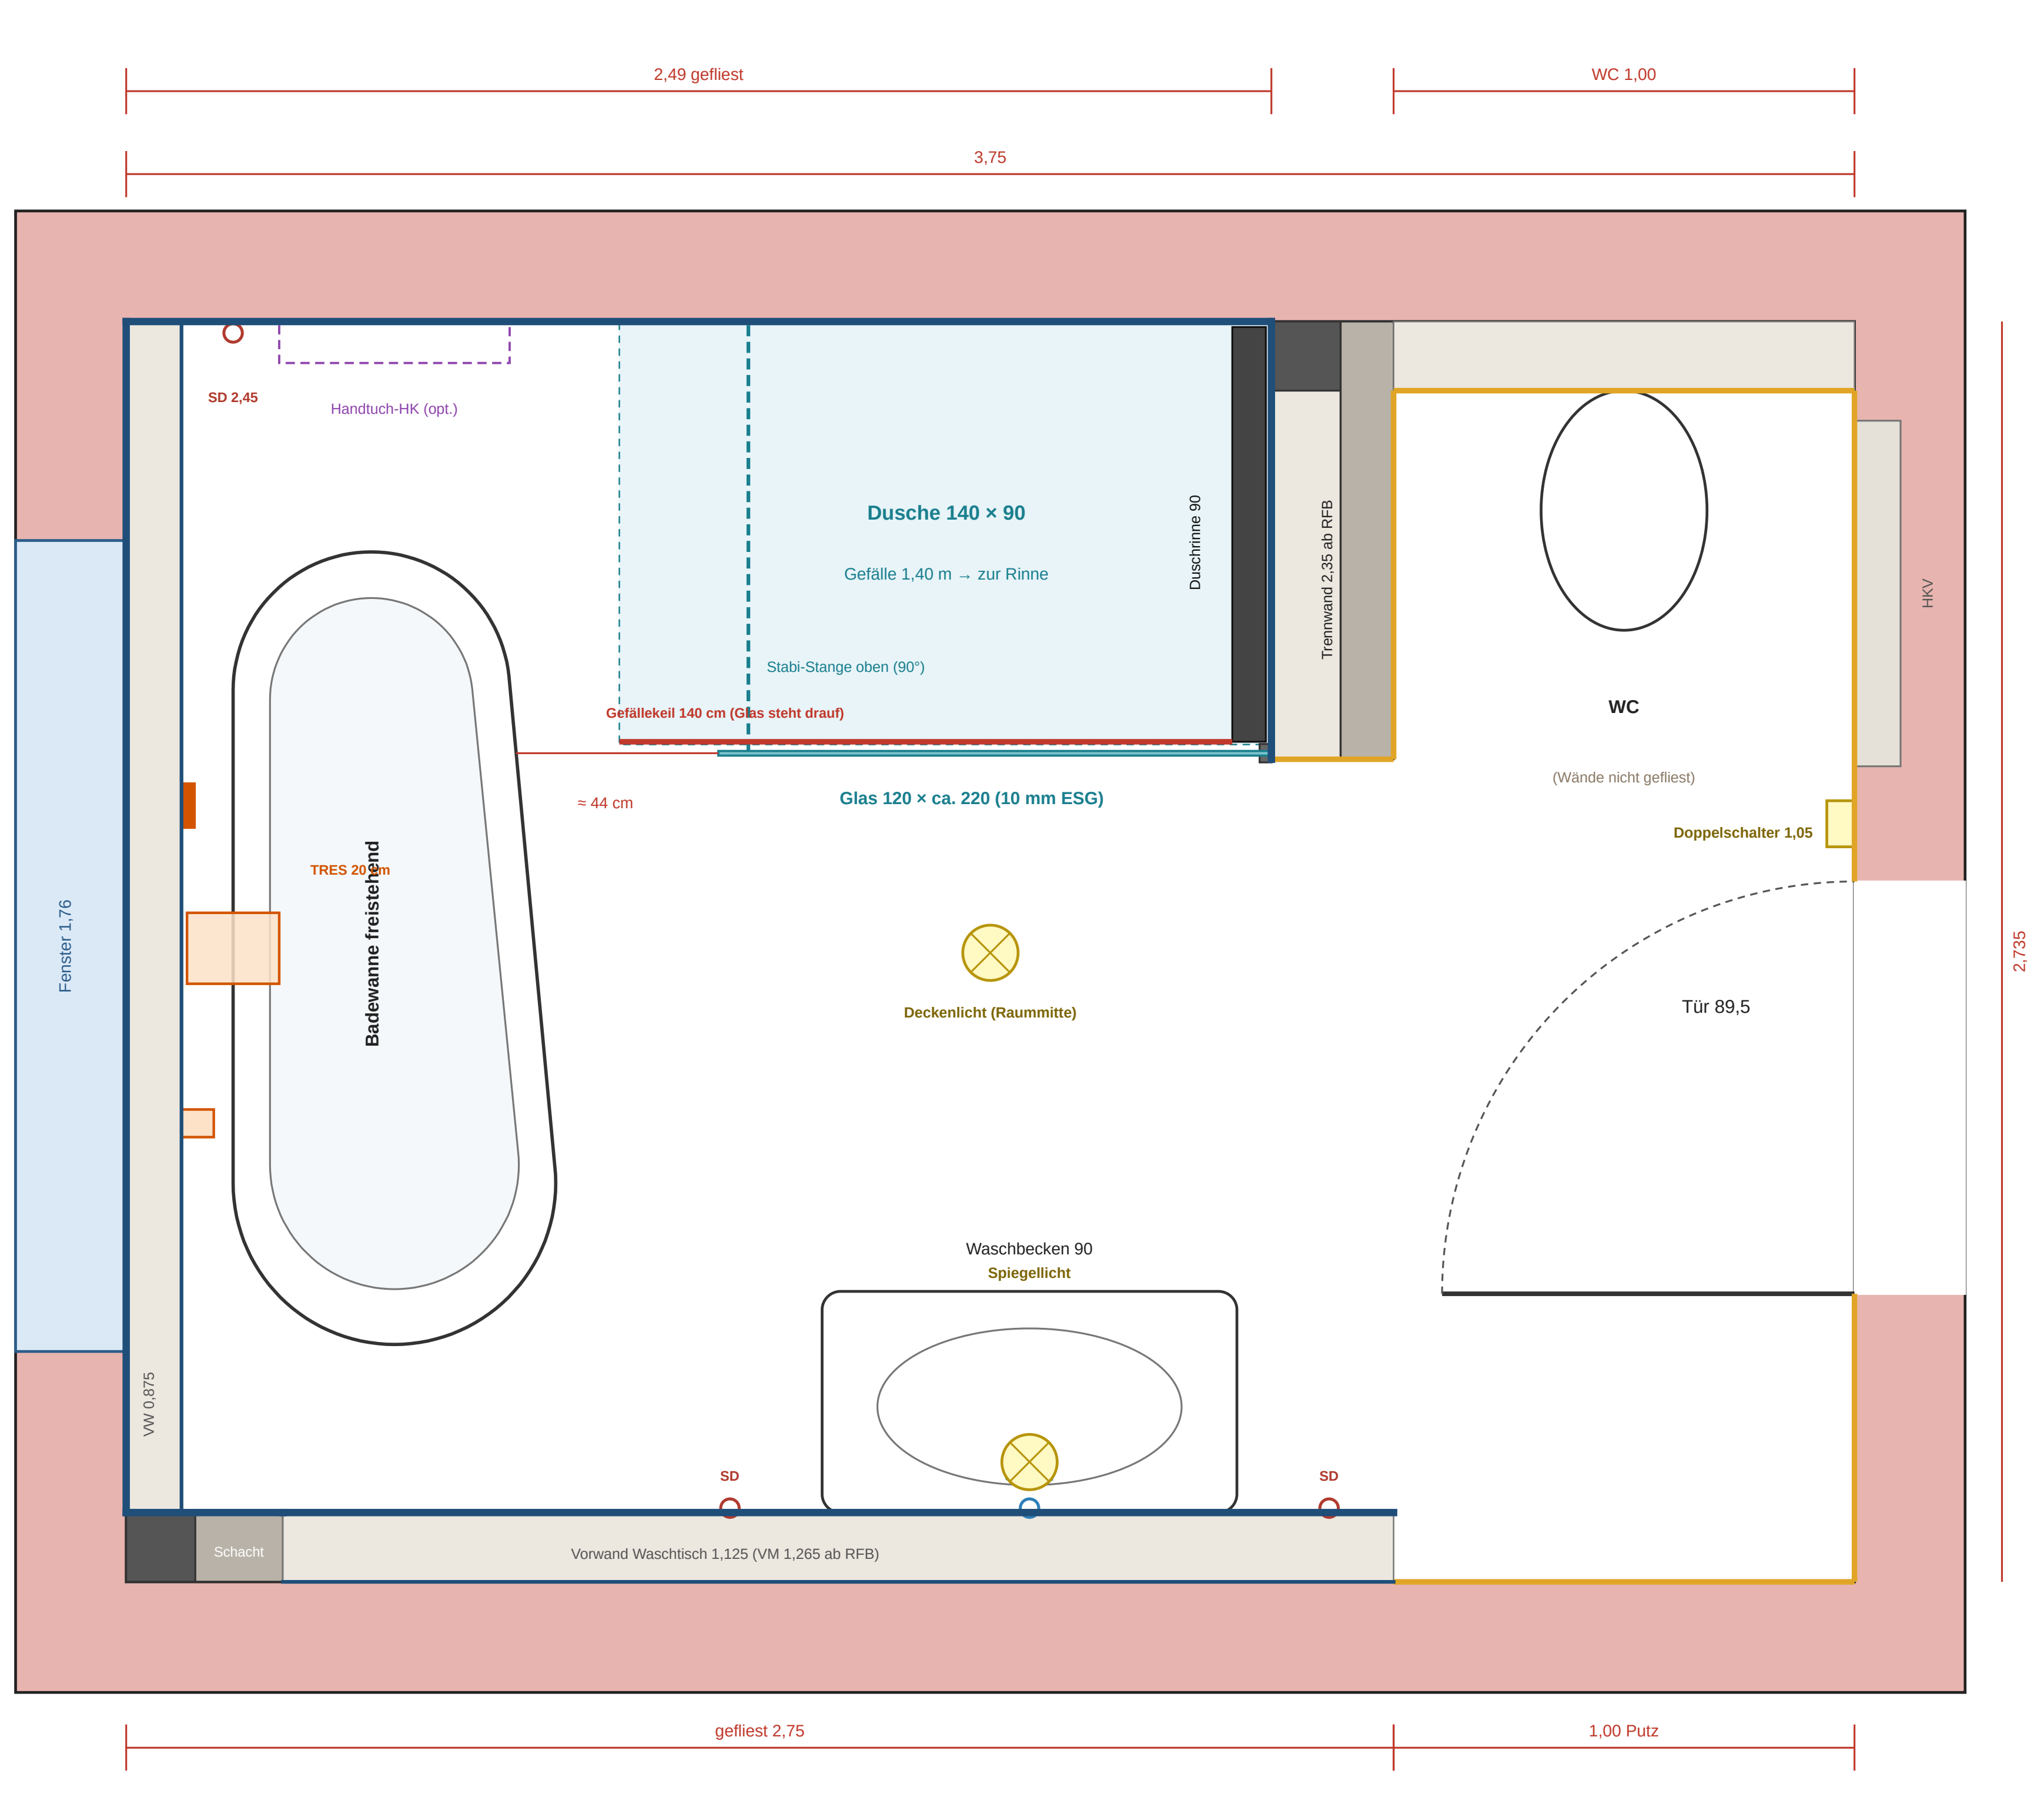

0a · Boden – Fliesen längs (Ost–West), 30 cm versetzt

60×30 · ca. 9,0 m² · ganze Reihen an der Duschwand · Streifen 13,7 cm unter der Waschtisch-Vorwand · Duschrinne 90 cm an der Trennwand, Gefälle über 1,40 m · Gefällekeil 140 cm an der Glaslinie

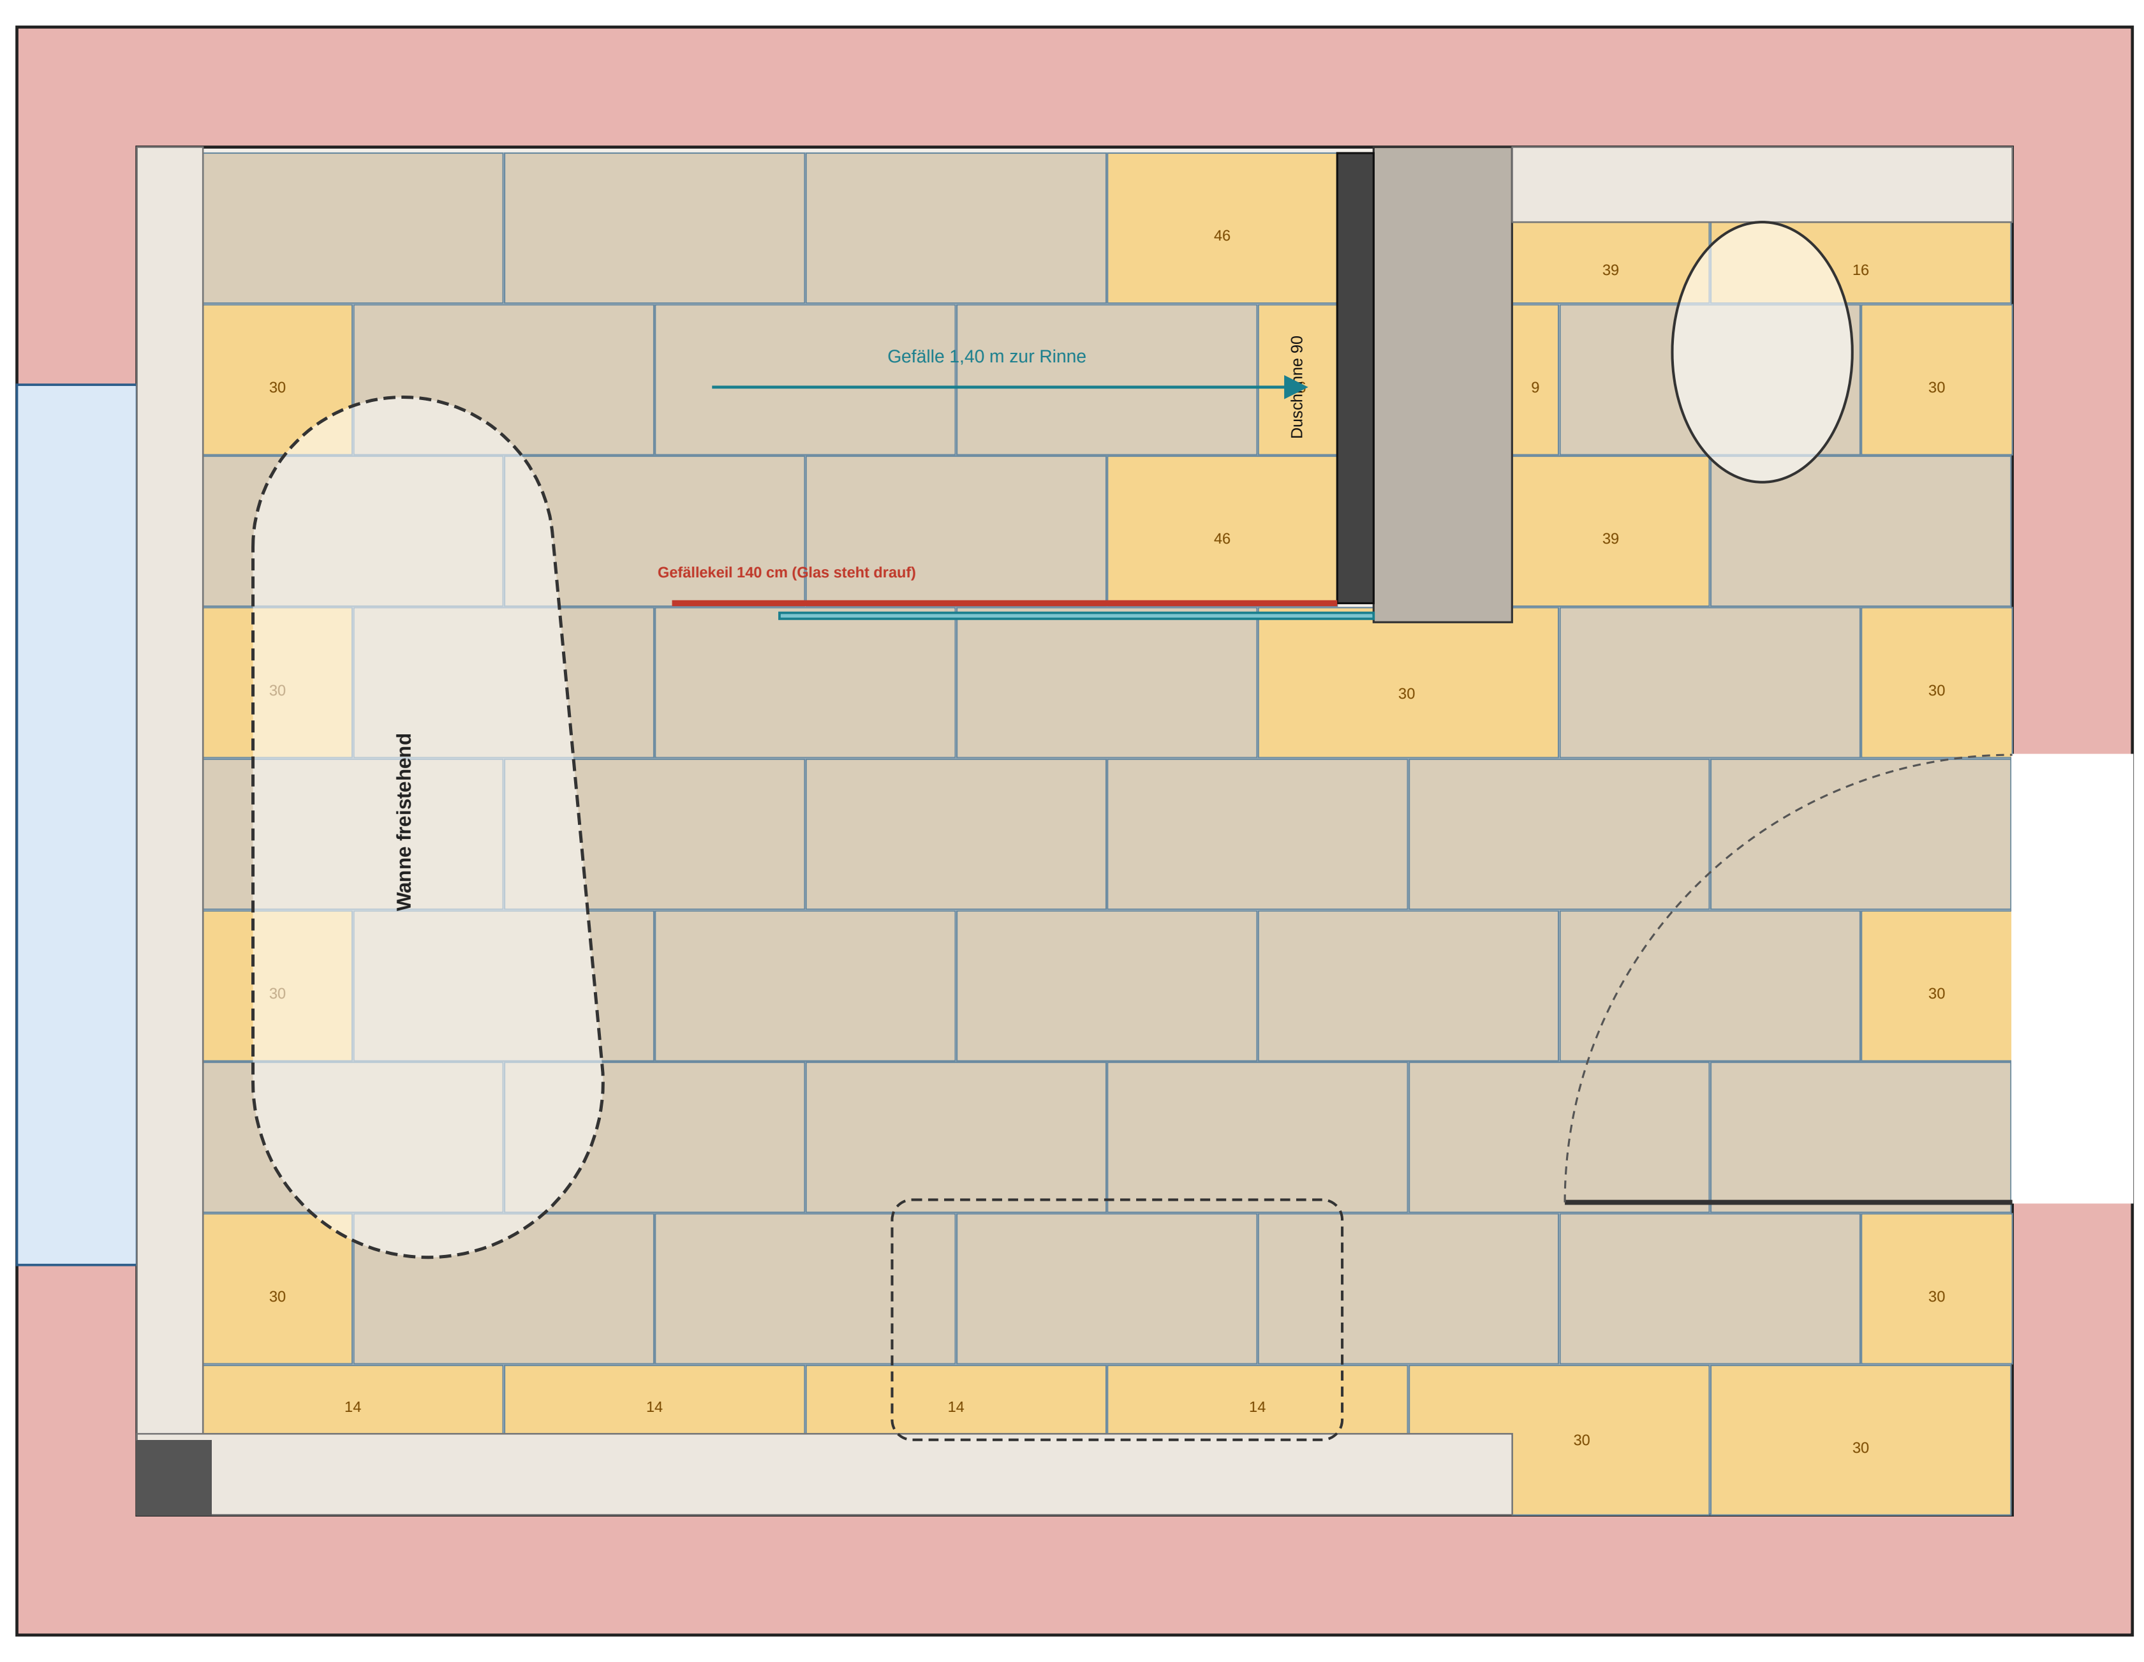

1 · Wand Badewanne / Fenster (Westen)

Blick nach Westen · Fliesen nur auf der Vorwand (bis 0,875 m) und oben auf der Ablage, darüber Putz

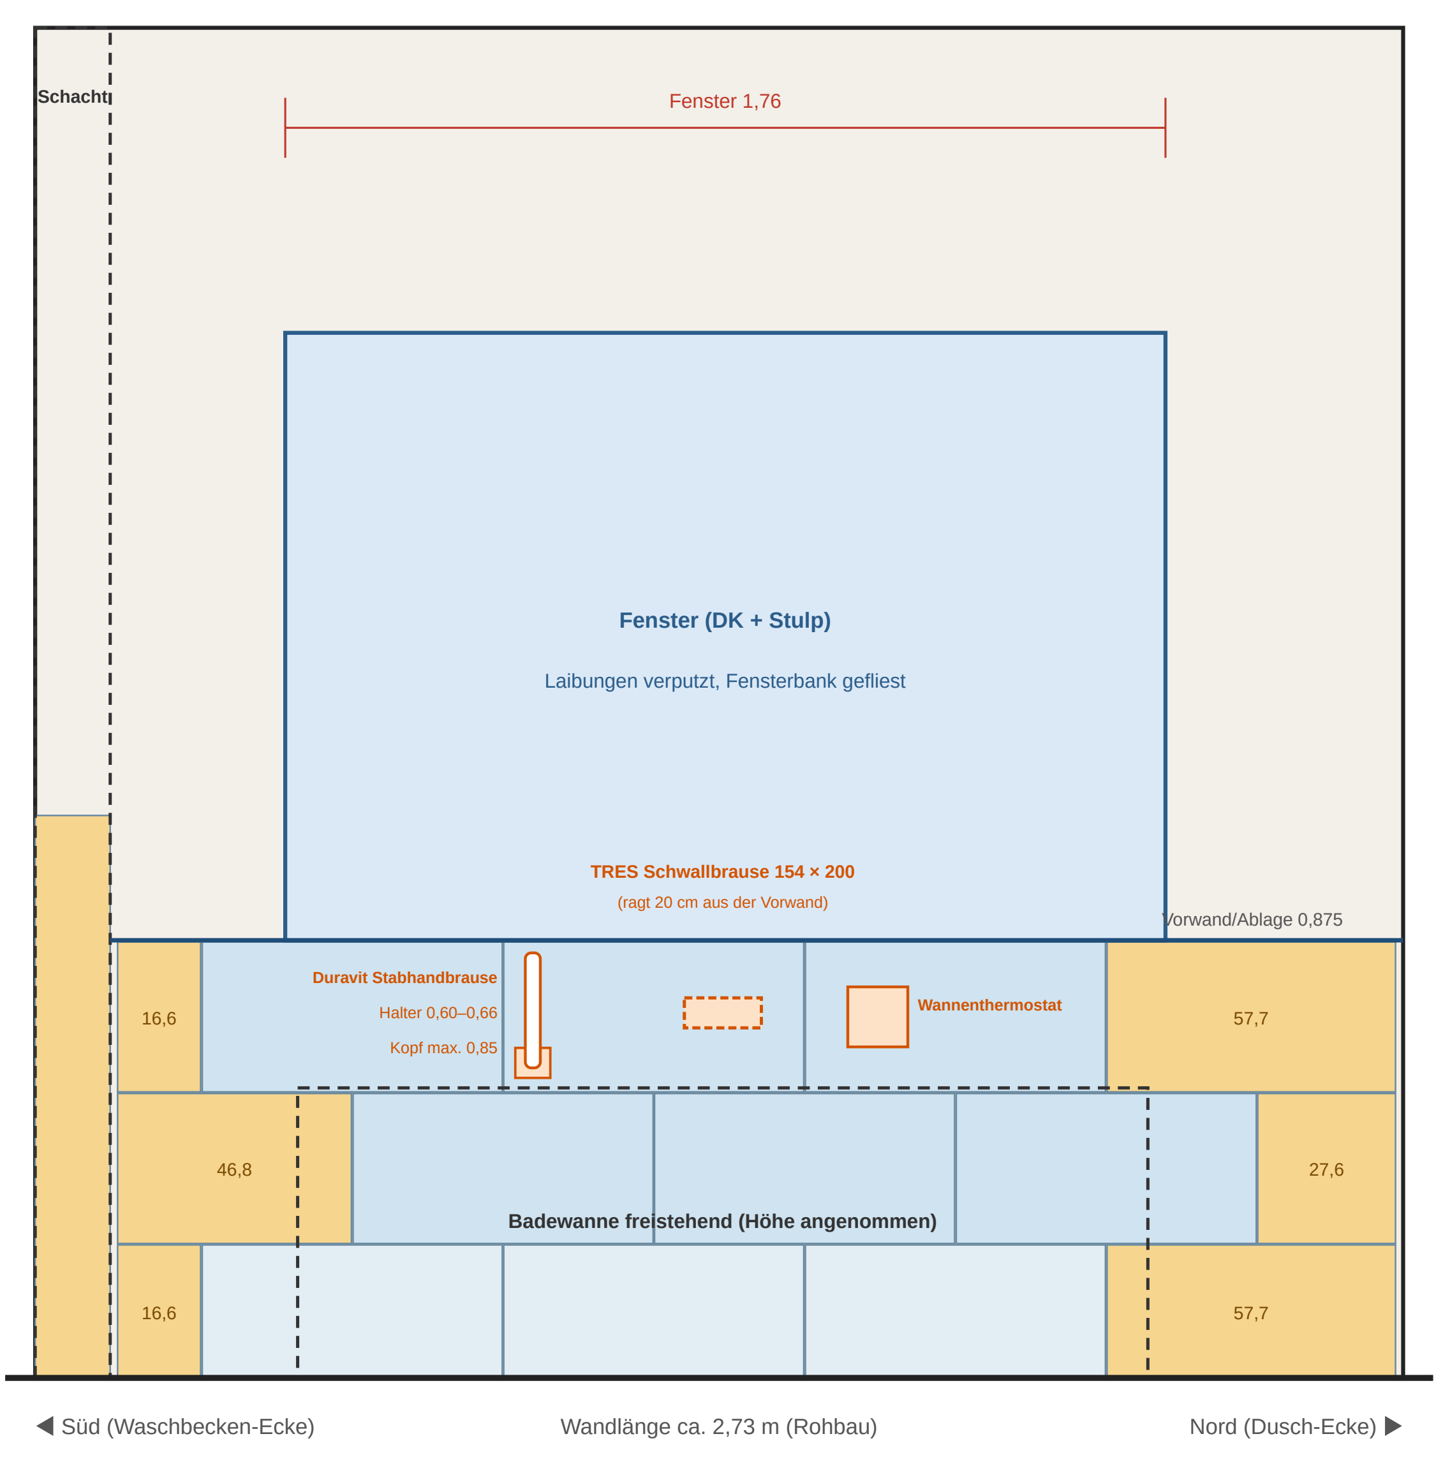

2 · Wand Dusche / WC (Norden)

Blick nach Norden · gefliest bis 2,21 m ab FFB (= 2,35 ab RFB) von der Wannen-Ecke bis zur Trennwand · WC-Nische nur Sockel

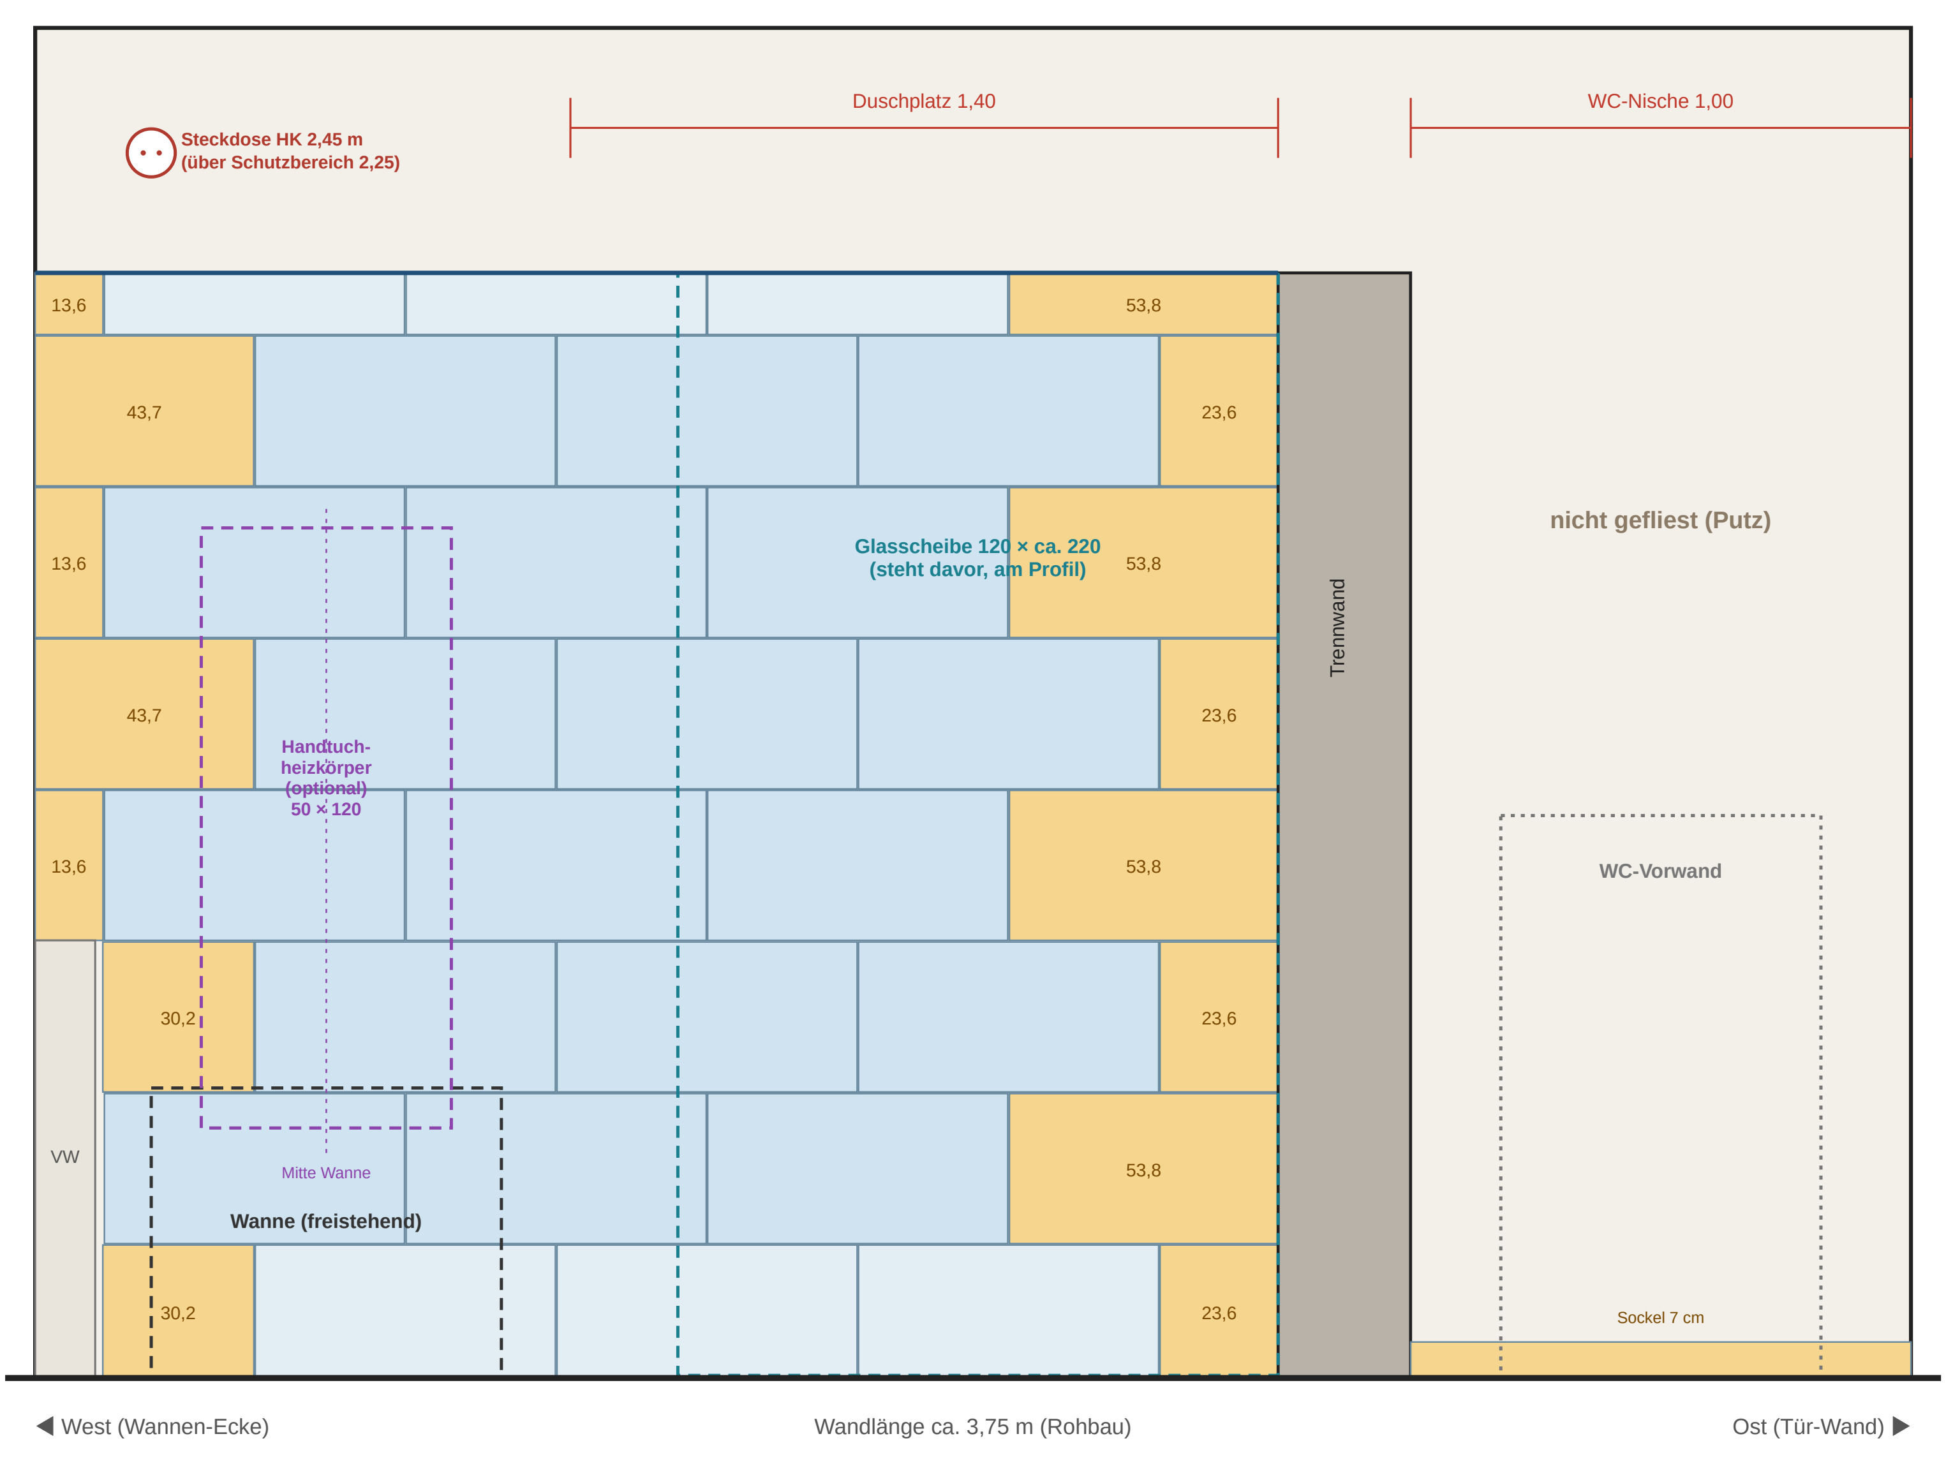

3 · Trennwand – Duschseite (mit Glasprofil)

Blick nach Osten aus der Dusche · Trennwand, Fliesen und Glas bis 2,21 m ab FFB (= 2,35 ab RFB lt. Werkplan)

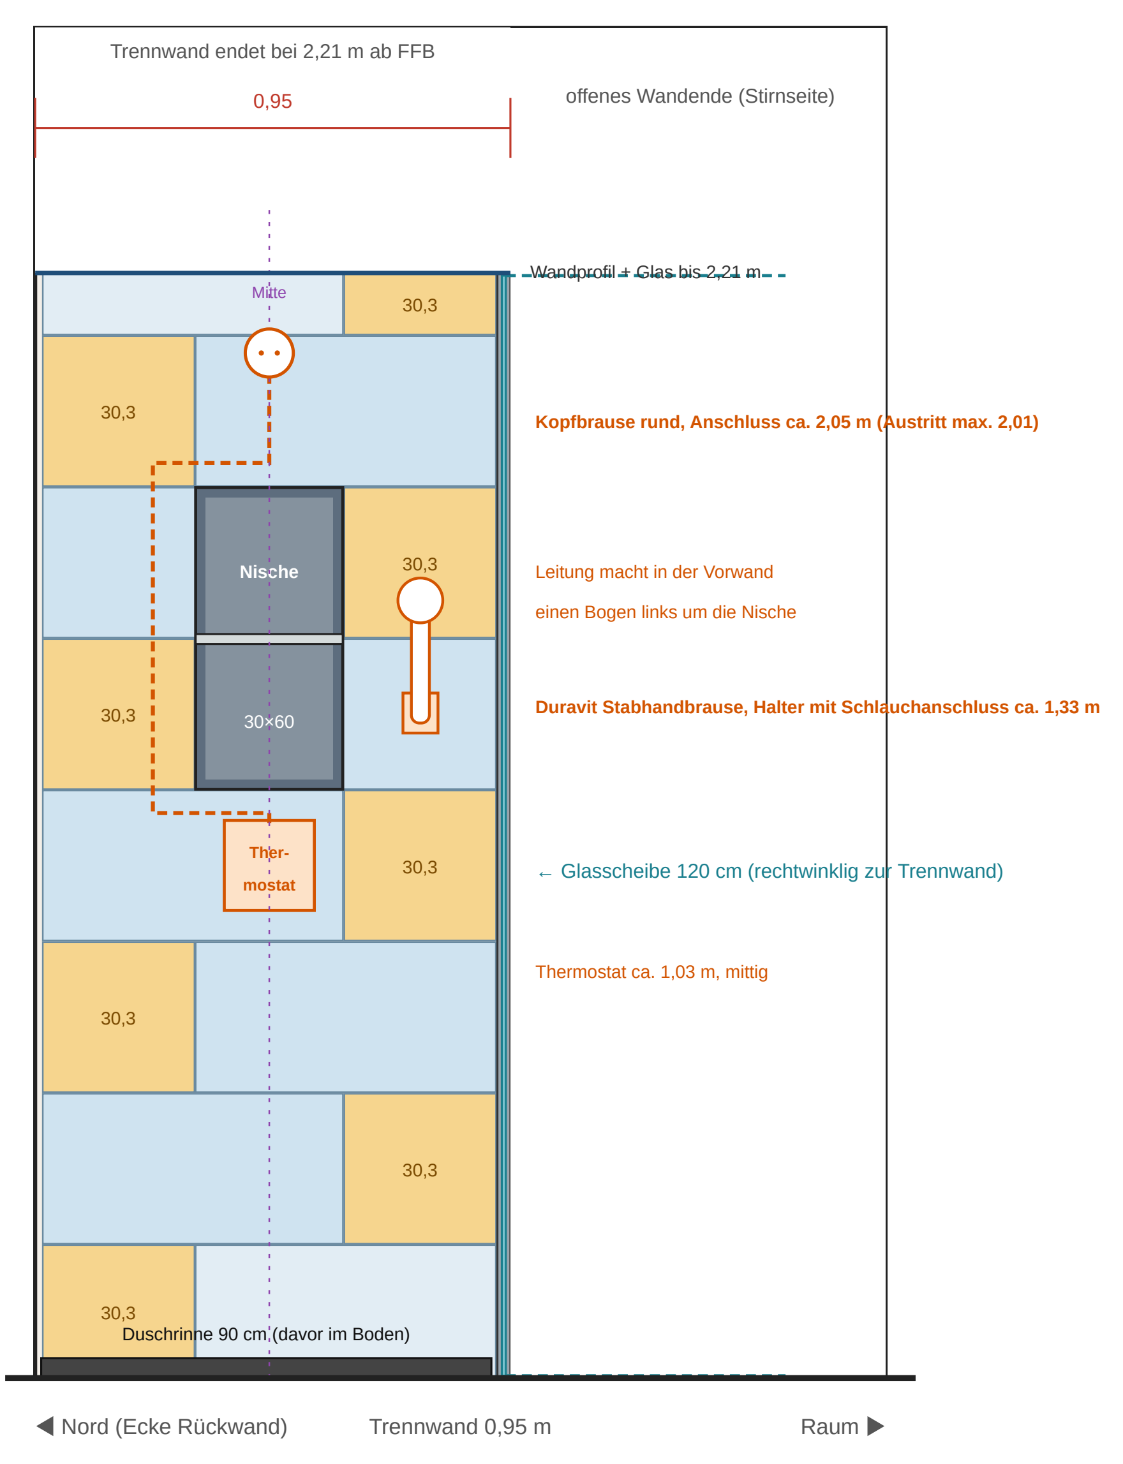
Trennwand endet bei 2,21 m ab FFB
0,95
offenes Wandende (Stirnseite)
Wandprofil + Glas bis 2,21 m
Mitte
30,3
30,3
Kopfbrause rund, Anschluss ca. 2,05 m (Austritt max. 2,01)
Nische
30×60
30,3
Leitung macht in der Vorwand
einen Bogen links um die Nische
30,3
Duravit Stabhandbrause, Halter mit Schlauchanschluss ca. 1,33 m
Ther-mostat
30,3
← Glasscheibe 120 cm (rechtwinklig zur Trennwand)
Thermostat ca. 1,03 m, mittig
30,3
30,3
30,3
Duschrinne 90 cm (davor im Boden)
◀ Nord (Ecke Rückwand)
Trennwand 0,95 m
Raum ▶

4 · Wand Waschbecken (Süden)

Blick nach Süden · Fliesen nur auf der Vorwand (bis 1,125 m) und oben auf der Ablage, darüber Putz · die ersten 1,00 m an der Tür-Seite nur Sockel

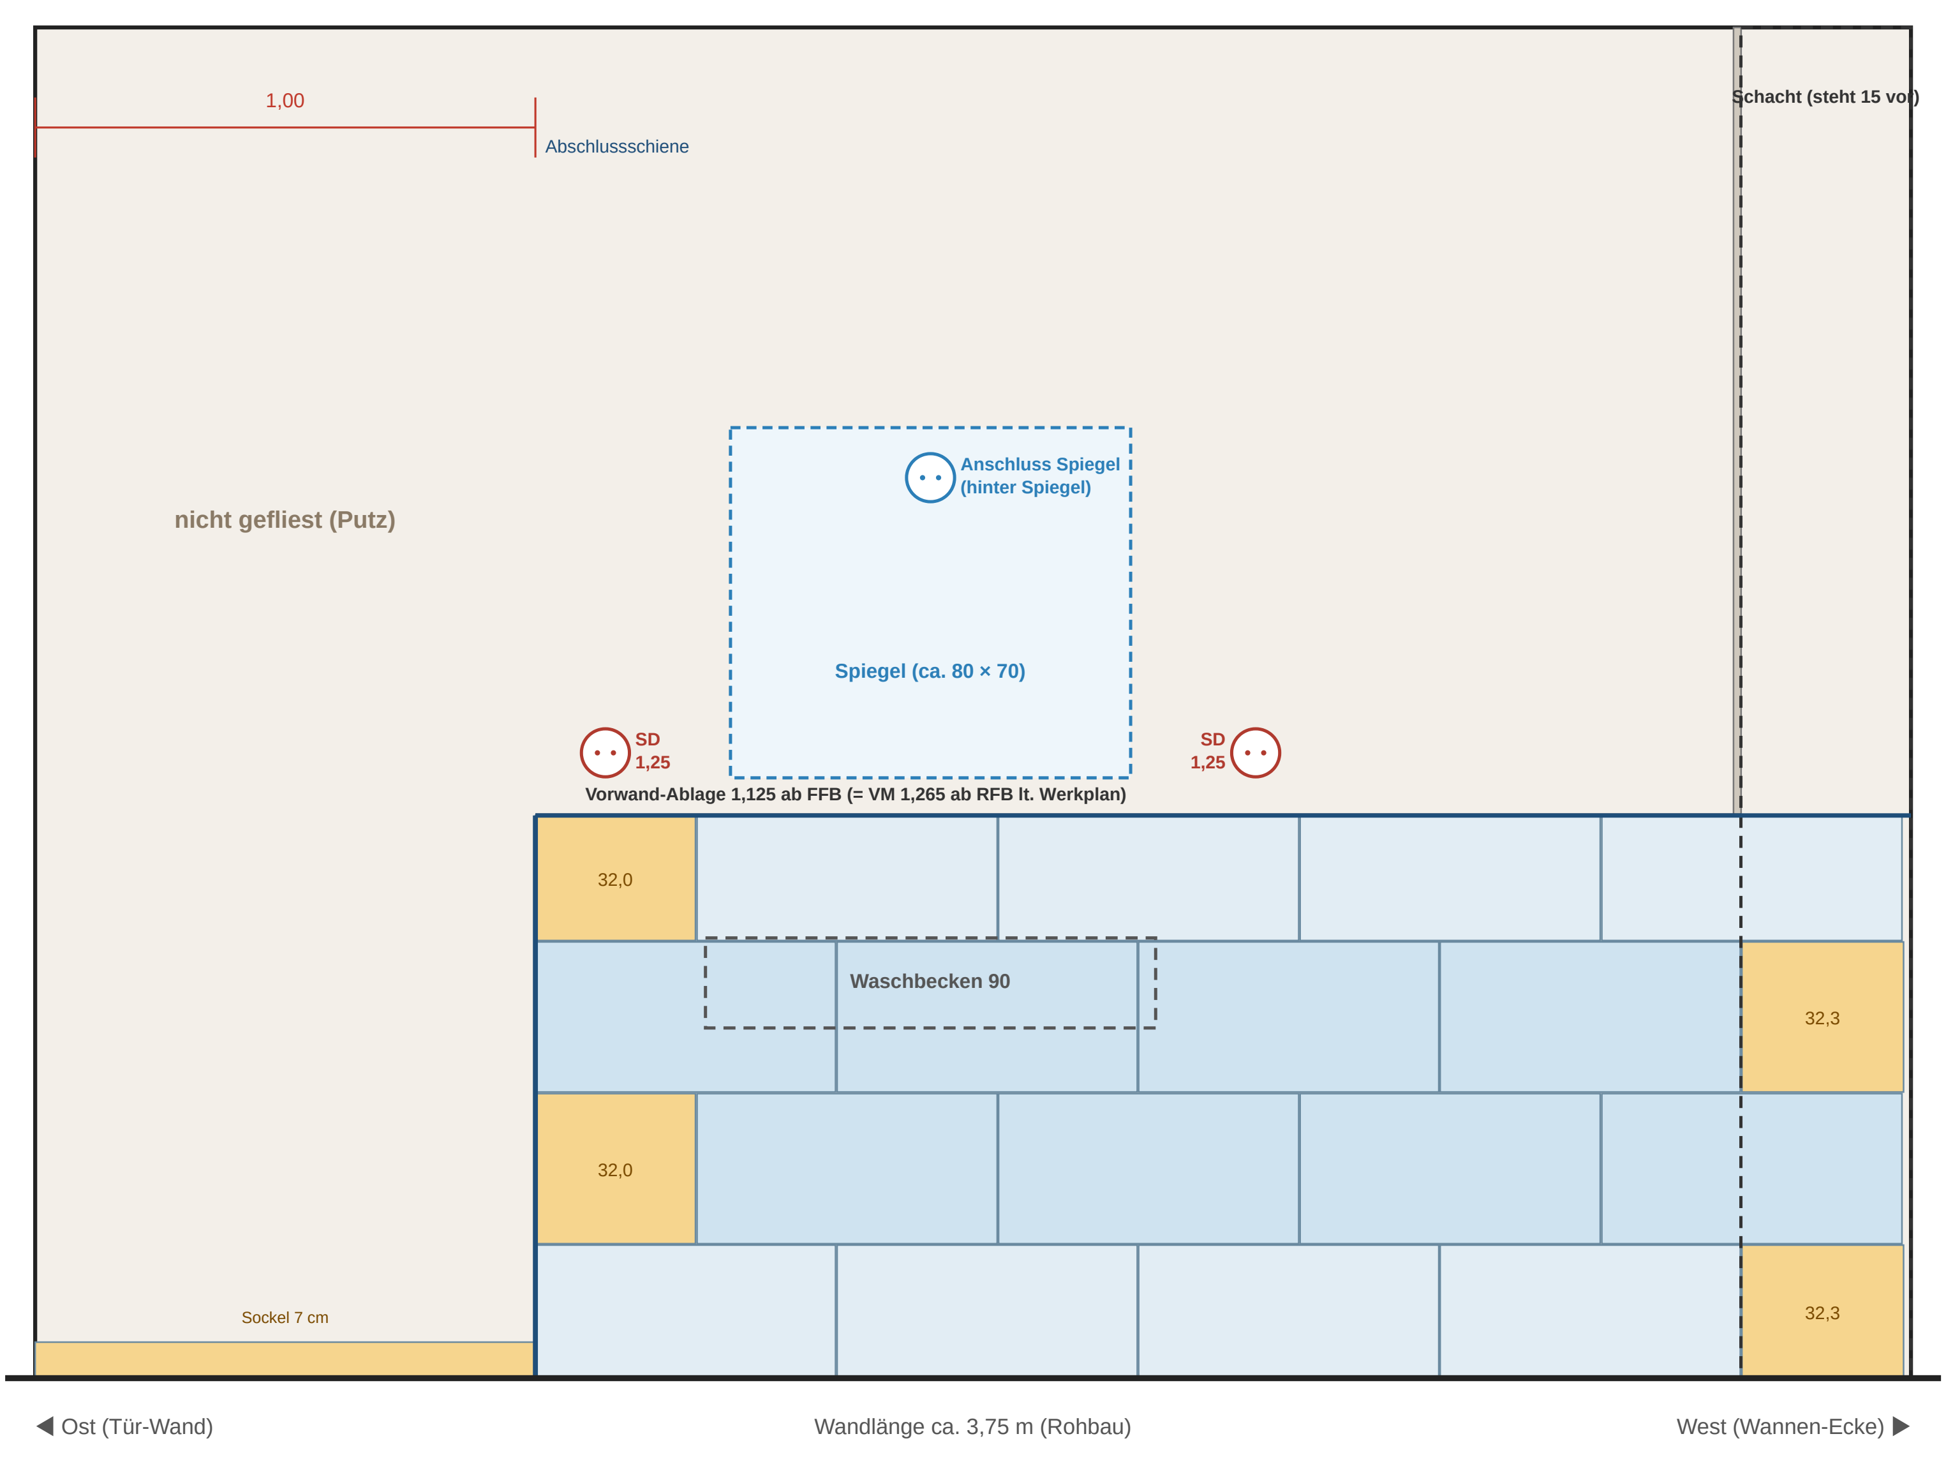

5 · Wand mit Tür (Osten)

Blick nach Osten · nicht gefliest, nur Fliesensockel 7 cm

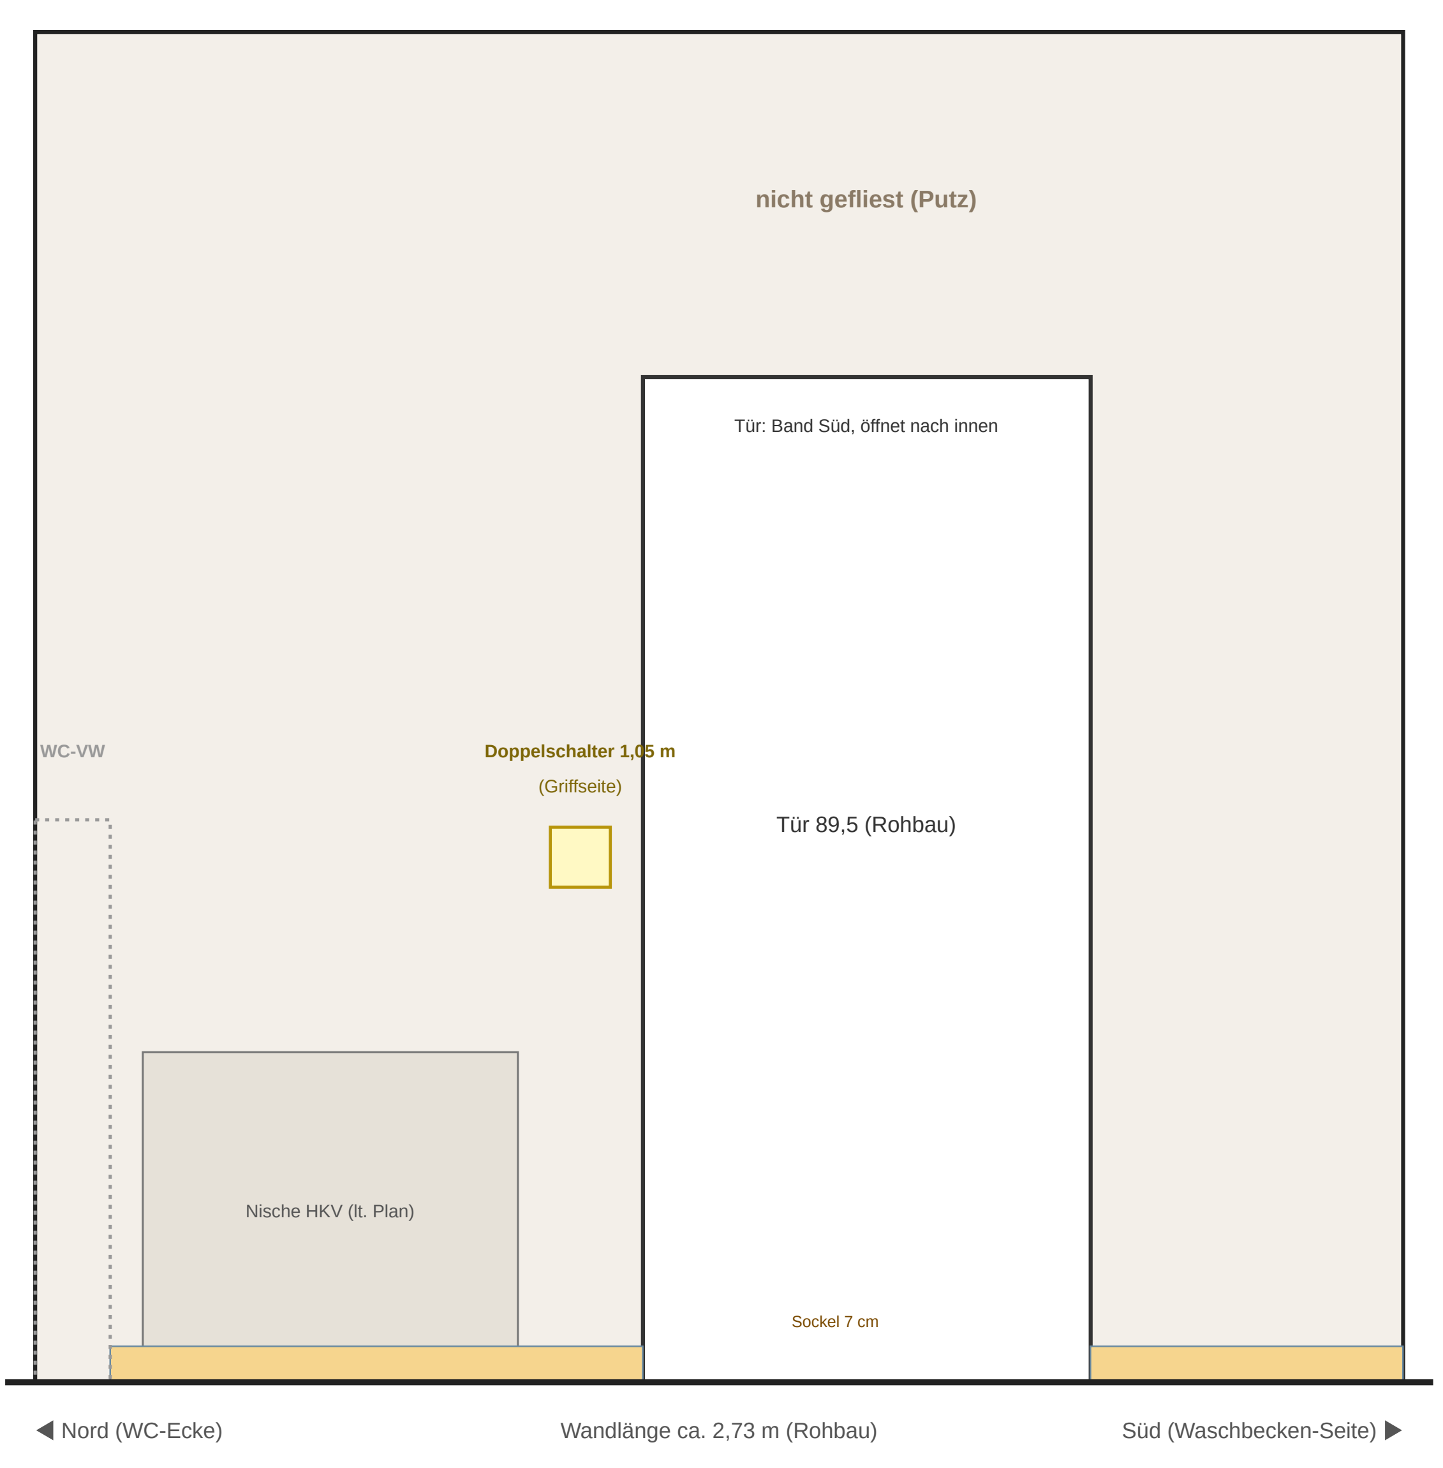

▨	ganze Fliese 60×30
☐	volle Breite, in der Höhe geschnitten
🟨	Zuschnitt (Zahl = Maß in cm)
—	Fliesenkante 2,21 m ab FFB

Fugen 3 mm · Reihenhöhen von unten: 26,6 / 6× 30 / 12,3 cm (bis 2,21 ab FFB = 2,35 ab RFB) → Fuge genau auf Fensterbank (0,875) · Maße aus Plan „03A Dachgeschoss“, auf der Baustelle nachmessen! Decke/Dachschräge vereinfacht als 2,70 m dargestellt. Ansichten jeweils „vom Raum aus auf die Wand geschaut“. Badewanne freistehend, linke Längsseite parallel zur Wand, 10 cm vor der Vorwand.

🟫	ganze Bodenfliese